© GRIMM AND PARKER, P.C. 2014

TAGGED NOTES	
A77	REFER TO SHEET M4.0 FOR MECHANICAL ROOM - CENTRAL 2101 HEAT PUMPS AND CORRESPONDING TAGS INDICATING ROOM/S SERVED.

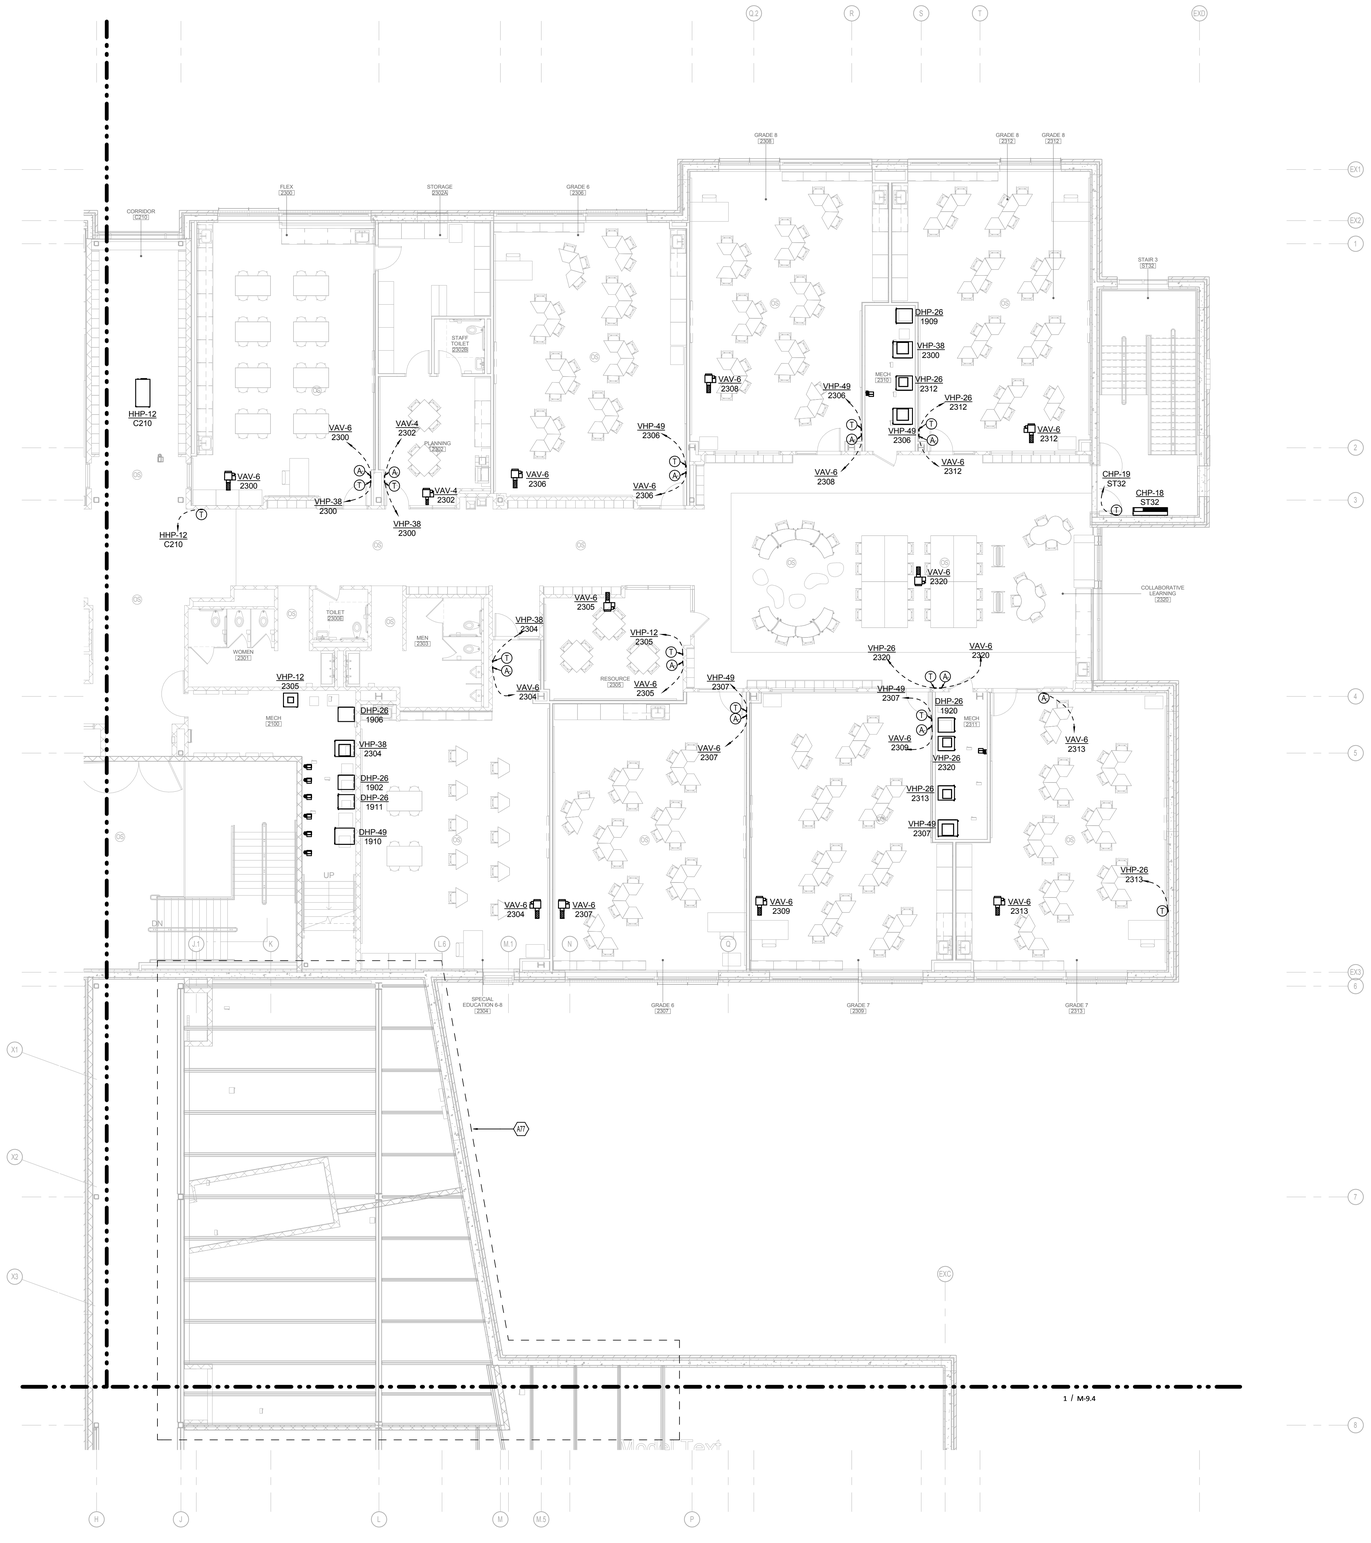

1 Second Floor - Mechanical Controls - Area C

SCALE: 1/8" = 1'-0"

0 2' 4' 8' 16' 24' 32'

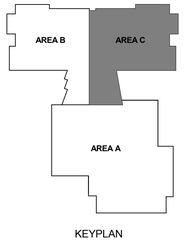

KEYPLAN

N

2429 Members Way
Lexington, Ky 40504
Tel: 859.253.0892
http://www.cmtaegs.com/

11720 Beltsville Drive
Suite 600
Calverton, MD 20705
Tel: 301.595.1000
www.grimmandparker.com

GRIMM AND PARKER

GP# 21553

HVAC CONTORLS - SECOND FLOOR AREA C

HOLABIRD ACADEMY PK-8
CITY OF BALTIMORE, MARYLAND

DATE	DESCRIPTION

M-9.5

03/13/2017
BID SET

© GRIMM AND PARKER, P.C. 2014