© GRIMM AND PARKER, P.C. 2014

## SHEET KEY NOTES

1. EMERGENCY STORM DRAIN DISCHARGE TO GRADE PIPE 18"-24" ABOVE FINISHED GRADE. PROVIDE DISCHARGE NOZZLE WITH SCREEN. COORDINATE WITH CIVIL PLANS FOR GRADE ELEVATION.
2. PROVIDE ACCESS PANELS TO ALL DOMESTIC SUPPLY VALVES.
3. PROVIDE ACCESS PANELS TO ALL WATER HAMMER ARERESTORS. REFER TO PLUMBING RISER DIAGRAM FOR WATER HAMMER ARRESTOR LOCATION.




1 P-1.3H PLUMBING PARTIAL FIRST FLOOR PLAN – AREA C

SCALE: 1/8" = 1'-0"

## KEY PLAN

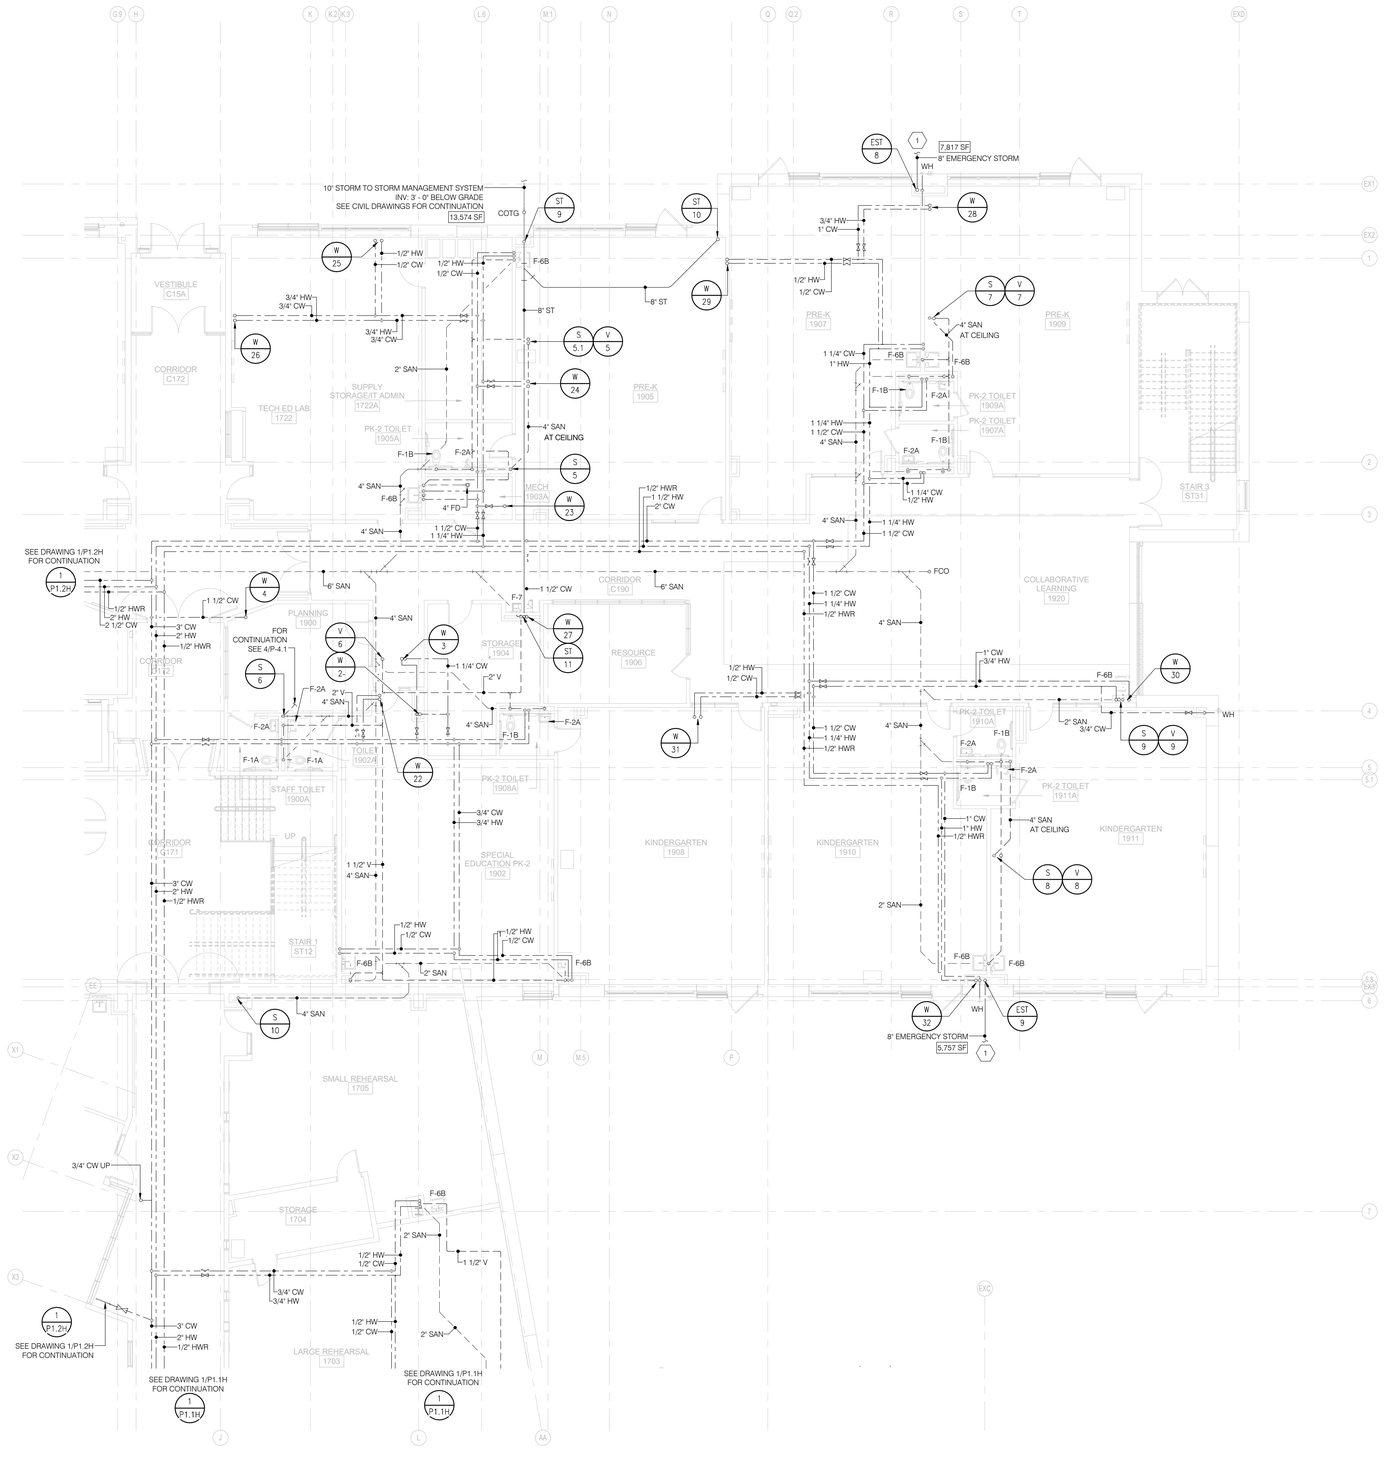


SETTY
ONE SOUTH STREET, SUITE 1110
BALTIMORE, MARYLAND 21202
TEL 667-329-5035
MAINTENANCE MANAGEMENT · ENERGY MANAGEMENT
ENERGY MANAGEMENT SERVICES · OPERATION AND SERVICES
CONSULTING · ENGINEERING · DESIGN · CONSTRUCTION
DISTRICT OF COLUMBIA · MARYLAND
www.SETTY.com
SAD/CITY # # # # #
PROJECT NUMBER

11720 Beltsville Drive
Suite 600
Calverton, MD 20705
Tel: 301.595.1000
www.grimmandparker.com

G+P GRIMM AND PARKER
GP# 21553

PLUMBING PARTIAL FIRST FLOOR PLAN – AREA C

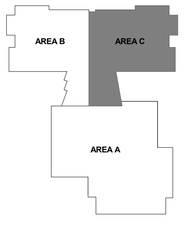HOLABIRD ACADEMY PK-8
CITY OF BALTIMORE, MARYLAND

| DATE | DESCRIPTION |
|---|---|
| | |

**P-1.3H**

03/13/2017
BID SET

© GRIMM AND PARKER, P.C. 2014