NOTES THIS SHEET:

1. OUTLETS TO BE INSTALL TO OUTSIDE EDGE OF TV. COORDINATE WITH DUAL TV ELEVATIONS.
2. LOCATION OF AIPHONE STATION. COORDINATE EXACT LOCATION FOR OUTLET BOX AND CONCEALED CONDUIT.
3. PLYWOOD PANELS 8'X4'X3/4", "A/B WITH A SIDE TO THE OUTSIDE WRAPPING THE ROOM" AT 6" OFF THE FLOOR.
4. ROUTE CONCEALED CONDUIT AS HIGH AS POSSIBLE TO NEAREST CONCEALED CEILING VOID.

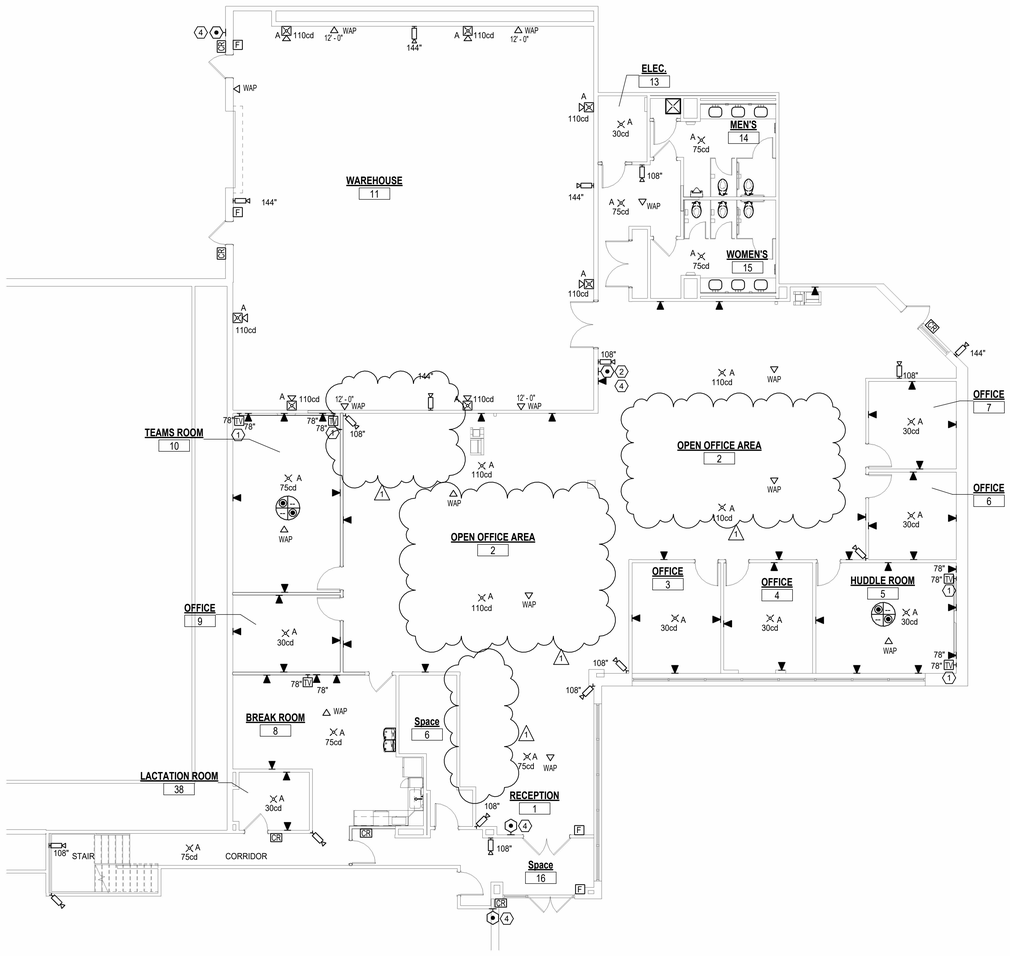

1 E4.1 FIRST FLOOR ELECTRICAL LOW VOLTAGE NEW WORK PLAN

SCALE: 1/8" = 1'-0"

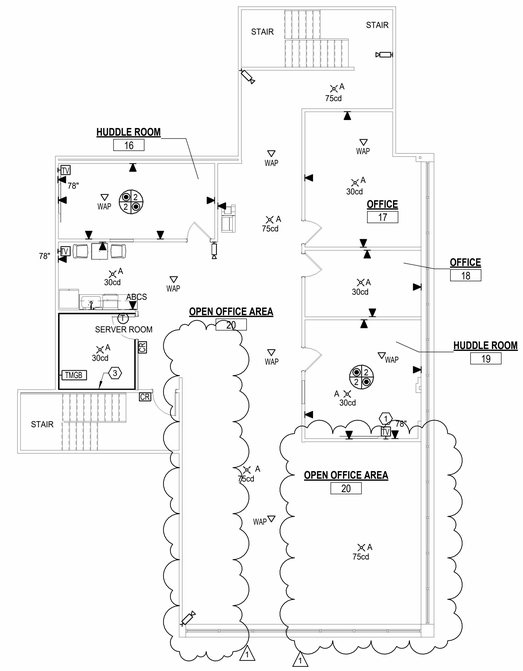

2 E4.1 SECOND FLOOR ELECTRICAL LOW VOLTAGE NEW WORK PLAN

SCALE: 1/8" = 1'-0"

SAMAHA

10521 Rosehaven Street, Suite 200 Fairfax, VA 22030
Phone 703-691-3311 Fax 703-691-3316

ASCENT ENGINEERING GROUP
5228 VALLEYPOINTE PKWY, SUITE 4
ROANOKE, VIRGINIA 24019
(540) 265-4444

D: 2024-0030 C:

LOUDOUN COUNTY PRCS

750 MILLER DR
LEESBURG, VA 20175

BID SET

LOUDOUN COUNTY

NO	REVISION	DATE
1	Addendum 1	08/30/2024

Sheet Title:

ELECTRICAL LOW VOLTAGE NEW WORK PLANS

Issue Date: 7/24/2024

Sheet Number:

E4.1

Sheet No. in Set: Total No. Sheets: -

Project Number: XXXXXX
Drawn By: Author
Checked By: Checker