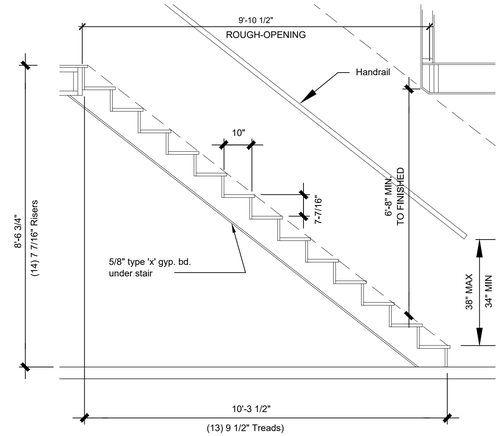

TYP. STAIR DETAIL

SCALE: NTS

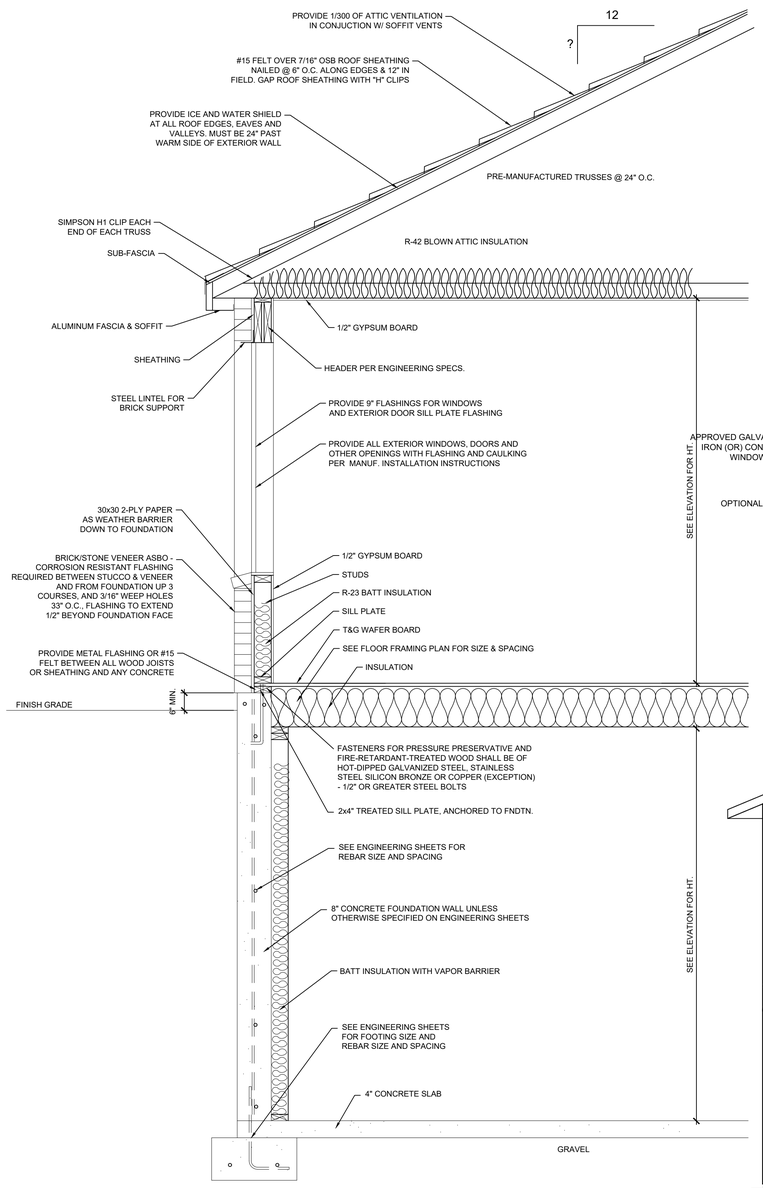

TYP. WALL SECTION DETAIL

SCALE: ¾" = 1'-0"

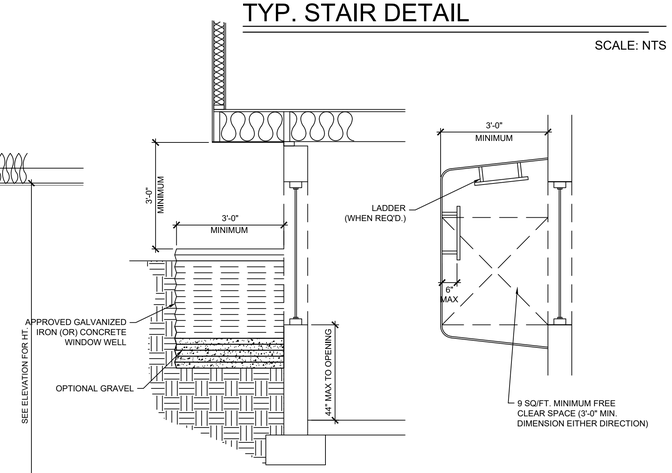

TYP. WINDOW WELL DETAIL

SCALE: NTS

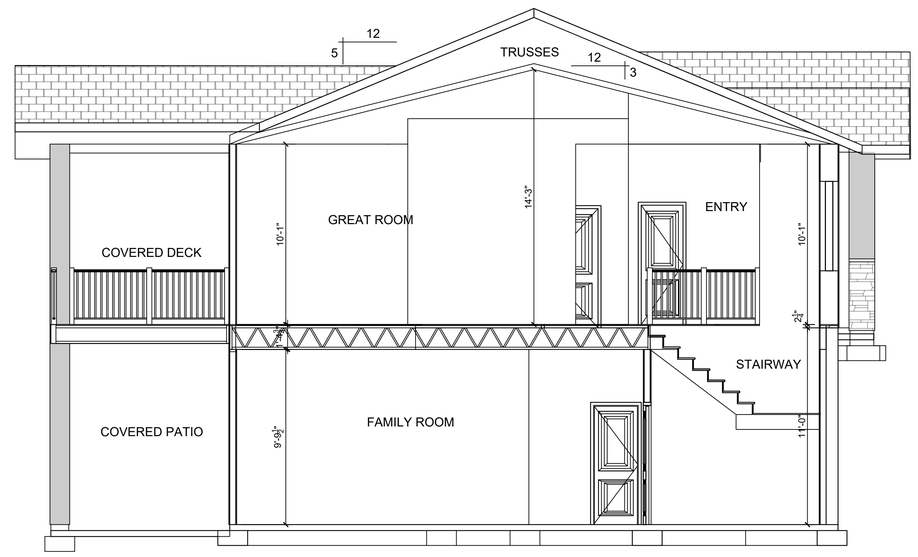

1 SECTION

SCALE: ¼" = 1'-0"

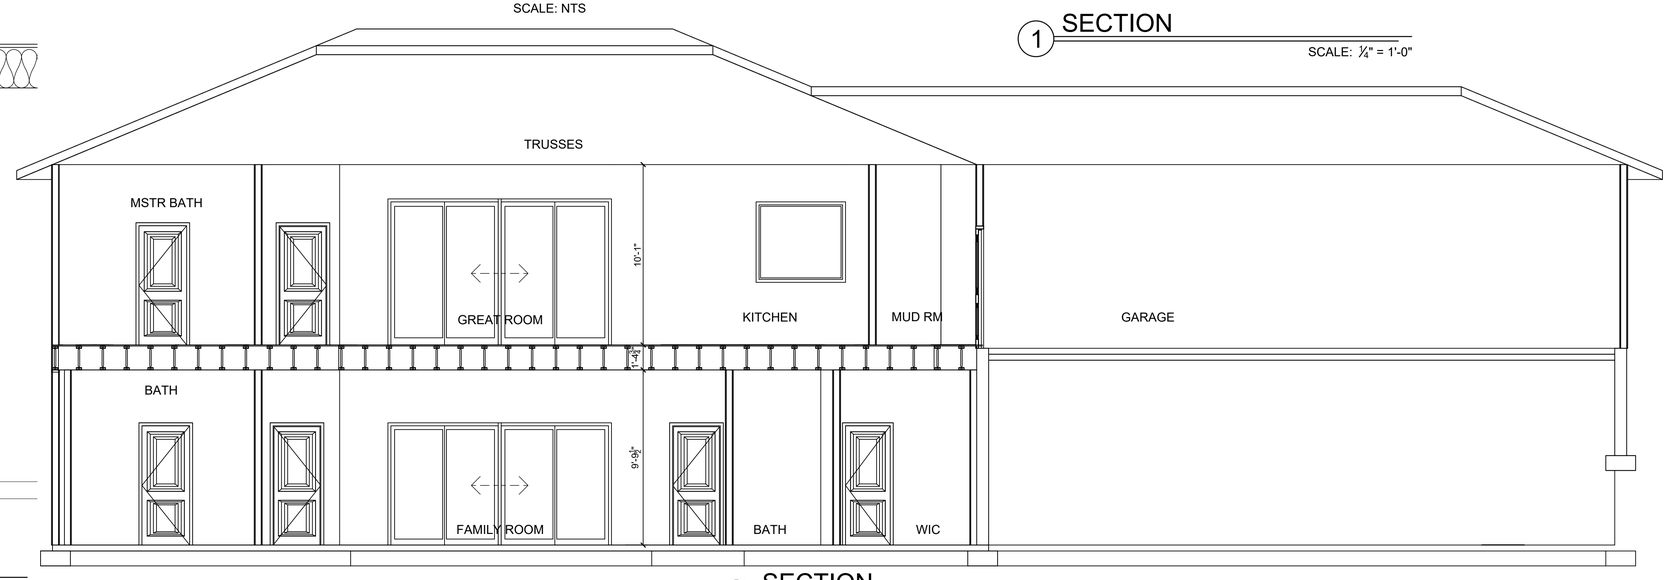

2 SECTION

SCALE: ¼" = 1'-0"

DRAWN BY	JLF
PROJECT #	20-142
REV.1	-
REV.2	-
FINAL REV.	1/11/2021

COOPER RESIDENCE
305 W. Shangri-La
Toquerville, UT 84774

BUILDING SECTIONS

J. LONNIE FOX
DRAFTING AND DESIGN
phone: (801) 987-1442 • jlonniefox@gmail.com • www.jlfdraftingdesign.com

BASEMENT SQFT	1713
MAIN FLR SQFT	1705
2ND FLR SQFT	0
GARAGE SQFT	909
TOTAL FIN SQFT	3418
TOTAL SQFT	3418

SHEET #
A3.1

COPYRIGHT 2020 J. LONNIE FOX DRAFTING AND DESIGN. THE PURCHASER IS GRANTED A SINGLE USE LICENSE FOR CONSTRUCTION ONLY. THESE PLANS ARE COPYRIGHTED AND ARE SUBJECT TO COPYRIGHT PROTECTION AS AN "ARCHITECTURAL WORK" UNDER THE COPYRIGHT ACT.