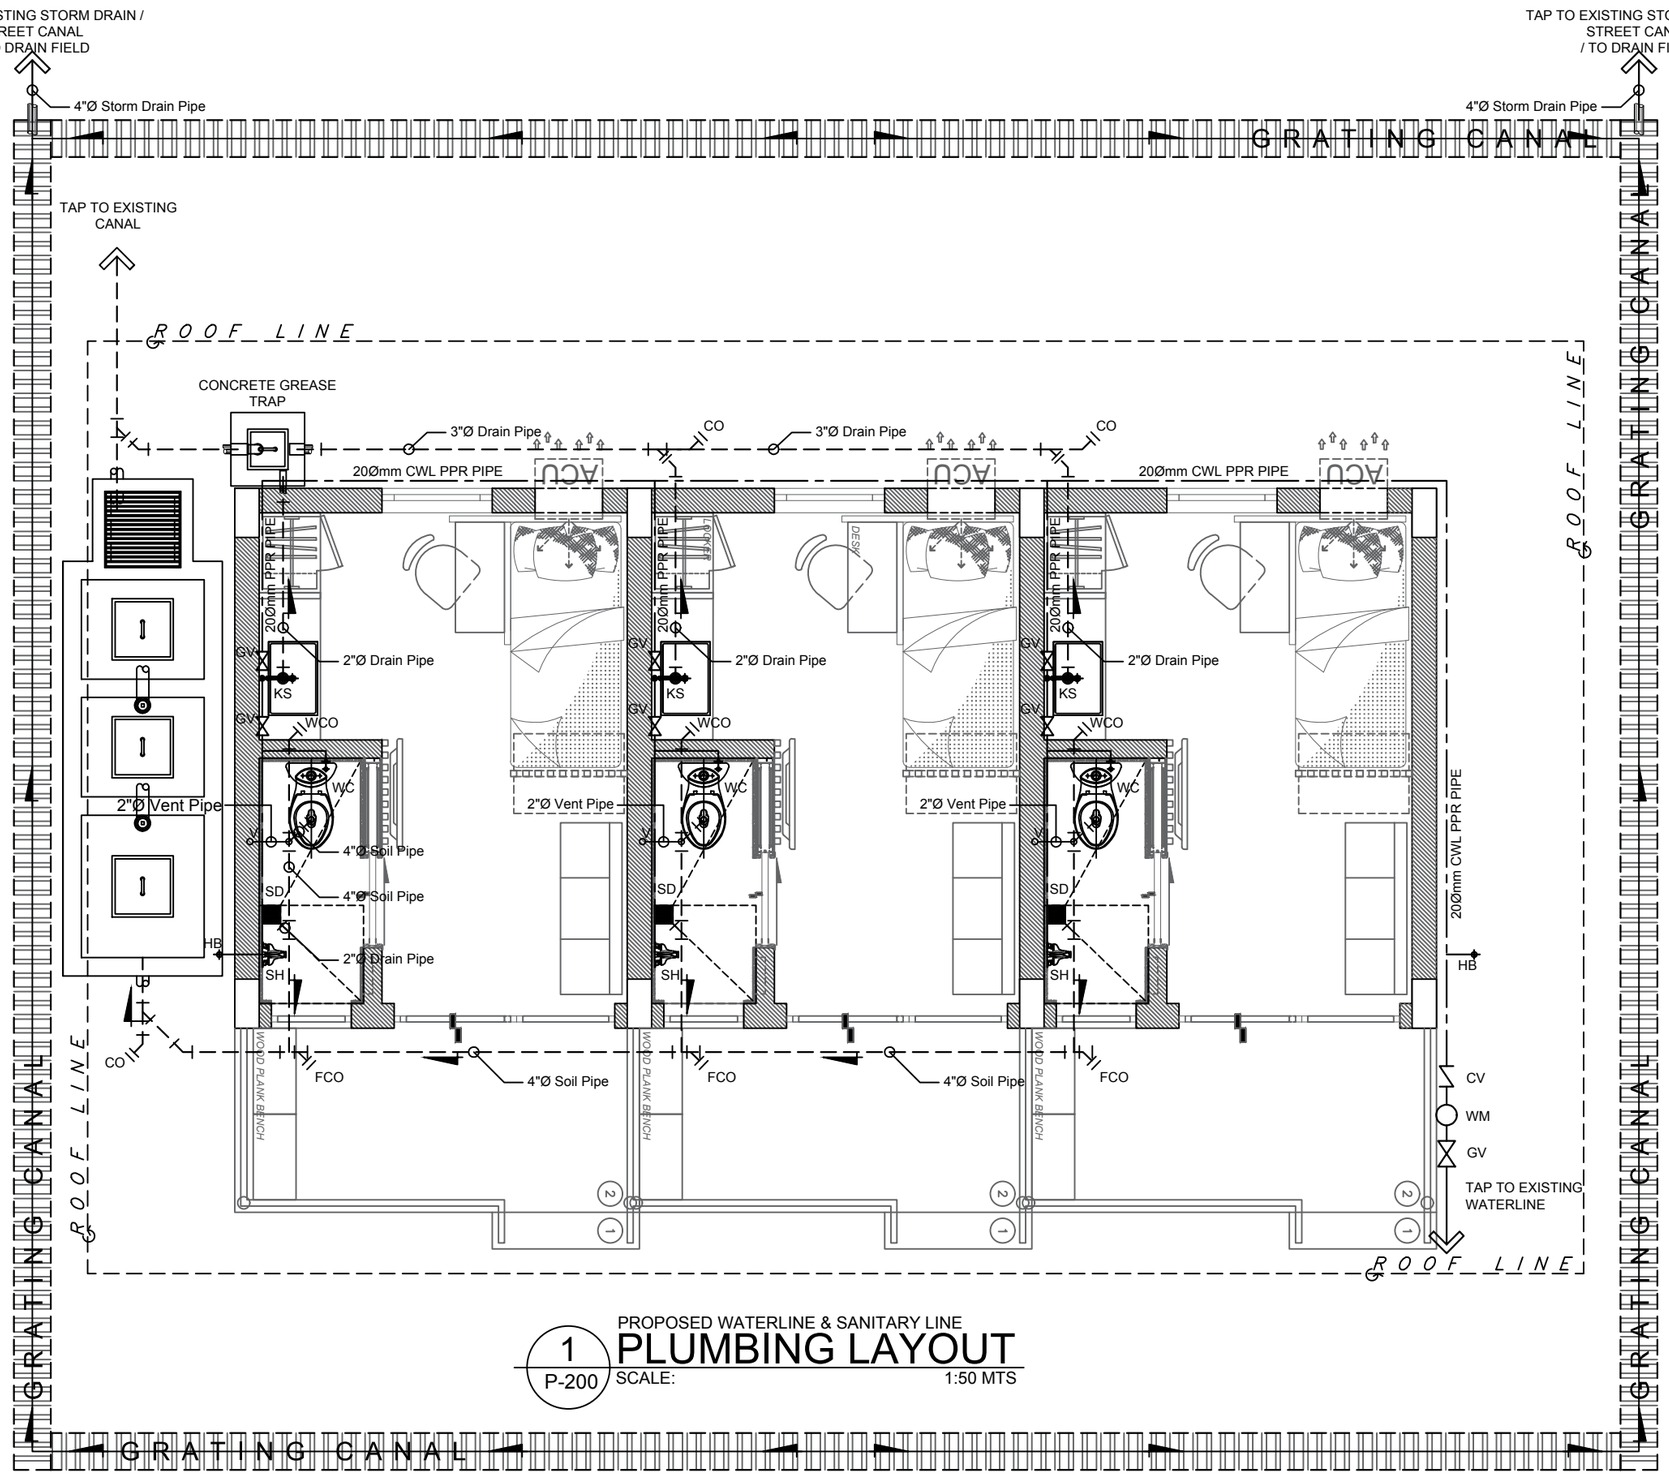

PROPOSED WATERLINE & SANITARY LINE

PLUMBING LAYOUT

1 / P-200

SCALE: 1:50 MTS

LEGEND:	
WATER SUPPLY:	
CV	– Check Valve
WM	– Water Meter
GV	– Gate Valve
FAU	– Faucet
SH	– Shower Head
FIXTURES:	
WC	– Water Closet
FD	– Floor Drain
SD	– Shower Drain
KS	– Kitchen Sink
WASTE LINE:	
CO	– Clean Out
V	– Vent
VTR	– Vent Thru Roof

WATER SUPPLY LINE

SANITARY LINE

STORM DRAIN LINE

REPUBLIC OF THE PHILIPPINES
DEPARTMENT OF SOCIAL WELFARE AND DEVELOPMENT
PRK. BUMANAAG, BRGY.ZONE III,
KORONADAL CITY, SOUTH COTABATO, FO XII

PREPARED BY:
ENGR. CRESSYL ANN E. BANTAYA
TECHNICAL FACILITATOR

CHECKED BY:
ENGR. FRANCIS C. ESTOMATA
PDO III

RA 9266 SECTION 33

Drawings and specifications and other contract documents duly signed, stamped or sealed, as instruments of service, are the intellectual property and documents of the architect, whether the object for which they are made is executed or not. It shall be unlawful for any person to duplicate or make copies of said documents for use in the repetition of and for other projects or buildings, whether executed partly or in whole, without the written consent of the architect or author of said documents.

REVIEWED AND VERIFIED BY:
ENGR. ROLLY A. TEOFILO
PDO IV FOR INFRA

PROJECT TITLE:
CONSTRUCTION OF 2-UNITS ISOLATION BUIDLING (11-ROOMS)

LOCATION:
RRCY, BRGY. BUKAY PAIT, TANTANGAN, SOUTH COTABATO

APPROVED BY:
CEZARIO JOEL C. ESPEJO
REGIONAL DIRECTOR
DSWD - FIELD OFFICE XII

SHEET CONTENT
PLUMBING LAYOUT
WATERLINE
STORM DRAIN LINE
SANITARY LINE

REVISIONS		
MARK	DATE	

PROJECT NO.		SHEET NO.
DRAWN BY :	CEB	P-200
DESIGNED BY :		
DATE :	--	
CHECKED BY :	FCE	SCALE: A3 AS SHOWN / A1