PRODUCED BY AN AUTODESK STUDENT VERSION

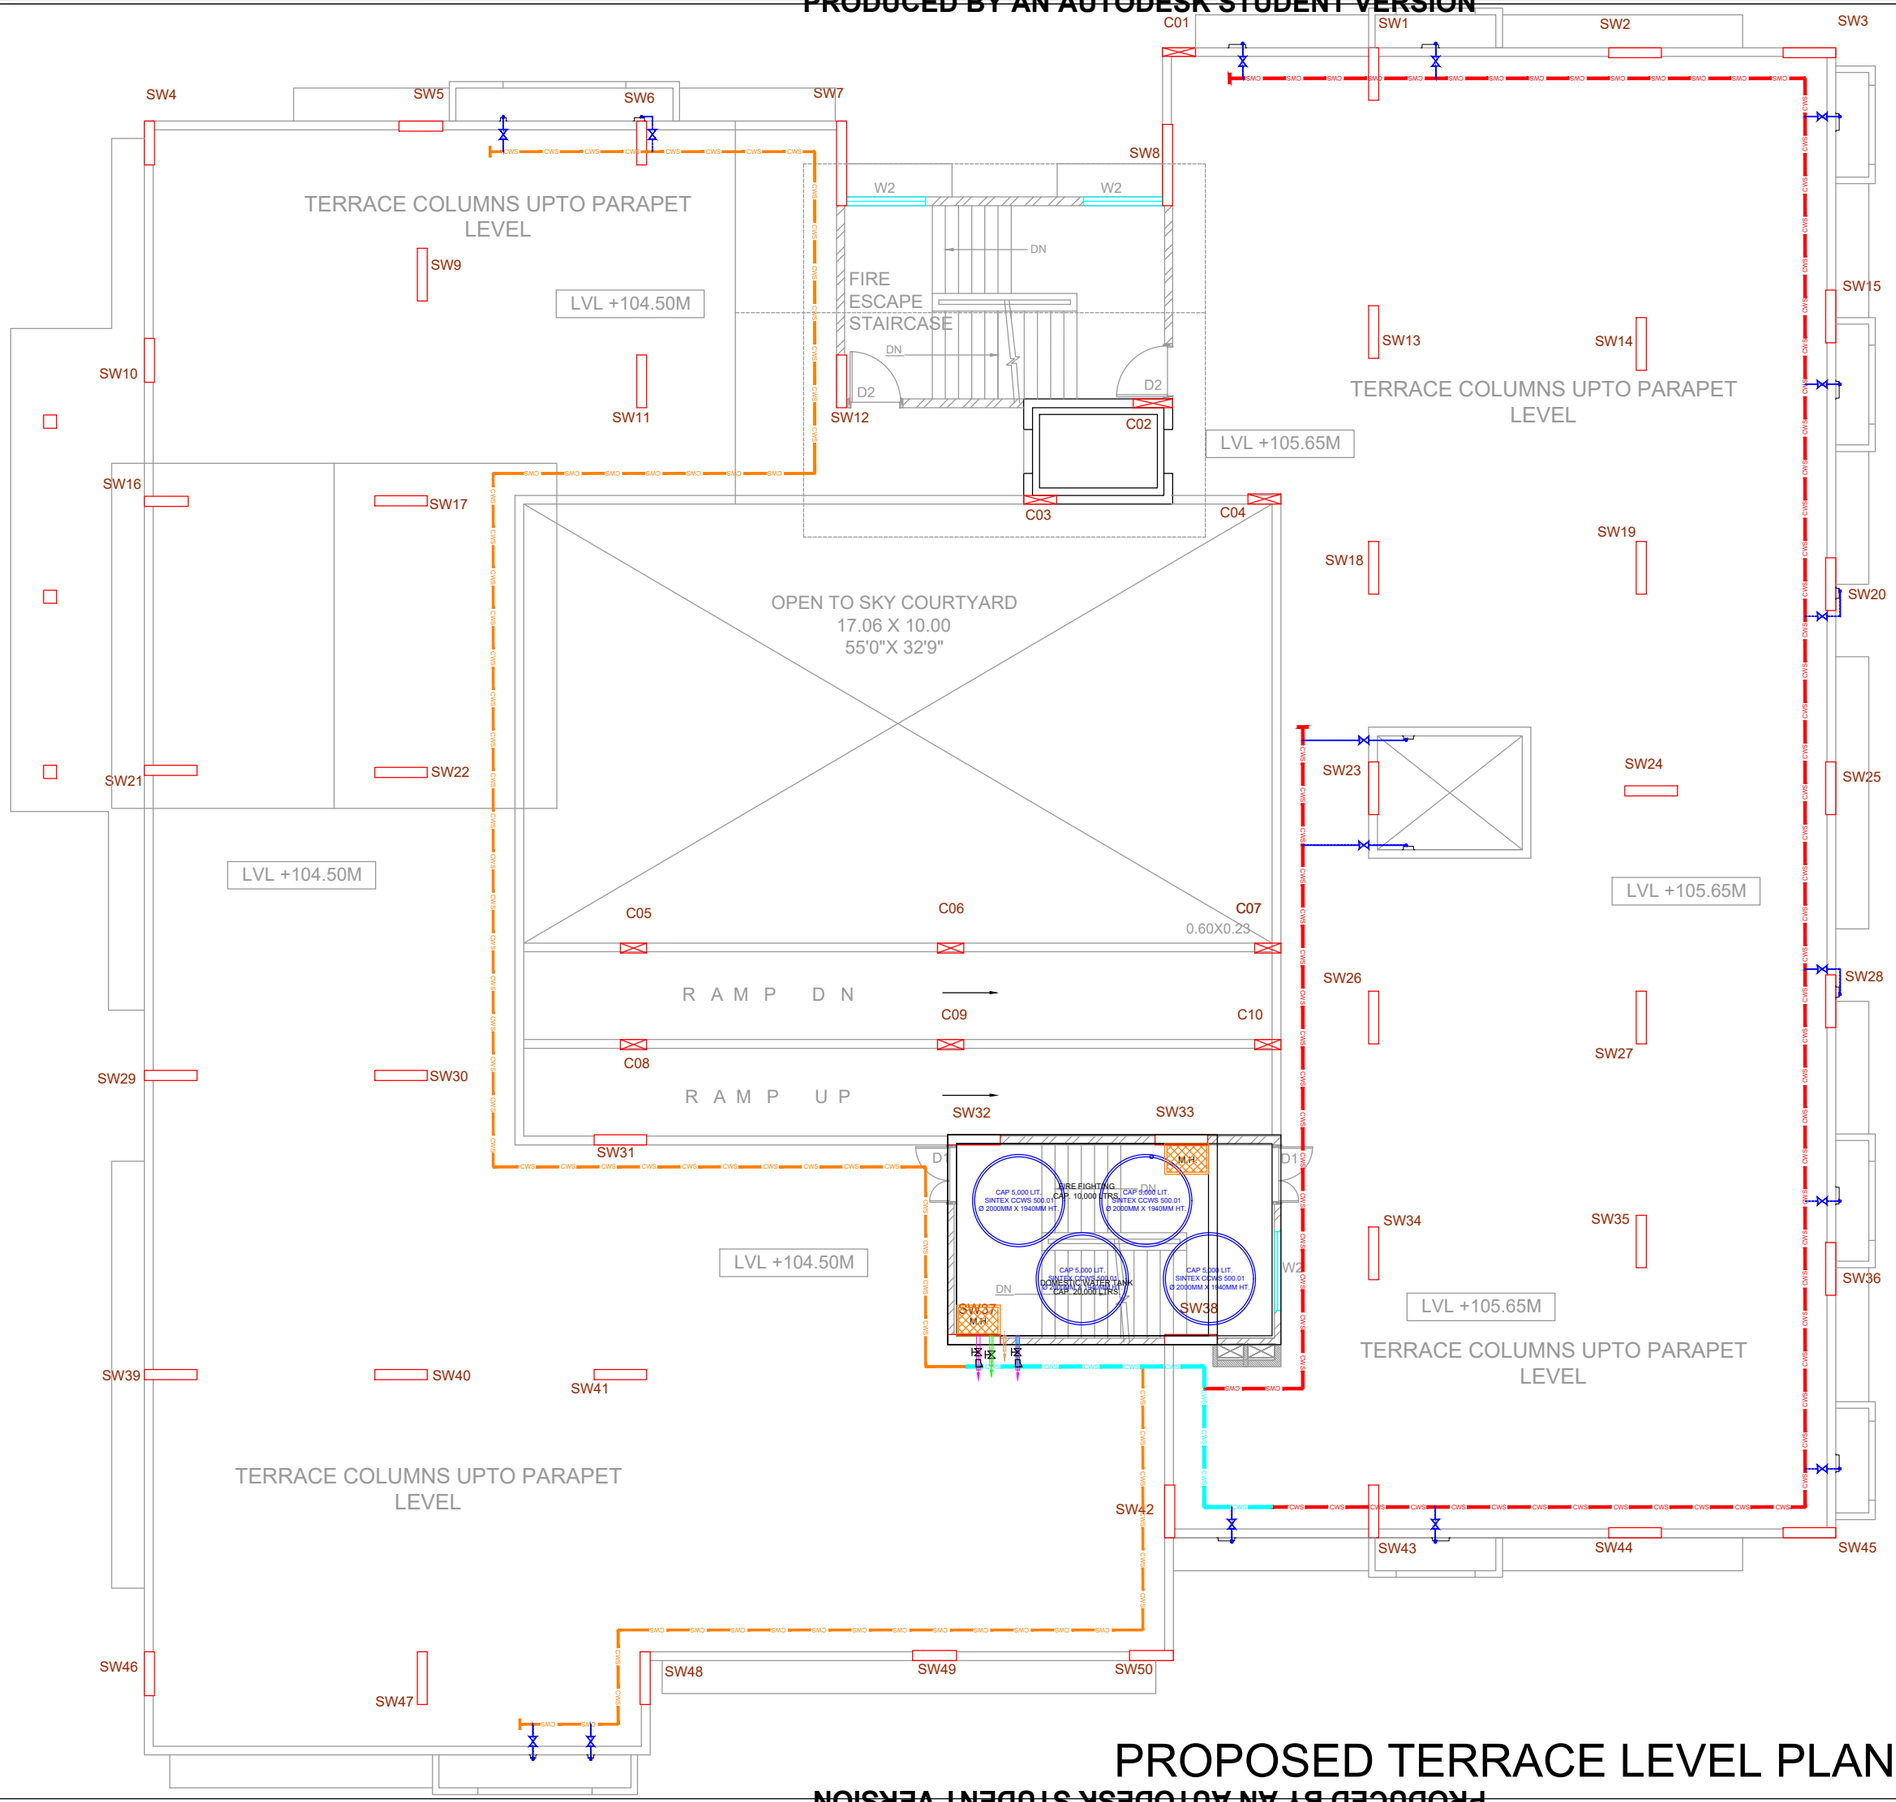

PROPOSED TERRACE LEVEL PLAN

DRG NO.	M/167/08	01/01
	R3	

STAMP & SIGNATURE

McLIN Consultants Pvt. Ltd. FOR APPROVAL Pune-30

NOTES:

CWS	DOMESTIC WATER LINE Ø 80MM
CWS	DOMESTIC WATER LINE Ø 65MM
CWS	DOMESTIC WATER LINE Ø 50MM

REV NOS	DATE	REMARK / SUBJECT
R5		
R4		
R3	01.04.21	REVISED ARCH. PLAN
R2	10.01.20	REVISED ARCH. PLAN
R1	28.11.19	REVISED ARCH. PLAN

REVISIONS

DRAWING TITLE	TERRACE WATER DISTRIBUTION LOOP
PROJECT	ARC AUTISM RESEARCH & TRAINING CENTRE

McLIN CONSULTANTS PVT.LTD.
CONSULTANCY IN PLUMBING AND ENVIRONMENTAL ENGINEERING
'GIRIJA' 5, Sitabaug Colony, Vithalwadi Road,
Pune - 411 030 Tel - 2432 0010
e-mail - mclincpl@gmail.com

CLIENT	MR. SUBHASH LELE	
ARCHITECT	INDESIGN ARCHITECTS	
NORTH	DATE:-	26.11.2019
	DRAWN BY	PANKAJ G.
	CHECKED BY	MOHANISH P.
	APPROVED BY	MOHANISH P.
SCALE:-NTS		

C:\Users\Dell\Downloads\ARC Plumbing Drawings (1)\ARC Plumbing Drawings\R3 Terrace Loop Detail 01.04.21.dwg

PRODUCED BY AN AUTODESK STUDENT VERSION
PRODUCED BY AN AUTODESK STUDENT VERSION
PRODUCED BY AN AUTODESK STUDENT VERSION