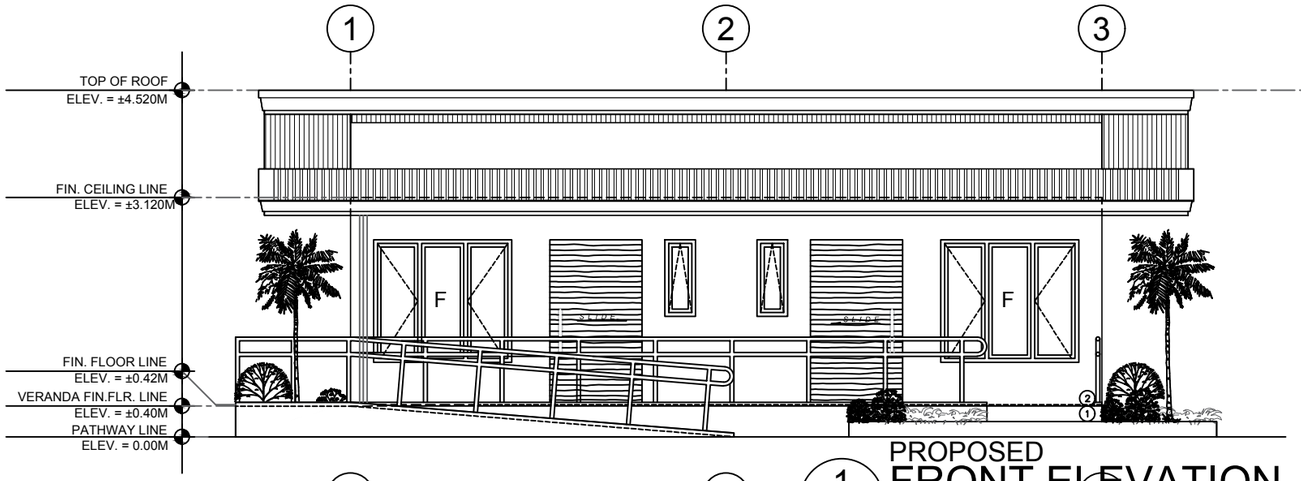

PROPOSED
1 A-300 FRONT ELEVATION
SCALE: 1:80 MTS

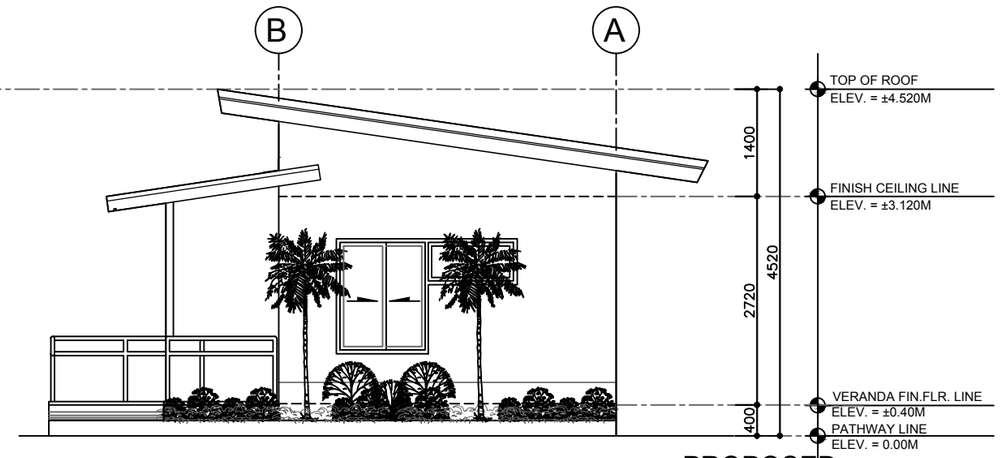

PROPOSED
2 A-300 RIGHT ELEVATION
SCALE: 1:80 MTS

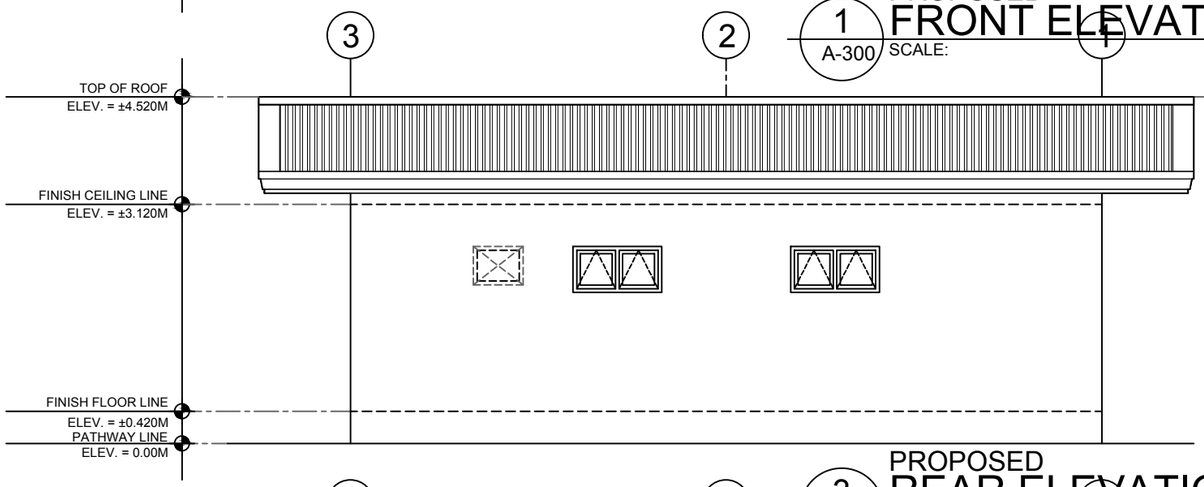

PROPOSED
3 A-300 REAR ELEVATION
SCALE: 1:80 MTS

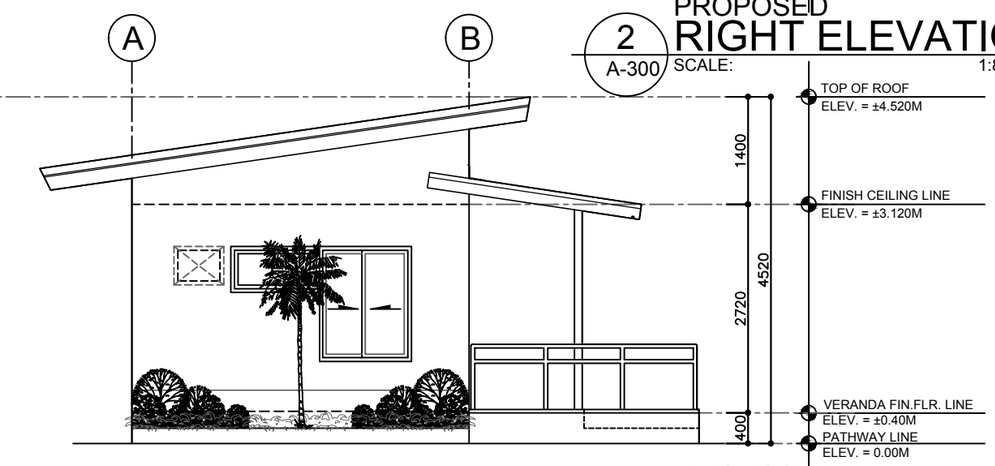

PROPOSED
4 A-300 LEFT ELEVATION
SCALE: 1:80 MTS

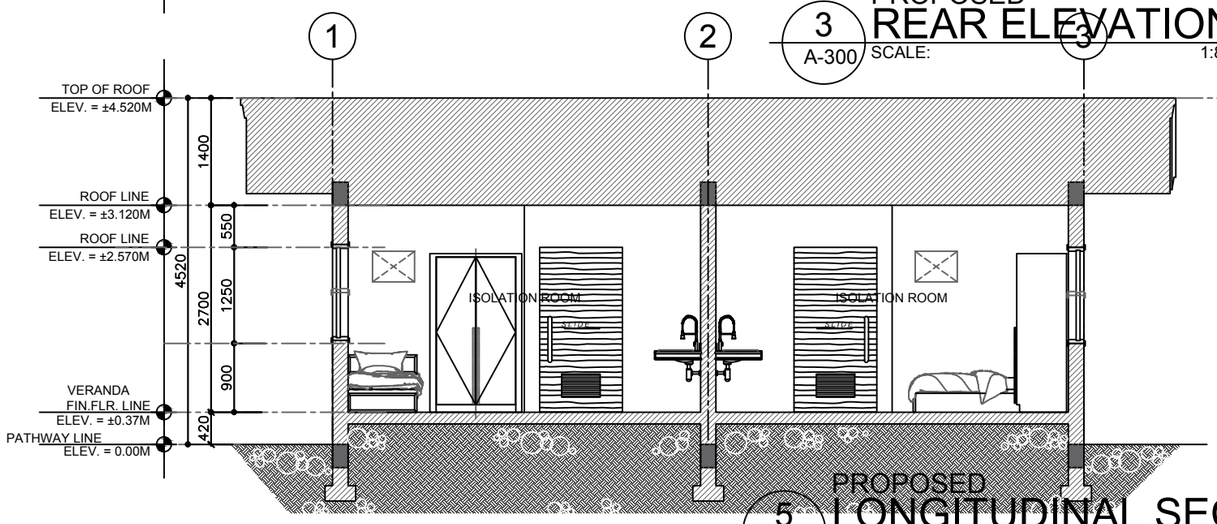

PROPOSED
5 A-300 LONGITUDINAL SECTION
SCALE: 1:80 MTS

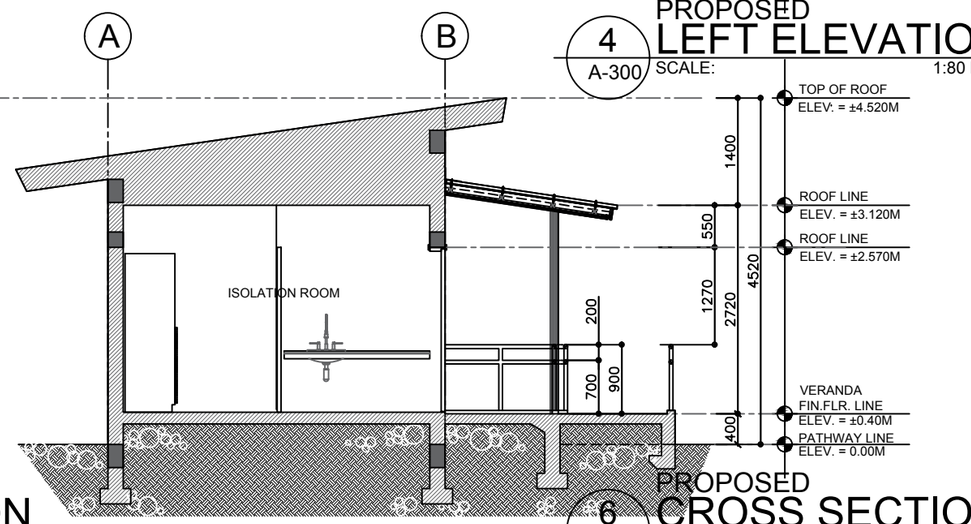

PROPOSED
6 A-300 CROSS SECTION
SCALE: 1:80 MTS

REPUBLIC OF THE PHILIPPINES
DEPARTMENT OF SOCIAL WELFARE AND DEVELOPMENT
PRK. BUMANAAG, BRGY.ZONE III,
KORONADAL CITY, SOUTH COTABATO, FO XII

PREPARED BY:	RA 9266 SECTION 33	REVIEWED AND VERIFIED BY:	PROJECT TITLE:	APPROVED BY:	SHEET CONTENT	REVISIONS	PROJECT NO.	SHEET NO.
ENGR. CRESSYL ANN E. BANTAYA TECHNICAL FACILITATOR CHECKED BY: ENGR. FRANCIS C. ESTOMATA PDO III	*Drawings and specifications and other contract documents duly signed, stamped or sealed, as instruments of service, are the intellectual property and documents of the architect, whether the object for which they are made is executed or not. It shall be unlawful for any person to duplicate or make copies of said documents for use in the repetition of and for other projects or buildings, whether executed partly or in whole, without the written consent of the architect or author of said documents.*	ENGR. ROLLY A. TEOFILO PDO IV FOR INFRA	CONSTRUCTION OF 2-UNITS ISOLATION BUIDLING (11-ROOMS) LOCATION: RRCY, BRGY. BUKAY PAIT, TANTANGAN, SOUTH COTABATO	CEZARIO JOEL C. ESPEJO REGIONAL DIRECTOR DSWD - FIELD OFFICE XII	ELEVATION SECTION	MARK / DATE	DRAWN BY : CEB DESIGNED BY : DATE : -- CHECKED BY : FCE	A-300 SCALE A3 AS SHOWN A1