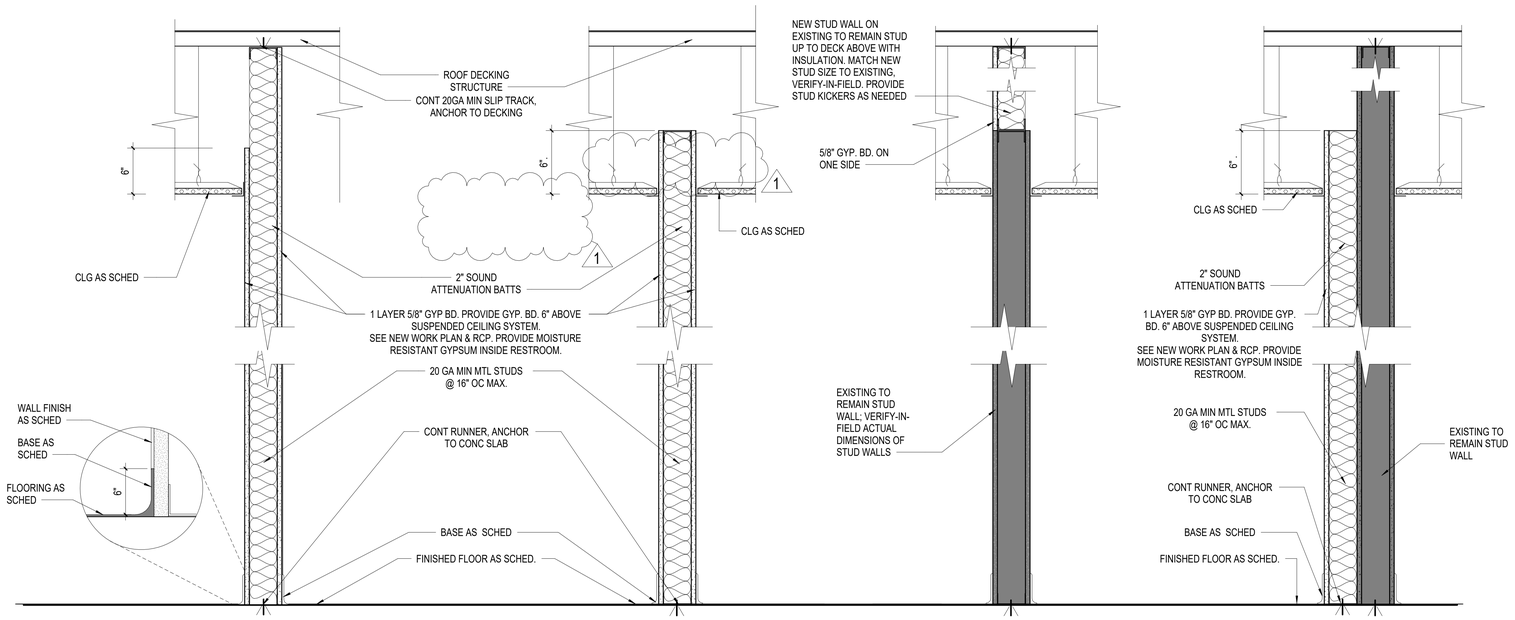

PARTITION TYPE "A" 6" STUD
PARTITION TYPE "C" 3-5/8" STUD

PARTITION TYPE "B" 3-5/8" STUD
PARTITION TYPE "D" 8" STUD

PARTITION TYPE "E"
EXISTING PARTITION
UP TO DECK

PARTITION TYPE "F"
EXISTING PARTITION W/
NEW 3-5/8" STUD

1 / A3.1 PARTITION TYPES
1 1/2" = 1'-0"

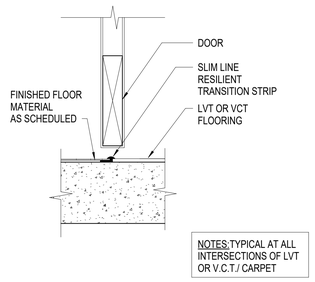

2 / A3.1 THRESHOLD DETAIL
3" = 1'-0"

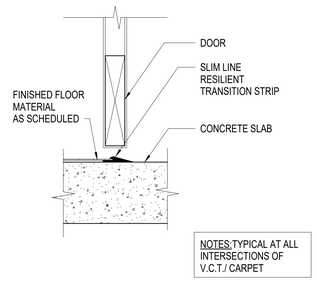

3 / A3.1 THRESHOLD DETAIL
3" = 1'-0"

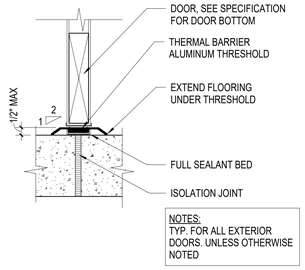

4 / A3.1 THRESHOLD DETAIL
3" = 1'-0"

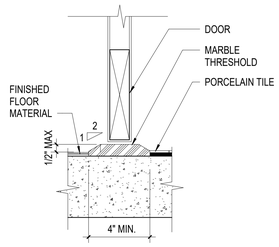

5 / A3.1 THRESHOLD DETAIL
3" = 1'-0"

SAMAHA

10521 Rosehaven Street, Suite 200 Fairfax, VA 22030
Phone 703-691-3311

LOUDOUN COUNTY PRCS

750 MILLER DR
LEESBURG, VA 20175

BID SET

LOUDOUN COUNTY

NO	REVISION	DATE
1	ADDENDUM	08/23/24

Sheet Title:
PARTITION TYPES

Issue Date: 7/24/24
Sheet Number:
A3.1

Sheet No. in Set: 6 Total No. Sheets: -

Project Number: XXXXXX
Drawn By: Author
Checked By: Checker