GENERAL NOTES:

1. COMPACTION REQUIRED ON ALL BACKFILLED AREAS.
2. COMPACTION CERTIFICATION REQUIRED AT FINAL INSPECTION.
3. 6" SLOPE IN THE FIRST 10' & 2% THEREAFTER.
4. ROOF VENTING THE REQUIRED AS PER IRC STANDARDS.
5. ALL STUCCO MUST BE ICC APPROVED.
6. ALUMINUM FLASHING REQUIRED BETWEEN ALL TRANSITIONS OF BRICK, STONE, STUCCO, SIDING, & CONCRETE.

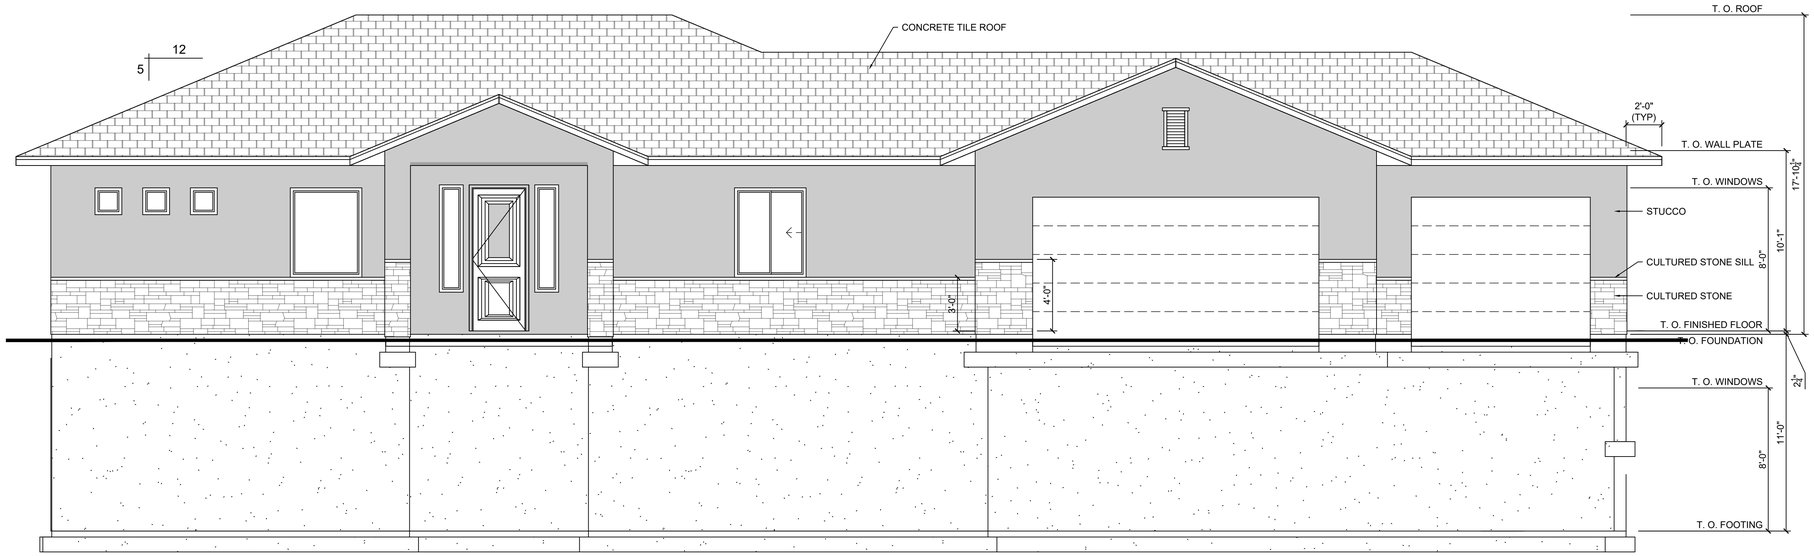

1 (NORTH) FRONT ELEVATION

SCALE: ¼" = 1'-0"

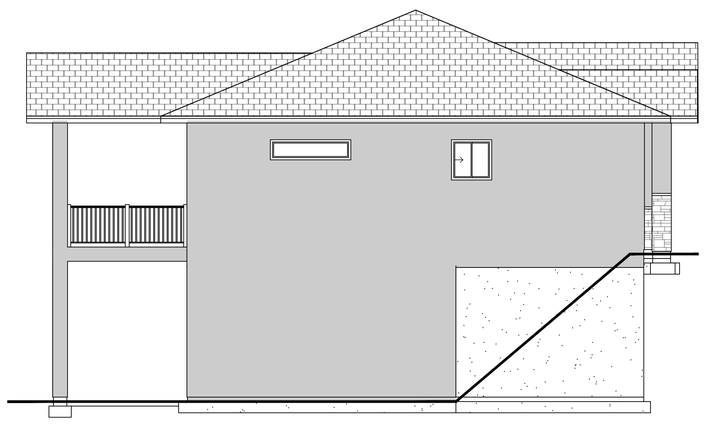

2 (EAST) LEFT ELEVATION

SCALE: 3/16" = 1'-0"

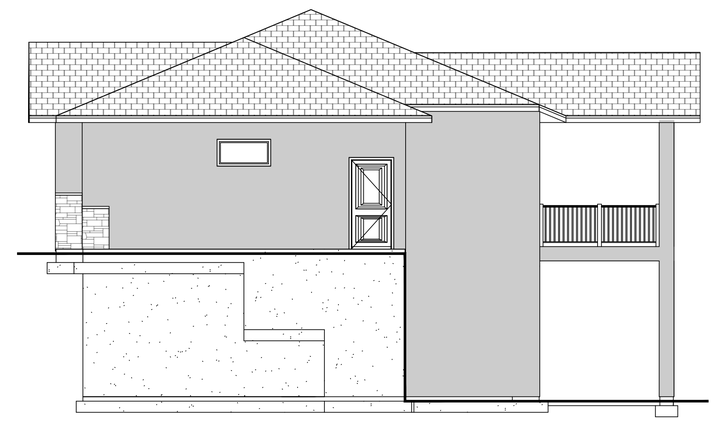

3 (WEST) RIGHT ELEVATION

SCALE: 3/16" = 1'-0"

4 (SOUTH) REAR ELEVATION

SCALE: 3/16" = 1'-0"

DRAWN BY	JLF
PROJECT #	20-142
REV.1	-
REV.2	-
FINAL REV.	1/11/2021

COOPER RESIDENCE
305 W. Shangri-La
Toquerville, UT 84774

ELEVATIONS

J. LONNIE FOX
DRAFTING AND DESIGN
phone (801) 787-1442 • jlonniefox@gmail.com • www.jlfdraftingdesign.com

BASEMENT SQFT	1713
MAIN FLR SQFT	1705
2ND FLR SQFT	0
GARAGE SQFT	909
TOTAL FIN SQFT	3418
TOTAL SQFT	3418

SHEET #
A2.1

COPYRIGHT 2020 J. LONNIE FOX DRAFTING AND DESIGN. THE PURCHASER IS GRANTED A SINGLE USE LICENSE FOR CONSTRUCTION ONLY. THESE PLANS ARE COPYRIGHTED AND ARE SUBJECT TO COPYRIGHT PROTECTION AS AN "ARCHITECTURAL WORK" UNDER THE COPYRIGHT ACT.