CODE SUMMARY

CODE DATA CHART:

Code Data Chart		1997 Standard Building Code		1994 ANSI/NFPA 101 Life Safety Code
Code Section	Section	Standard Building Code Notes:	Section	Life Safety Notes:
Occupancy Classification	Chapter 3	Group B – BUSINESS (Principal intended use) Group A-2 Small Assembly (Large class only)	26	New Business
Construction Type	606	Type IV Un-Protected Fully Sprinklered	NA	NA
Gross Building Area	Table 500	Maximum Area = 34,000 s.f. per floor 1st Floor ..... 14,915 G.S.F. 2nd Floor ..... 16,270 G.S.F. 3rd Floor ..... 16,270 G.S.F. Total ..... 47,455 G.S.F.	NA	NA
Building Height		Building Height = 42' Max Height 55'	NA	NA
Fire Resistance Rating	Table 600	Roof / Ceiling ..... NC Exterior Non-Bearing Walls And Cable Ends ..... NC, 10ft Unprotected Wall Opening Horiz. Separation over 10 Ft. ..NC Interior Non-Bearing Partitions..NC Columns ..... NC Beams ..... NC Floor / Ceiling ..... NC	26-1.6	No minimum construction requirements
Protection	Table 705.1.2 Table 704.2.4 Table 704.1	Elevator Shaft : Enclosure walls ..... 1 HR Noncombustible materials Opening Protectives ..... 1 HR Exit Access Corridor: Walls ..... 0 HR Opening Protectants ..... 0 HR Sprinklered Mechanical Shafts, Elevator Eqpt. Rooms: Walls ..... 1 HR Stairways: Walls ..... 1 HR Opening Protectants ..... 1 HR 100 sq. in. view panel glass Mixed Occupancy Separation btwn. business and assembly ..... 1 HR	26-3.6 5-2.6.2 5-1.3.2.1	Exit Corridors ..... 0 HR Hazardous Areas: Storage ..... 1 hr & sprinklers Opening Protectants .....3/4 HR Exits : Doors ..... 1 Hr. Walls ..... 1 Hr. Stairways : Walls ..... 1 HR
Materials and Finishes	708.2	Insulation: Flame Spread ..... 75 Max Smoke Rating ..... 450 Max Materials for fire resistance to comply with chapter requirements. Exits.....C Exit Access.....C Other Spaces .....F Flame Spread ..... FR – 200 Smoke Developed..... O – 450 Interior Sighns... 20% of Wall Area maximum	26-3.3-1	Interior Finish per 6-5: Test Standards per NFPA 255. Exit Corridors ..... Class A or B All other Spaces ..... Class A, B, or C Floors in Corridors..... Class I or II Class A..... Flame Spread ..... 0-25 Smoke Developed..... 0-450 Class B..... Flame Spread ..... 25-75 Smoke Developed..... 0-450 Class C..... Flame Spread ..... 70-200 Smoke Developed..... 0-450 Exception: Exposed structure complying with Type IV Construction per NFPA 220.
Fire Alarm System	905.1 905.1.5.4 905.1.5.5	Manual fire alarm system required. Exception: Fully Sprinkled Audible Alarms: 60 dBA minimum sound pressure. Visible Alarms: every occupied space	26-3.4.2 26-3.4.3	Alarm initiated by operation of sprinklers as Notification by live public address or per section 7-6.3
Stairs	1006.1 1007.3 1007.4 1007.4.3 1007.5	Exit stairways separated by 2 HR walls w/ 1-1/2 HR opening protectives per 705.1.2 Treads and risers shall be sum of two risers plus one tread equals between twenty-four and twenty-five inches. Landings shall have width not less than stairways. Landings to have guardrails on open side Handrails shall be located on each side, between 34" and 38" above tread. Exception: Handrails which form part of a guard-rail may be 42" high.	 5-2.2.2.1 5-2.2.4	 Max Riser..... 7 inches Max Treads ..... 11 inches Landing Width ..... stair width min. Handrails on both sides within 34" to 38" above tread. Exception: Handrails that form part of guardrail can be 42" high.

CODE DATA CHART:

Code Data Chart		1997 Standard Building Code		1994 ANSI/NFPA 101 Life Safety Code
Code Section	Section	Standard Building Code Notes:	Section	Life Safety Notes:
(Stairs Cont.)	1007.5.5	Extend 12" beyond top riser and at bottom extend one treed depth past bottom riser. Intermediate Rails inluded such that a 6-inch sphere can not pass through openings Headroom: minimum clearance 6'-8" a.f.f.	 5-2.2.4.6 5-1.5	Handrail: Extend 12" beyond to riser and slope to depth of one treed beyond bottom riser. Guardrails not yet less than 42" high with 4 inch sphere can not pass through intermediate rails. Headroom 6'-8" a.f.f. minimum
			5-2.2.6.3	Outside stairs separated by rated walls to 10 feet above top landing and 10 feet horizontally.
Sprinklers	903	Sprinkler system shall be provided for buildings without ample fire rescue access.	26-3.5	Provide portable fire extinguishers per Section 7-7.4.1
Sprinklers	1103 1103 Table 1104.3 1106.1 1106.2 1106.3 1012.1.2 1012.1.7 1012.2	Accessible route to connect accessible spaces with an interior path of travel between accessible route to floor levels. 50% of building entrances. Parking: For 26 to 50 stalls = 2 accessible stalls Toilet rooms must have minimum of one accessible fixture. All elevators. 50% of drinking fountains. Egress swinging door maximum force of 15 lbf to release latch, 30 lbf to set in motion. Exit doors shall open without use of key or special knowledge. Power operated doors shall be manually operable in event of power failure.	5-1.2 5-2.1.4 5-2.1.5 5-2.1.9	Accessible means of egress required to all public ways or areas of refuge. Force to open door in means of egress not to exceed 15 lbf to release latch, 30 lbf to set in action. Locks shall not require the use of key or special knowledge. Power operated doors shall be manually operable in event of power failure.
Exiting Provisions	Table 1003.1 Table 1004	Occupancy Load : Business ..... 100 Gross S.F./Person Assembly ..... 1 Fixed seat/person Egress Width : Corridors & Doors: ..... 0.20 Stairs ..... 0.30 Min. clear opening doors ..... 32" min. Min. corridor width ..... 44" min. Exception: 36 inches if load is less than 50 for corridors and stairs with projections and handrails 3-1/2 inches or less. Max. travel distance to exit ..... 250 feet Max Dead-end corridor ..... 20 feet	26-1.7 5-2.2.2	Business.....100 Gross S.F./Person Egress Width: Corridors & Doors.....0.20 Stairs.....0.30 Min. clear opening doors.....32" min. Min. corridor width.....44" min. Exception: 36 inches if load is less than 50 for corridors and stairs with projections and handrails 3-1/2 inches or less.
			26-2.5	Travel distance.....200 FT Max
			26-2.4	Max Common path of travel distance: 100 FT Max Dead-end corridor: 20 FT
	1004.2	Minimum Number of Exits: Occupancy Load 1-500 ..... 2 exits	2-8	Number of exits: Building shall have at least 2 exits located remotely per section 5-5.
	1004.1.2	Room with 50 or more occupants require 2 egress doors if travel distance exceeds 75 ft.	26-2.2.10	Area of refuge: Not required when Fully Sprinklered building.
	1003.3.2	Capacity of exit stairways shall be determined by the floor having the highest occupancy load, not the total building occupant load	5.5.4.4	Elevator as means of egress if accessed from an accessible area of refuge. Since building is fully sprinklered, elevator does not need to be located in a shaft system.
	1003.3.4	Required capacity of corridors serving exits at least equal to exit width required.		
	1004.3.2.1	Exit stair to be accessible must be 48" clear between handrails with on area of refuge. Exception: Fully Sprinklered Building.		
	1004.3.5	Areas of refuge not required to egress, due exception 1004.3.2.1 Fully Sprinklered.		
	1004.3.3	One elevator shall serve as one required accessible means of egress. Exception: Fully sprinklered buildings and floors provided with a horizontal exit and located at or above the level of the exit discharge.		

FIRE RESISTANCE DIRECTORY (EXRH)

FIRE RESISTANCE RATINGS - ANSI/UL263 (BXUV)—Continued

Design No. N501
Restrained Beam Rating—2 Hr.
Unrestrained Beam Rating—2 Hr.

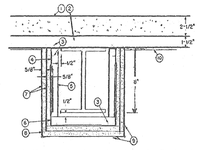

Steel Beam—Min size, a W8X24 with outside dimensions of 7-7/8x6-1/2 in. with a flange thickness of 3/8 in., a web thickness of 1/4 in., and a minimum weight of 24 lb/ft.
1. **Normal Weight Concrete**—148 pcf.
2. **Steel Floor and Form Units***—1-1/2 in. fluted type, welded to beam.
3. **Drill Screw**—No.8-18 by 1/2-in. long Phillips pankhead drill screws, self-drilling and self-tapping, made of case-hardened steel.
4. **Runner Angle**—24 MSG galv steel with 1 and 2-in. legs. Fastened to steel deck 12 in. O.C. with Item 3.
5. **Hanger**—Hat channel formed from 25 MSG galv steel, 1-11/16 in. deep with 1-in. legs and spaced 24 in. O.C. fastened to the runner angles with Item 3.
6. **Corner Angle**—Same material as Item 4, fastened to channel brackets with Item 3.
7. **Wallboard, Gypsum***—5/8 in. thick. First layer fastened with 1-1/4 in. long, 0.150 in. diam screws spaced 16 in. O.C. Second layer attached with Item 3 in. long, 0.120 in. diam screws spaced 16 in. O.C. Screws are self-drilling and self-tapping Phillips head made of case-hardened steel.
   American Gypsum Co.—Type AG-C.
   Canadian Gypsum Company—Type C, IP-X1, IP-X2, SCX, SHX or WRX.
   Celotex Corp.—Type C, FRP or SF1.
   Continental Gypsum Company—Type CG1-1, CG-1, CG1-3, CG5-5, CG6-6, CG9-9, CG3C-C, CG-C.
   G-P Gypsum Corp.—Types S, C, DGG, GYPS1, GYPS6.
   Jones Handle Gypsum Inc.—Types Fire X, Max"C".
   LaFarge Gypsum, A Div. of LaFarge Corp.—Types LGFC1, LGFC6, LGFC.
   National Gypsum Co., Charlotte, NC—Type FSR-G, FSW or FSW-G.
   National Gypsum Co., Riyadh, Saudi Arabia—Type FR or WR.
   Rulon Gypsum, A Div. of Pacific Coast Bldg. Products, Inc.—Type C, PN-1 or PN-C.
   Republic Gypsum Co.—Type RG-1, RG-3 or RG-C.
   Standard Gypsum Corp.—Type SG-C, SGC or SGC-C.
   Temple-Inland Forest Products Corp.—Type TG-C.
   United States Gypsum Co.—Types C, IP-X1, IP-X2, SCX, SHX, WRX.
   Yeso Panamericano SA de CV—Types C, IP-X1, IP-X2, SCX, SHX, WRX.
8. **Corner Bead**—Fabricated from 20 MSG galv steel to form an angle with 1-1/4 in. legs. Legs perforated with 1/4 in. diam holes approx 2 in. OC. Attached to wallboard with special crimping tool approx 6 in. OC. As an alternate, the bead may be nailed to the wallboard.
9. **Joint Treatment**—Cover the joints between edges of wallboard from corner beads and fastened out. Paper tape embedded in joint compound over joints with edges of compound feathered-out.
10. **Protective Material—Spray-Applied Fire Resistive Materials*** —Spray applied to the underside of the steel floor units, filling the flutes of the units and providing a smooth ceiling which was 1/4 in. thick as measured from the bottom plane of the floor units.
    Spray-Applied Fire Resistive Materials (CHPX) category for Individual Manufacturers
11. **Alternate Joint System**—(Not Shown)—For lath only. A 1/16 in. thickness of gypsum plaster applied to entire exposed surface over either paper tape on joints embedded in cementitious compound or 2 1/2 in. wide glass fiber tape stapled 8 in. O.C. on joints.

*Bearing the UL Classification Marking

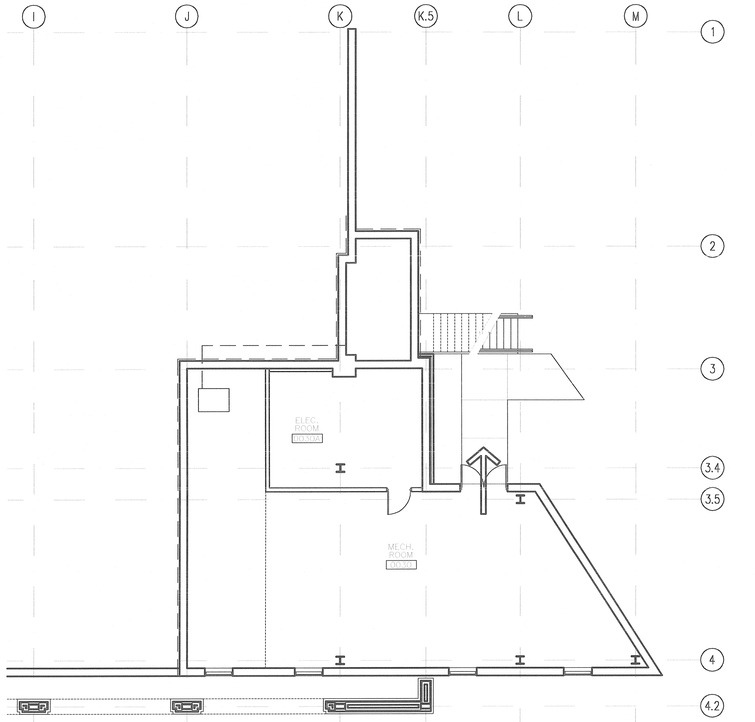

2 MECHANICAL LEVEL EGRESS PLAN
1/8" = 1'-0"

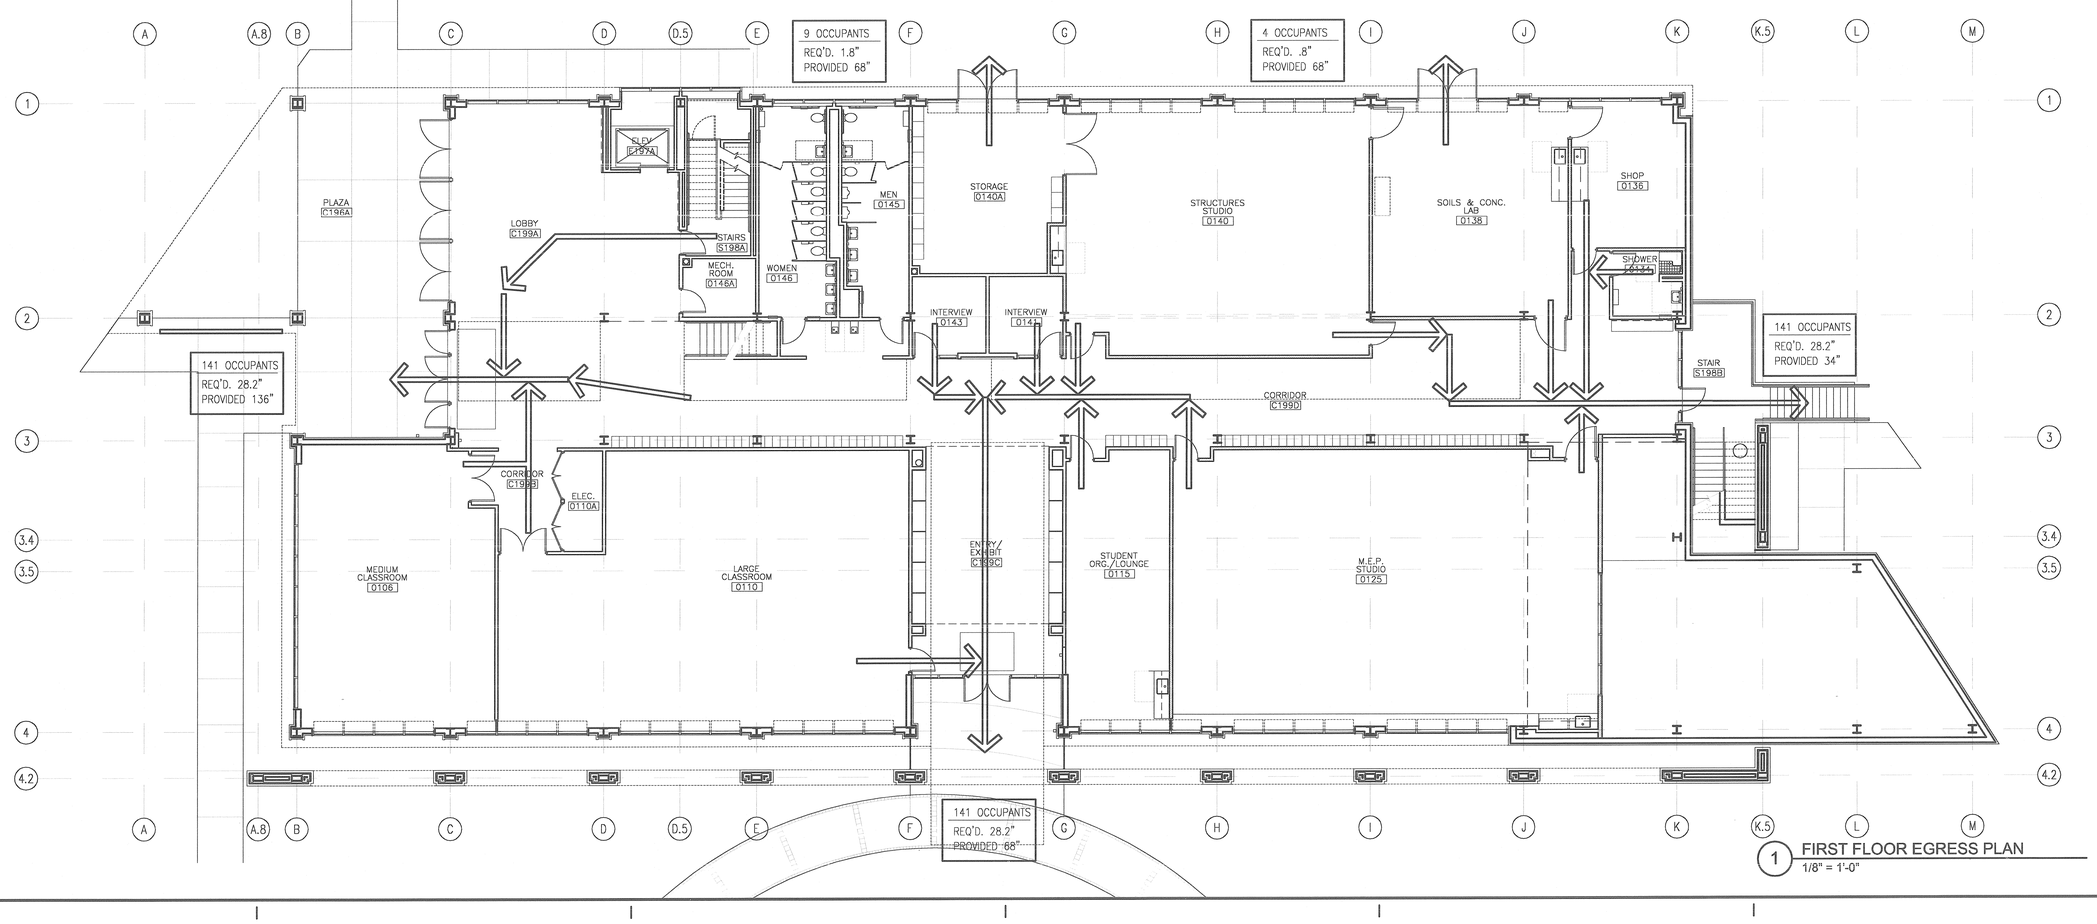

1 FIRST FLOOR EGRESS PLAN
1/8" = 1'-0"

M.E. RINKER, Sr. HALL
SCHOOL OF BUILDING CONSTRUCTION
UNIVERSITY OF FLORIDA-GAINESVILLE
PROJECT NO. BR-191

ARCHITECTS
CROXTON COLLABORATIVE/
GOULD EVANS ASSOCIATES

CROXTON COLLABORATIVE ARCHITECTS
475 FIFTH AVENUE
NEW YORK, NY 10017
TEL 212.683.1998
FAX 212.683.2799

GOULD EVANS ASSOCIATES
5405 WEST CYPRESS STREET
TAMPA, FL 33607
TEL 813.288.0729
FAX 813.288.0231

MECHANICAL ENGINEERS
LEHR ASSOCIATES
130 WEST 30TH STREET
NEW YORK, NY 10001-4092
TEL 212.947.8050
FAX 212.967.2059

STRUCTURAL ENGINEERS
WALTER P. MOORE
201 EAST KENNEDY BOULEVARD
TAMPA, FL 33602
TEL 813.221.2424
FAX 813.221.2289

CIVIL ENGINEERS
BROWN & CULLEN, INC.
3530 NW 43 STREET
GAINESVILLE, FL 32605
TEL 352.375.8999
FAX 352.375.0833

LANDSCAPE ENGINEERS
McCLAIN DESIGN GROUP, INC.
1843 NW 39 DRIVE
GAINESVILLE, FL 32605
TEL 352.372.2808
FAX 352.372.6622

CONSULTANT
SEEGY-BISCH
AUSSERE SULZBACHER STR. 118
NURNBERG, GERMANY
TEL 0911/59 90 99
FAX 0911/59 98 05

THIS DRAWING, AS AN INSTRUMENT OF SERVICE, IS AND SHALL REMAIN, PROPERTY OF CROXTON COLLABORATIVE ARCHITECTS. THIS DRAWING SHALL NOT BE REPRODUCED, PUBLISHED, USED ON OTHER PROJECTS, USED FOR ADDITIONS, OR USED IN COMPLETION OF THIS PROJECT BY OTHERS EXCEPT BY AGREEMENT IN WRITING. © 2001 CROXTON COLLABORATIVE ARCHITECTS/ GOULD EVANS ASSOCIATES.

NO.	ISSUE/REVISION	DATE

100% CONSTRUCTION DOCUMENTS

DRAWING NAME
MECHANICAL LEVEL & FIRST FLOOR PLAN EGRESS PLAN

DATE 11/21/01
SCALE 1/8"=1'-0"
DRAWN BY/CHECKED BY MM/JRae
DRAWING NUMBER A107