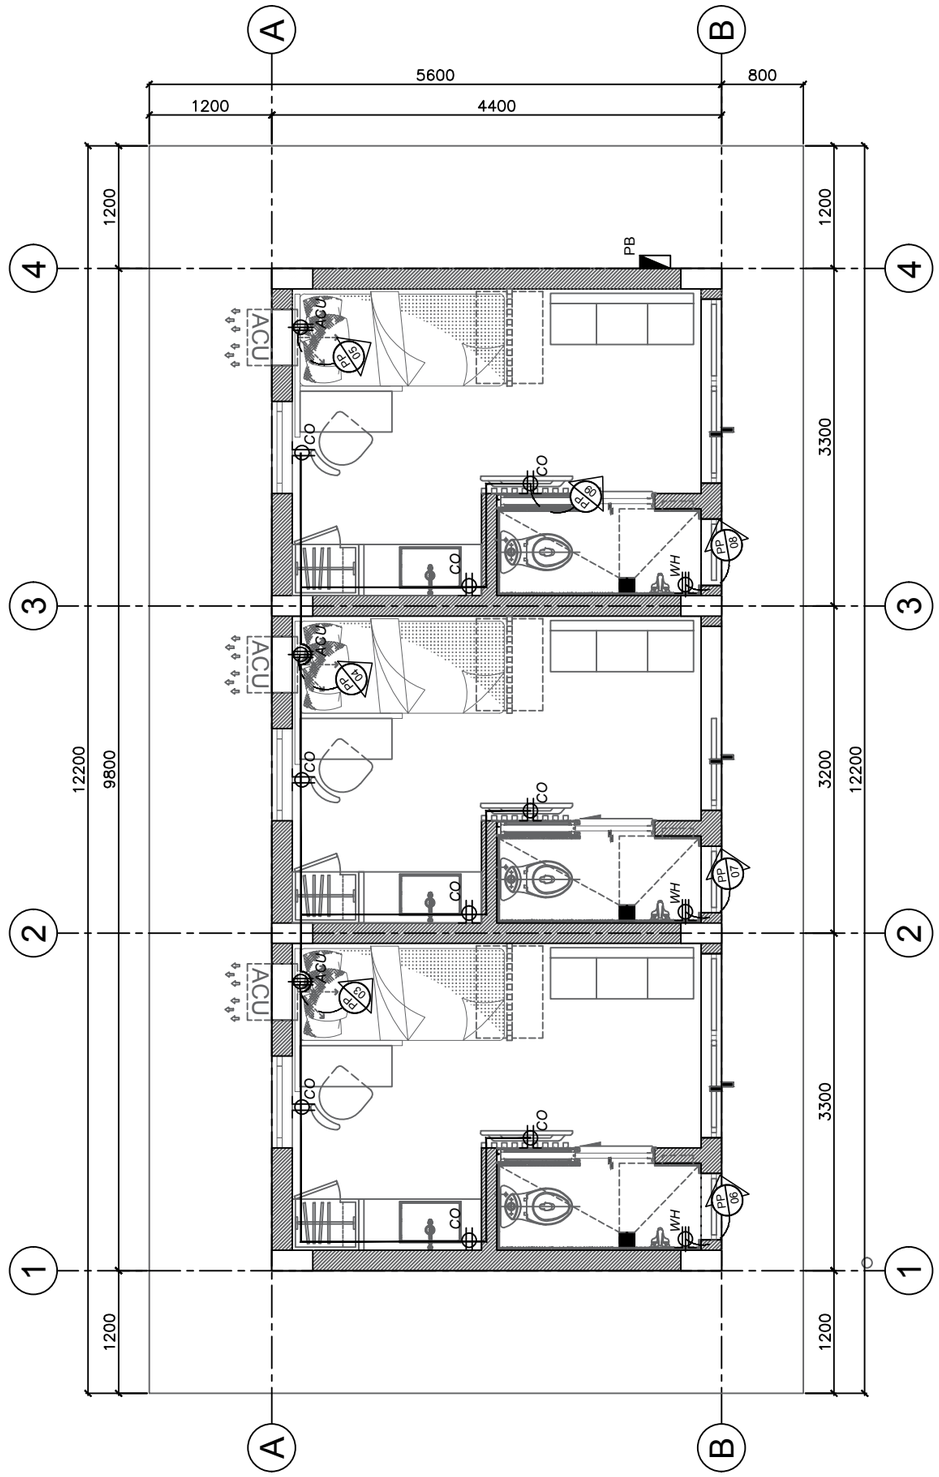

PROPOSED
POWER LAYOUT
1:60 MTS

1 / E-300 SCALE:

LEGEND:

POWER FIXTURES

- ACU (1 HP) WINDOW TYPE UNIT
- EXHAUST FAN (CEILING TYPE)
- MO — MISCELLANEOUS OUTLET FOR (MICROWAVE, TOASTER, RICE COOKER)
- ACU — CONVENIENCE OUTLET (AIRCON)
- WH — CONVENIENCE OUTLET (WATER HEATER)
- CO — DOUBLE CONVIENCE OUTLET
- Sa — SINGLE SWITCH SINGLE POLE
- Sbc — 2-GANG SWITCH SINGLE POLE
- Sdef — 3-GANG SWITCH SINGLE POLE
- LP — PANEL BOARD

REPUBLIC OF THE PHILIPPINES
DEPARTMENT OF SOCIAL WELFARE AND DEVELOPMENT
PRK. BUMANAAG, BRGY.ZONE III,
KORONADAL CITY, SOUTH COTABATO, FO XII

PREPARED BY:
ENGR. CRESSYL ANN E. BANTAYA
TECHNICAL FACILITATOR

CHECKED BY:
ENGR. FRANCIS C. ESTOMATA
PDO III

RA 9266 SECTION 33

Drawings and specifications and other contract documents duly signed, stamped or sealed, as instruments of service, are the intellectual property and documents of the architect, whether the object for which they are made is executed or not. It shall be unlawful for any person to duplicate or make copies of said documents for use in the repetition of and for other projects or buildings, whether executed partly or in whole, without the written consent of the architect or author of said documents.

REVIEWED AND VERIFIED BY:
ENGR. ROLLY A. TEOFILO
PDO IV FOR INFRA

PROJECT TITLE:
CONSTRUCTION OF 2-UNITS ISOLATION BUIDLING (11-ROOMS)

LOCATION:
RRCY, BRGY. BUKAY PAIT, TANTANGAN, SOUTH COTABATO

APPROVED BY:
CEZARIO JOEL C. ESPEJO
REGIONAL DIRECTOR
DSWD - FIELD OFFICE XII

SHEET CONTENT
POWER LAYOUT

REVISIONS

MARK	DATE

PROJECT NO.

DRAWN BY :	CEB
DESIGNED BY :	
DATE :	--
CHECKED BY :	FCE

SHEET NO.
E-300

SCALE: A3 AS SHOWN, A1