PRODUCED BY AN AUTODESK STUDENT VERSION

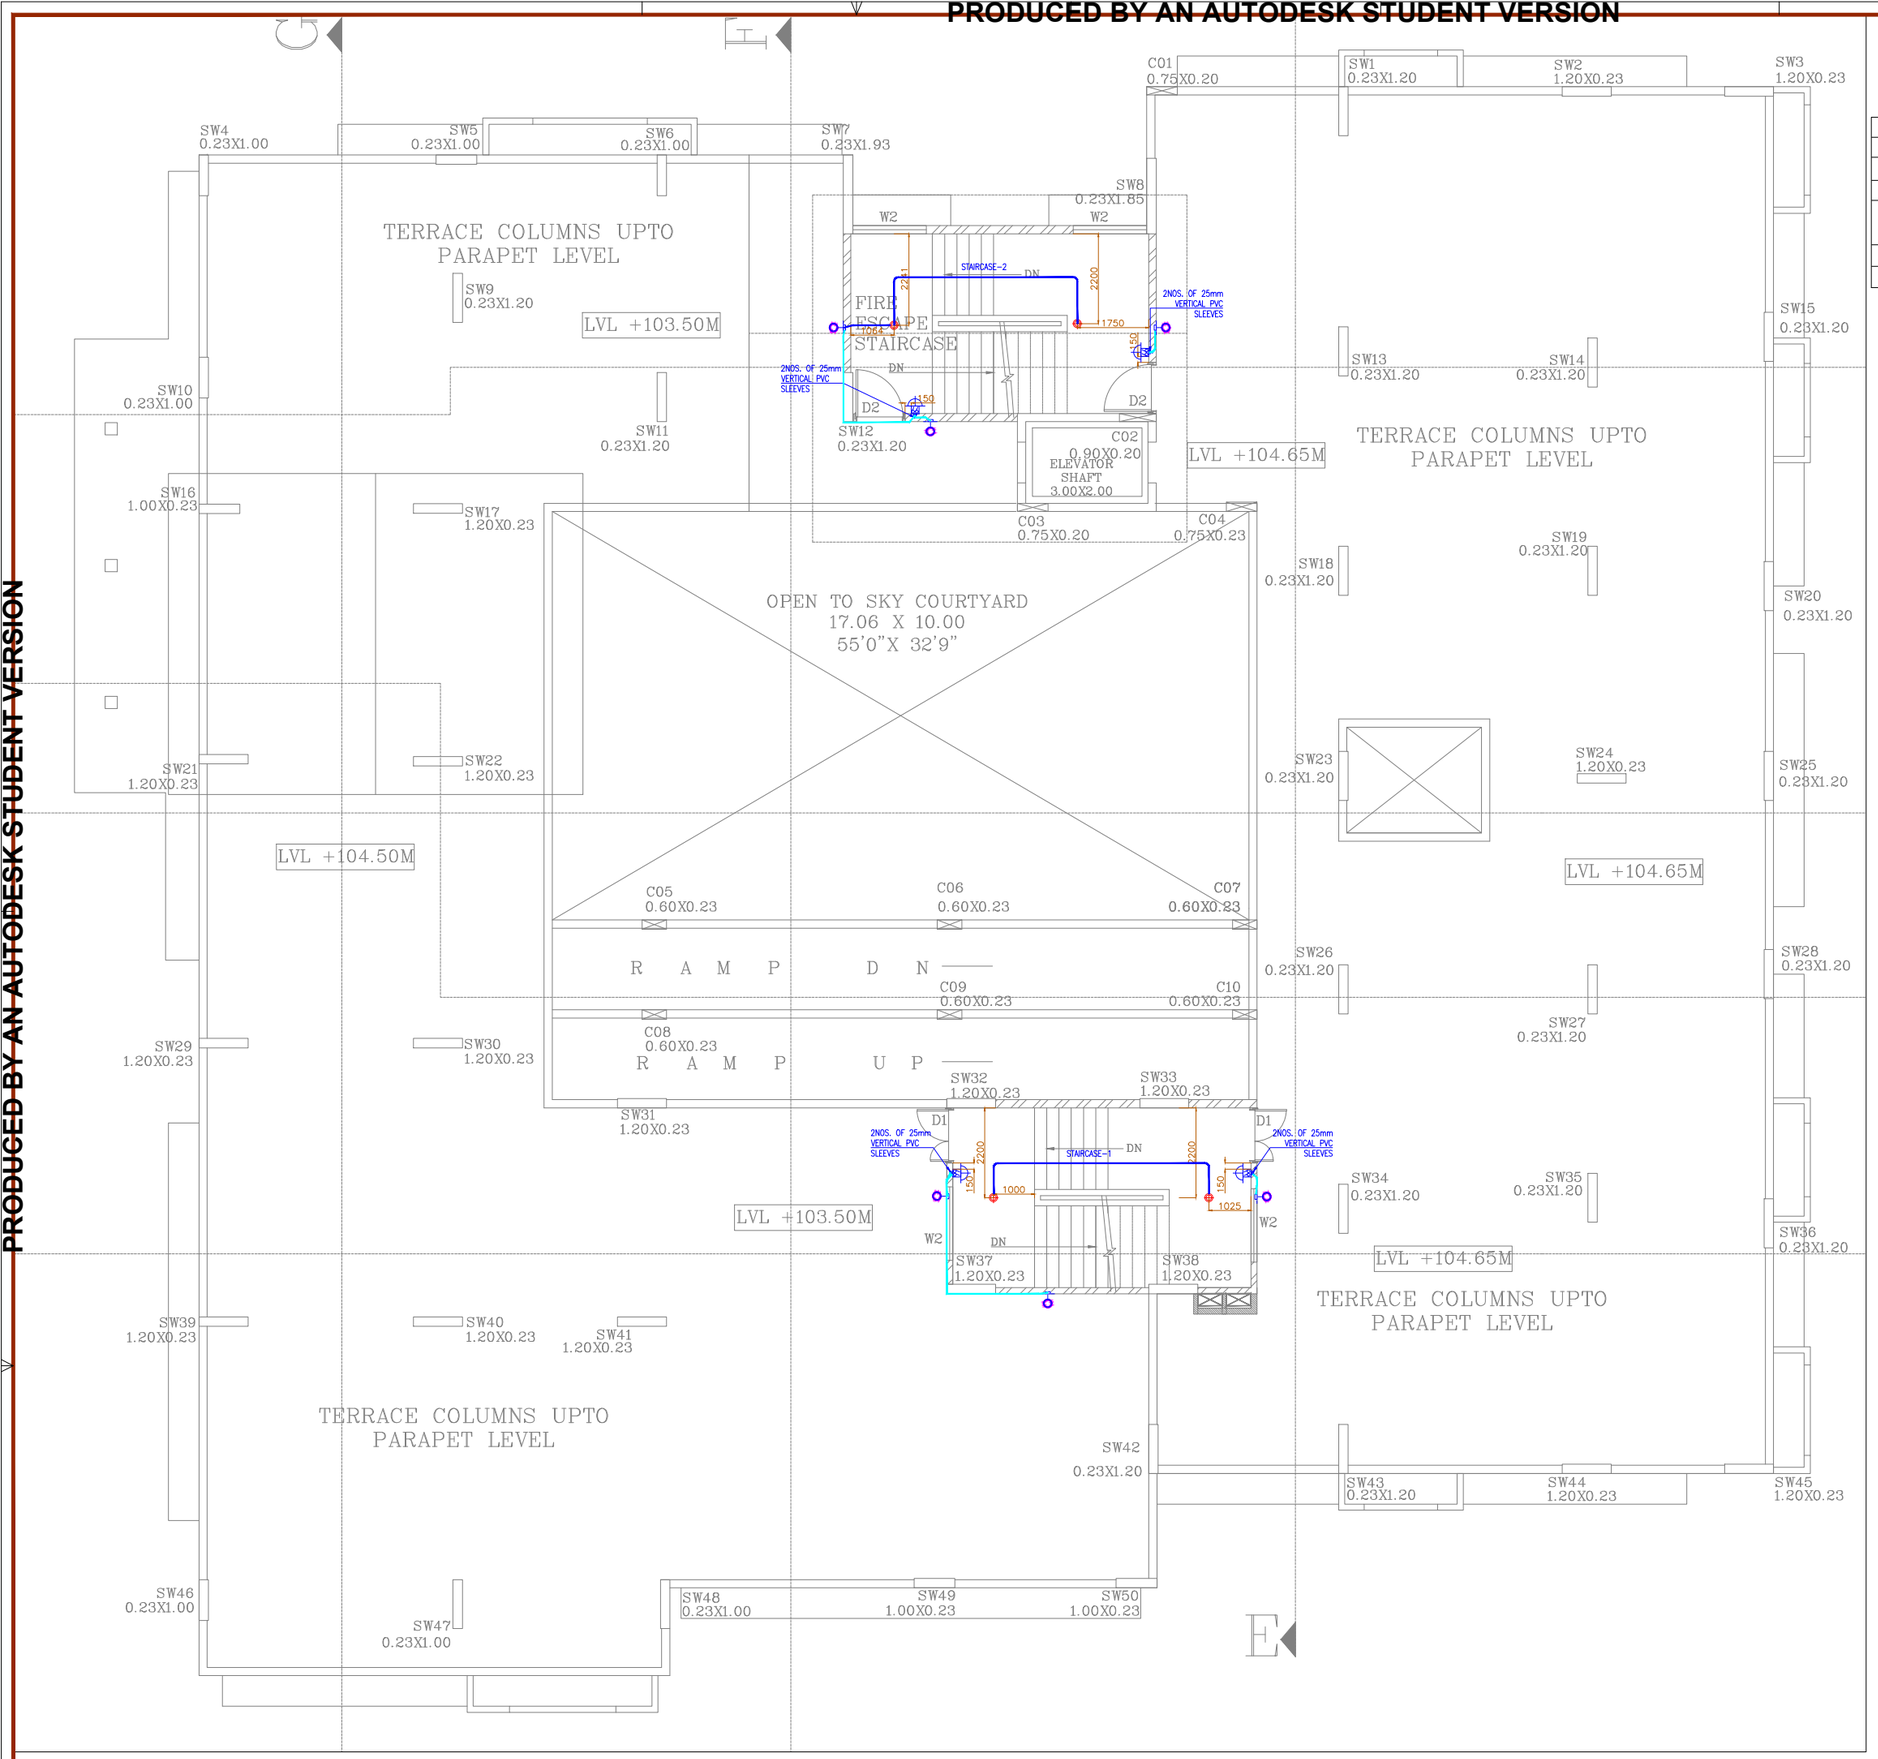

LEGEND:

	SWITCH BOARD WITH LIGHT SWITCH
	18W LED WALL MOUNTED IP65 BULKHEAD LUMINAIRE FOR TERRACE AREA.
	6A SOCKET WITH SWITCH.
	18W SURFACE MOUNTED LED DOWNLIGHTER ON EMERGENCY (REF WIPRO CAT NO.-CRDL11S023HP57)
	ø25 mm FRPVC SURFACE CONDUIT FOR POINT WIRING
	ø25 mm FRPVC CONDUIT FOR POINT WIRING

KEY PLAN

NOTE :

SUFFIX	DATE	REVISIONS
A	26/03/2021	FOR TENDER

DWG ISSUED FOR
☐ COMMENTS ☐ APPROVAL ☑ TENDER
☐ ADVANCE COPY ☐ RECORD ☐ G.F.C

ARCHITECT :
I N D E S I G N Architects And Interior Designers D-9, Saket Apartment, Patwardhan Baug, Karvenagar, Pune 411052
Tel : 020 - 25455830

ELECTRICAL CONSULTANTS:
abhiyanta
CONSULTING ENGINEERS LLP
Shree Swami Krupa, Plot No.-6, Neelkamal Housing Society, Karve nagar. Pune - 411052 . Tel/Fax.- 25462173, 25410691.
design@abhiyantaconsultants.com,
www.abhiyantaconsultants.com

CLIENT:
ARC. AUTISM RESEARCH CENTER

PROJECT:
AUTISM RESEARCH CENTER.

TITLE:
ELECTRICAL LAYOUT OF TERRACE FLOOR.

SCALE : 1:75	DATE : 26/03/2021	DRAWN SHUBHAM
DWG.NO. 2021/EL/--	SUFFIX A	CHECKED AMRUTA
		APPROVED VIVEK

REF. DWG
ARCH DWG REF:

THIS DRAWING IS THE PROPERTY AND COPYRIGHT OF ABHIYANTA CONSULTING ENGINEERS. [illegible] WRITTEN CONSENT. DO NOT SCALE THE DRAWING.

PRODUCED BY AN AUTODESK STUDENT VERSION