PRODUCED BY AN AUTODESK STUDENT VERSION

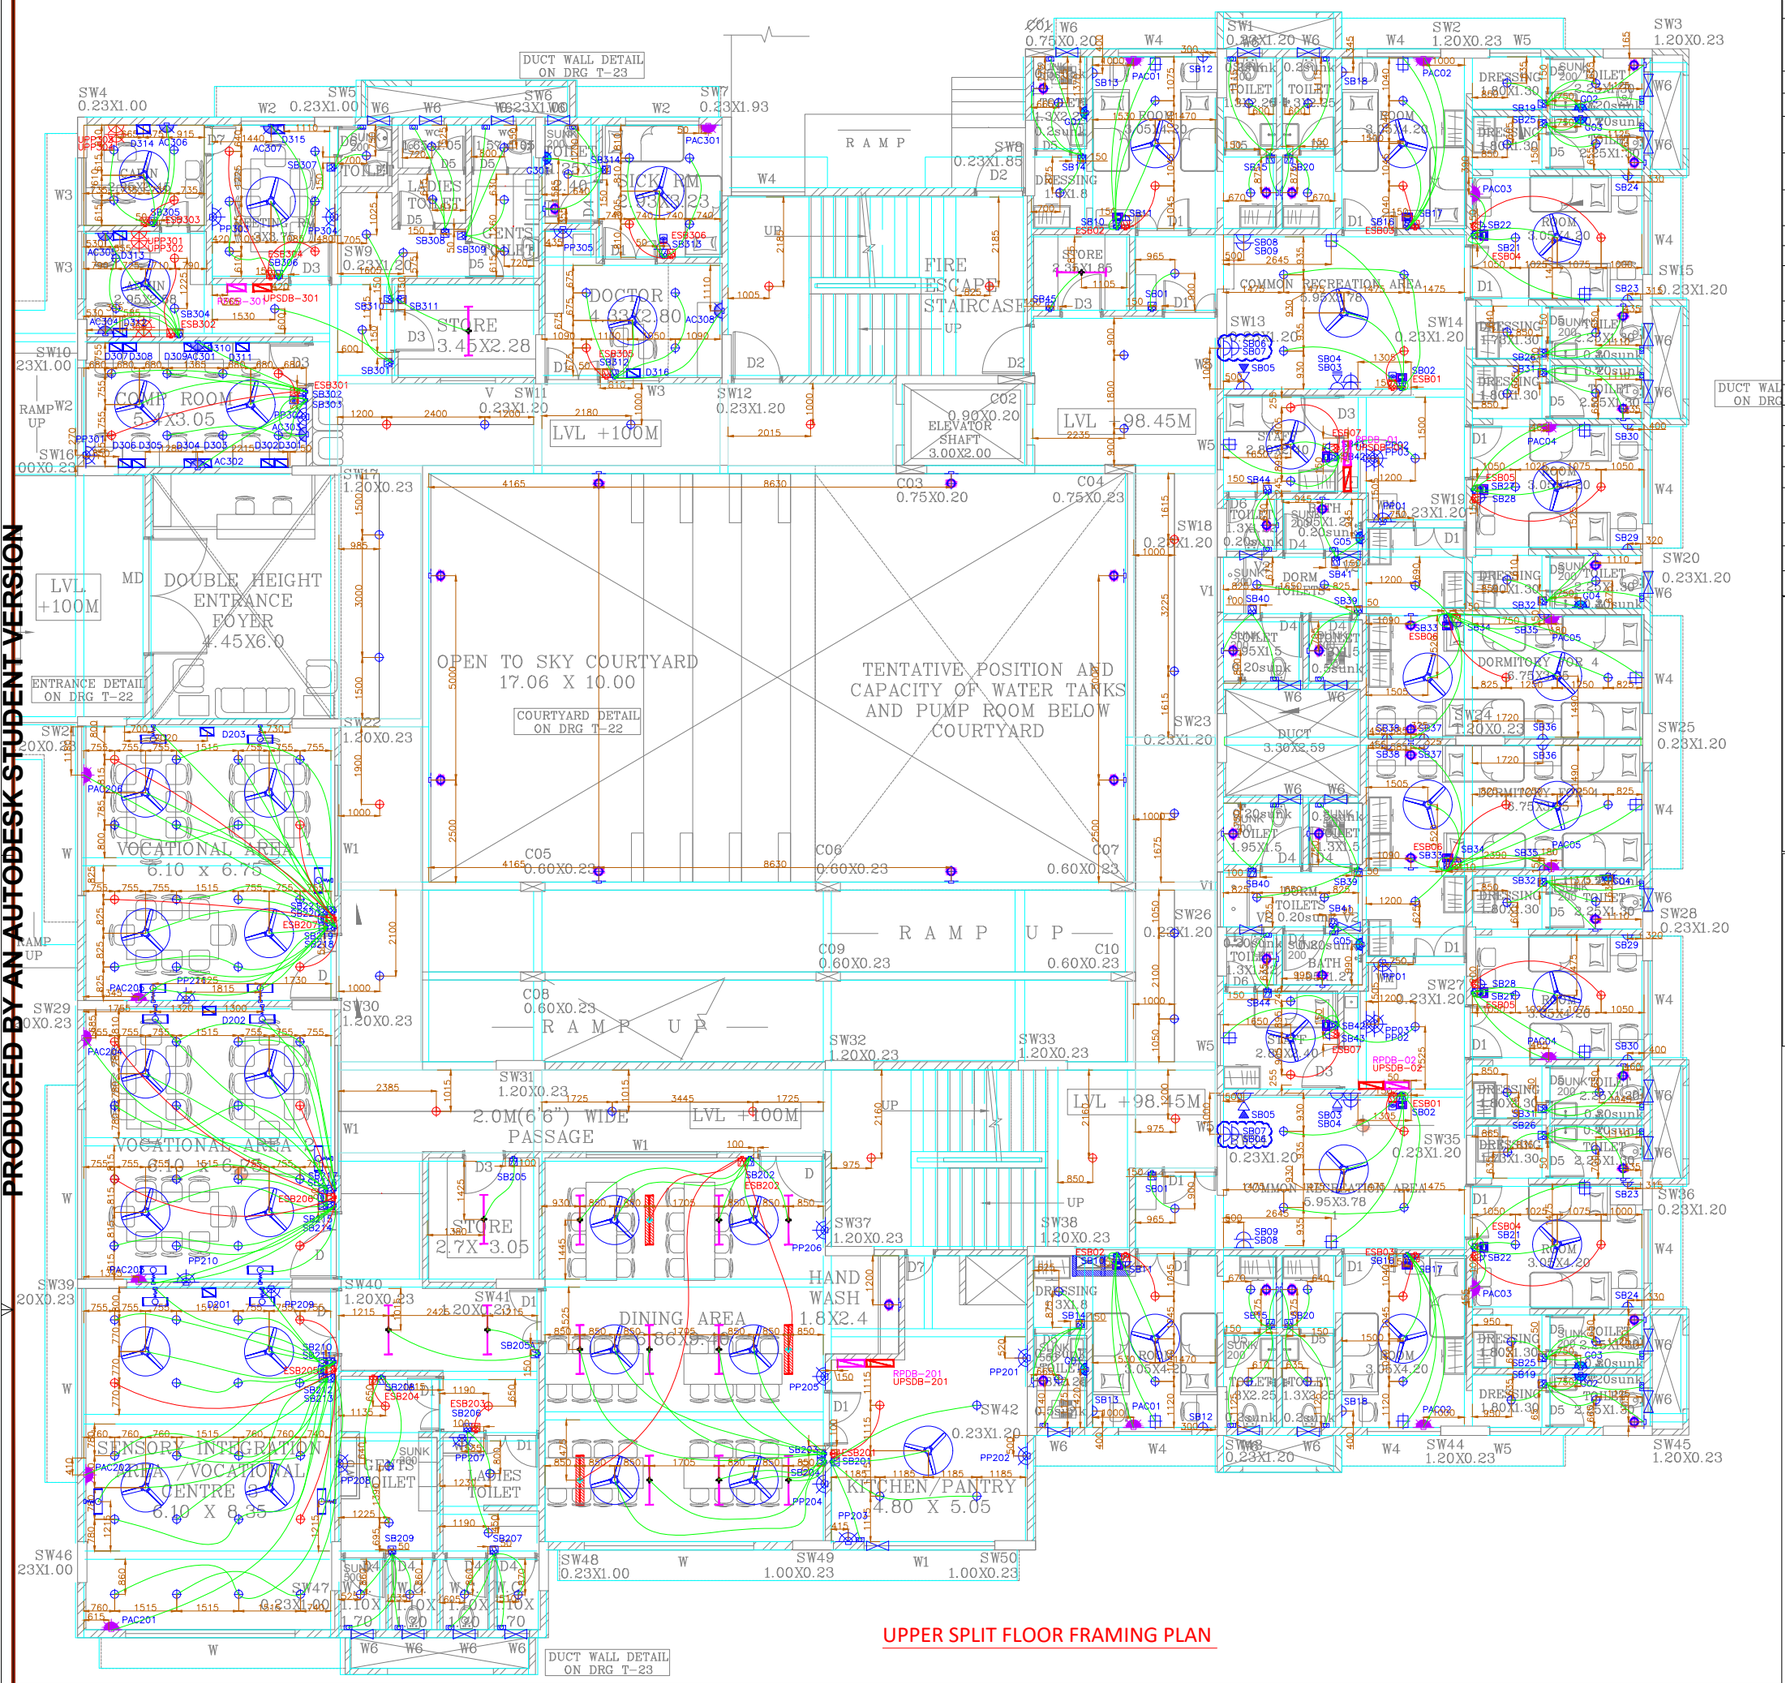

UPPER SPLIT FLOOR FRAMING PLAN

LEGEND:

	SWITCH BOARD WITH LIGHT SWITCH
	SWITCH BOARD WITH LIGHT SWITCH ON EMERGENCY
	1200MM CEILING FAN
	WALL LIGHT POINT @ 2500mm FROM FFL.
	DIFFUSED WALL LIGHT POINT
	18W SURFACE MOUNTED LED DOWNLIGHTER ON EMERGENCY (REF WIPRO CAT NO.-CRDL11S023HP57)
	12W SURFACE MOUNTED ROUND SLIM PANEL LED DOWNLIGHTER (WIPRO:LDB0-101-XXX-60-SM)
	12W SURFACE MOUNTED ROUND SLIM PANEL LED DOWNLIGHTER ON UPS (WIPRO:LDB0-101-XXX-60-SM)
	6A SOCKET ONLY
	6A SOCKET WITH SWITCH.
	20A 1ø SOCKET ONLY FOR GEYSER & SWITCH WITH INDICATOR WILL PROVIDED ON ITS RESPECTIVE SWITCH BOARD.
	LED FOOT LIGHT @300mm FROM FFL.
	EXHAUST FAN
	PANIC ALARM
	SINGLE TELEPHONE SOCKET OUTLET
	ELECTRICAL DB @ 1500mm FROM FFL
	CEILING ROSE
	SINGLE DATA SOCKET OUTLET FOR WIFI @2250mm FROM FFL.
	6A/16A SWITCH & SOCKET
	T.V. ANTENNA SOCKET OUTLET
	20A 1 PHASE SOCKET FOR AC PROVISION ONLY & SWITCH WILL BE ON ITS RESP. SWITCH BOARD AS PER SCHEDULE
	ø25 mm FRPVC CONDUIT FOR POINT WIRING
	ø25 mm FRPVC CONDUIT FOR SUBMAINS
	ø32 mm FRPVC CONDUIT FOR MAINS

HEIGHT SCHEDULE:

HEIGHTS MENTIONED IN FOLLOWING ITEMS ARE IN mm FROM FFL.
TO BOTTOM OF RESPECTIVE ITEM AND ARE AS FOLLOWS:

1. DISTRIBUTION BOARD = 1500mm
2. MAIN SWITCHBOARD = 1200mm
3. BED SIDE SWITCH BOARD = 600mm
4. AC = 2450mm OR 150mm ABOVE BEAM BOTTOM
5. GEYSER = 2300mm OR 150mm ABOVE BEAM BOTTOM
6. EXHAUSE FAN = NEAR TO EXHAUST FAN CUTOUT
7. FRIDGE = 1350mm
8. OVEN = 1000mm
9. WATER PURIFIER = 1400mm
10. AQUA = 1300mm
11. WASHING MACHINE = 1000mm
12. IRONING POWER POINT = 1000mm
13. DATA,TELEPHONE POINT = 600mm
14. MIXER = 1200mm
15. WALL LIGHT POINT = 2450mm
16. WASH BASIN LIGHT POINT = 1800mm
17. FOOT LIGHT = 300mm
18. TV POINT=
    - 2 NO. 6A SOCKET ONLY + 1 NO. 6A SWITCH + HDMI = 600mm
    - 1 NO. 6A SOCKET ONLY + TVAV + BLANK PLATE = 1050mm

NOTES:

1) EXACT SIZE OF PANEL WILL BE TAKEN AS PER GA DIAGRAM
2) ALL WALL LIGHT POINT SHALL BE AT 2500mm FROM FFL. IF ANY
3) ALL DIAMENSIONS WILL BE AS PER BEAM AND COLUMN REFERENCE.
4) TV, DATA POINT SHOWN IN THIS DRAWING IS FOR THE LOCATION IT IS TAKEN IN ELV DRAWINGS.
5) CONNECTION FOR EXHAUST TO BE PROVIDED (CONNECTOR ONLY) WHERE EXHAUST FAN HAS BEEN INDICATED
6) FOR DIMENTION OF ALL SWITCH BOARDS ARE EITHER FROM CENTER OF SWITCH BOARD OR FROM CORNER OF FINISHED PLATE OF SWITCH BOARD (FOR ALL TILED AREAS THE EDGES OF SWITCH PLATE SHOULD MATCH TO THE TILE JOINT)
7) TOILET AREA SWITCH BOARD TO BE ALIGNED WITH TILE JOINT.
8) ALL HEIGHTS MENTIONED ARE FROM FINISHED FLOOR LEVEL.
9) ALL HEIGHTS MENTIONED ARE FROM FFL TO PLATE BOTTOM OF SWITCH BOARD

KEY PLAN

NOTE :

SUFFIX	DATE	REVISIONS
R0	05/04/2021	GOOD FOR CONSTRUCTION

DWG ISSUED FOR
☐ COMMENTS ☐ APPROVAL ☐ TENDER
☐ ADVANCE COPY ☐ RECORD ☑ G.F.C

ARCHITECT :
I N D E S I G N Architects And Interior Designers D-9, Saket Apartment, Patwardhan Baug, Karvenagar, Pune 411052
Tel : 020 - 25455830

ELECTRICAL CONSULTANTS:
abhiyanta CONSULTING ENGINEERS LLP
Shree Swami Krupa, Plot No.-6, Neelkamal Housing Society, Karve nagar. Pune - 411052 . Tel/Fax.- 25462173, 25410691.
design@abhiyantaconsultants.com,
www.abhiyantaconsultants.com

CLIENT:
ARC. AUTISM RESEARCH CENTER

PROJECT:
AUTISM RESEARCH CENTER.

TITLE:
POINT LAYOUT OF LOWER SPLIT FLOOR PLAN.

SCALE : 1:75	DATE : 01/04/2021	DRAWN SHUBHAM L
DWG. NO. 2021/EL/----	SUFFIX R0	CHECKED AMRUTA
		APPROVED VIVEK

REF. DWG
ARCH DWG REF:

THIS DRAWING IS THE PROPERTY AND COPYRIGHT OF ABHIYANTA CONSULTING ENGINEERS LLP. IT MAY NOT BE REPRODUCED OR TRANSMITTED IN ANY FORM OR BY ANY MEANS WITHOUT WRITTEN CONSENT. DO NOT SCALE THE DRAWING.

PRODUCED BY AN AUTODESK STUDENT VERSION