SHEET NOTE	
1	REMOVE AND DEMOLISH DATA SWITCH.
2	REMOVE AND DEMOLISH DATA RACK AND ASSOCIATED CABLING.
3	REMOVE EXISTING FIBER OPTICS EQUIPMENT AND CABLING. COORDINATE REMOVAL WITH OWNER AND SERVICE PROVIDER TO NEW MAIN DATA ROOM.
4	REMOVE AND DEMOLISH LIGHTING FIXTURE.
5	CABINET 4 (VERIZON) AND CABINET 5 (BELL ATLANTIC) WALL MOUNTED STACKED ON WALL. REMOVE AND COORDINATE WITH OWNER AND SERVICE PROVIDER
6	CABINET 6 (BELL ATLANTIC). REMOVE AND COORDINATE WITH OWNER AND SERVICE PROVIDER.
7	CABINET 3 (VERIZON) AND CABINET 4 (VERIZON) WALL MOUNTED STACKED ON WALL. REMOVE AND COORDINATE WITH OWNER AND SERVICE PROVIDER
8	REMOVE AND DEMOLISH QUAD RECEPTACLE ON CORD REEL.
9	EXISTING PANELBOARDS TO REMAIN.
10	EXISTING PANELBOARD TO REMAIN.
11	EXISTING INCOMING DATA CIRCUITS (COPPER AND FIBER) TO BE REMOVED. REMOVE AND COORDINATE WITH OWNER AND SERVICE PROVIDER.
12	NO WORK IN THIS SPACE.
13	SPLIT COOLING SYSTEM TO REMAIN.
14	LIGHTS IN THIS STAIR ARE EXISTING TO REMAIN.

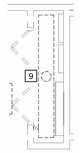

ELECTRICAL CLOSET ELECTRICAL DEMOLITION ENLARGED PLAN
5 E1.1 SCALE: 1/4" = 1'-0"

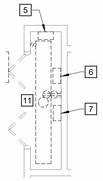

TELECOM CLOSET ELECTRICAL DEMOLITION ENLARGED PLAN
4 E1.1 SCALE: 1/4" = 1'-0"

TELECOM ROOM ELECTRICAL DEMOLITION ENLARGED PLAN
3 E1.1 SCALE: 1/4" = 1'-0"

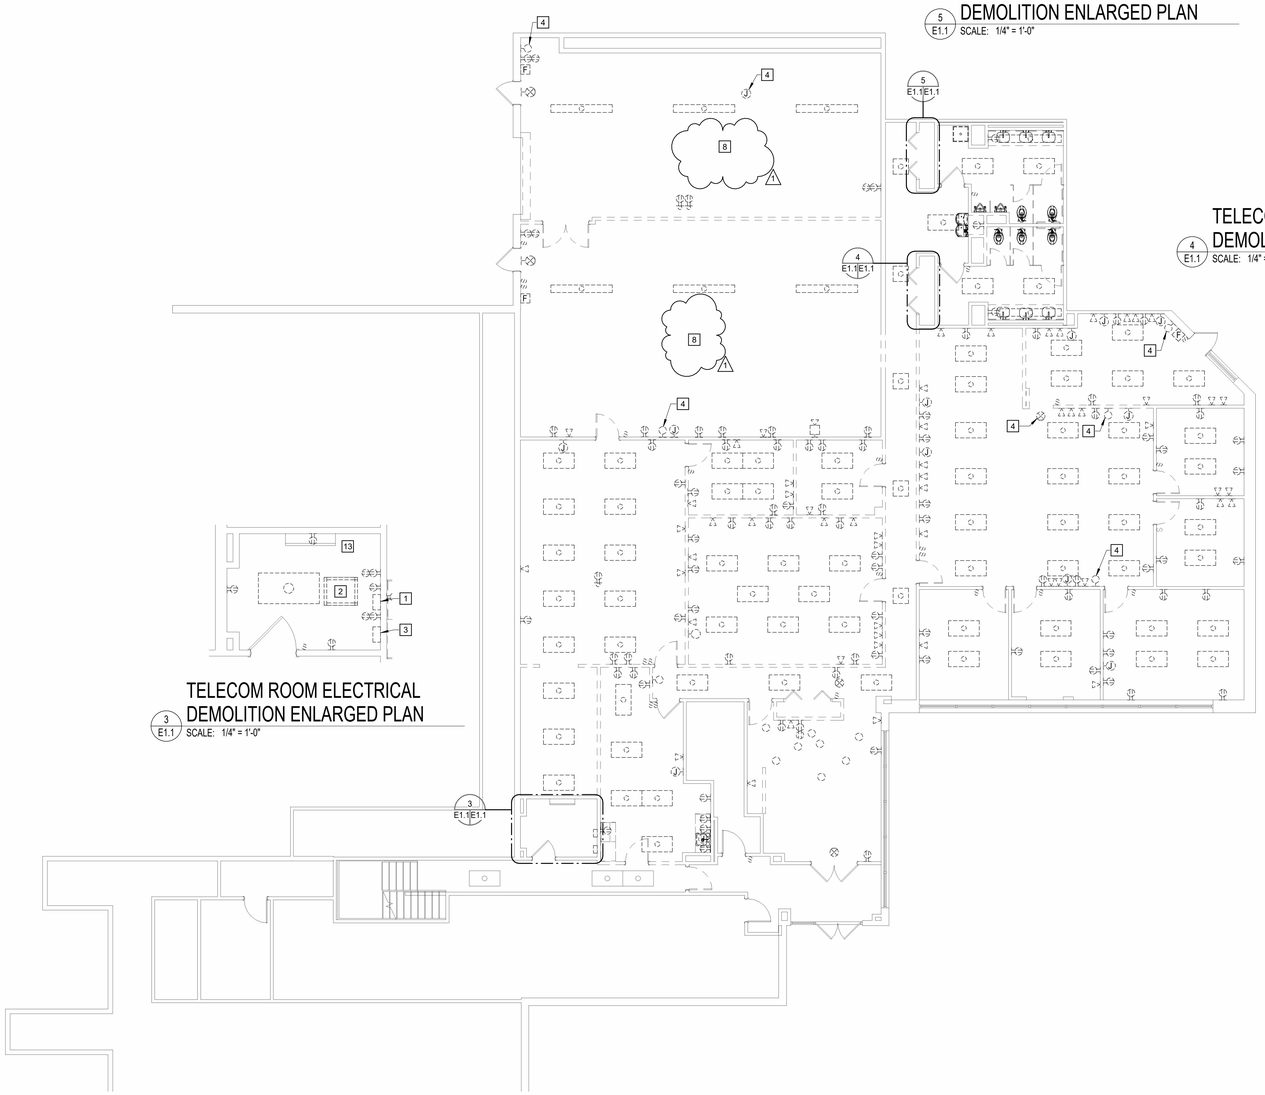

FIRST FLOOR ELECTRICAL DEMOLITION PLAN
1 E1.1 SCALE: 1/8" = 1'-0"

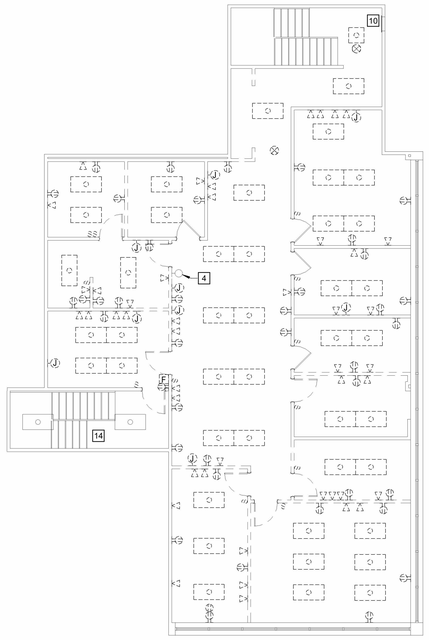

SECOND FLOOR ELECTRICAL DEMOLITION PLAN
2 E1.1 SCALE: 1/8" = 1'-0"

SAMAHA

10521 Rosehaven Street, Suite 200 Fairfax, VA 22030
Phone 703-691-3311 Fax 703-691-3316

ASCENT ENGINEERING GROUP
5228 VALLEYPOINTE PKWY, SUITE 4
ROANOKE, VIRGINIA 24019
(540) 265-4444

D: 2024-0030 C:

LOUDOUN COUNTY PRCS

750 MILLER DR
LEESBURG, VA 20175

BID SET

LOUDOUN COUNTY

NO	REVISION	DATE
1	Addendum 1	08/30/2024

Sheet Title:

ELECTRICAL DEMOLITION PLANS

Issue Date: 7/24/2024

Sheet Number:

E1.1

Sheet No. in Set: Total No. Sheets: -

Project Number: XXXXXX
Drawn By: Author
Checked By: Checker