ELECTRICAL LEGEND

- CEILING MOUNTED LIGHT
- RECESSED LIGHT
- WALL MOUNTED LIGHT
- PENDANT LIGHT
- CHANDELIER
- CEILING FAN
- CEILING FAN W/ LIGHT KIT
- FLORESCENT LIGHT BOX
- EXHAUST FAN
- MOTION SPOTLIGHT
- SD SMOKE DETECTOR
- CO CARBON MONOXIDE DETECTOR
- OUTLET
- FLOOR OUTLET
- 220 V OUTLET
- $ SWITCH
- TV CABLE TELEVISION OUTLET
- CAT 5
- AFCI ARC FAULT INTERRUPTER
- GFCI GROUND FAULT INTERRUPTER
- GFCI/WP WEATHERPROOF
- HB HOSE BIB
- GAS NATURAL GAS

ELECTRICAL:

1. SINGLE AND MULTIPLE STATION SMOKE DETECTORS SHALL BE INSTALLED IN THE FOLLOWING LOCATIONS AND BE CONNECTED TO ONE BEDROOM CIRCUIT WITH IRC R314-R315.
   - IN EACH BEDROOM
   - OUTSIDE OF EACH SEPARATE SLEEPING AREA IN THE IMMEDIATE VACINITY OF THE BEDROOMS
   - ON EACH ADDITIONAL STORY OF THE DWELLING, INCLUDING BASEMENTS AND CELLARS BUT
   - NOT CRAWL SPACES AND UNIHABITED ATTICS.
2. WIRE FOR DISHWASHER AND HOOD.
3. GFCI PROTECTION OF OUTLETS RQD. IN BATHROOMS AND GARAGES. (UP MIN. 18" OFF FLOOR) OUTDOORS INCLUDED.
4. HALLWAYS 10' OR MORE IN LENGTH SHALLHAVE A RECEPTACLE OUTLET.
5. SPACING FOR ELECTRICAL OUTLETS AT KITCHEN COUNTER, BAR, ISLAND IS 4' O.C. MAX.
6. PROVIDE INDIVIDUAL BRANCH CIRCUITS FOR FURNACE, REFRIGERATOR 7 (WHIRL POOL TO HAVE GFCI BREAKER #10 WIRE)
7. LIGHT IN CLOST SHALL CONFORM TO CLEARANCES SPECIFIED IN NEC 410-8
8. PROVIDE LIGHT IN ATTIC & CRAWL SPACE W/ SWITCH 7 ACCESS.
9. ALL TEMPORARY WIRING SHALL CONFORM TO NEC ARTICLE 305
10.PROVIDE #4 AWG OR LARGER BARE COPPER CONDUCTOR OR STEEL REINFORCING BAR OR ROD NOT LESS THAN 1/2 " DIA. GROUNDING ELECTRODES 20' MIN. LENGTH.
11. ARC FAULT PROTECTED CIRCUIT INTERUPTER IN ALL SLEEPING BEDROOMS AT BREAKER PANEL.

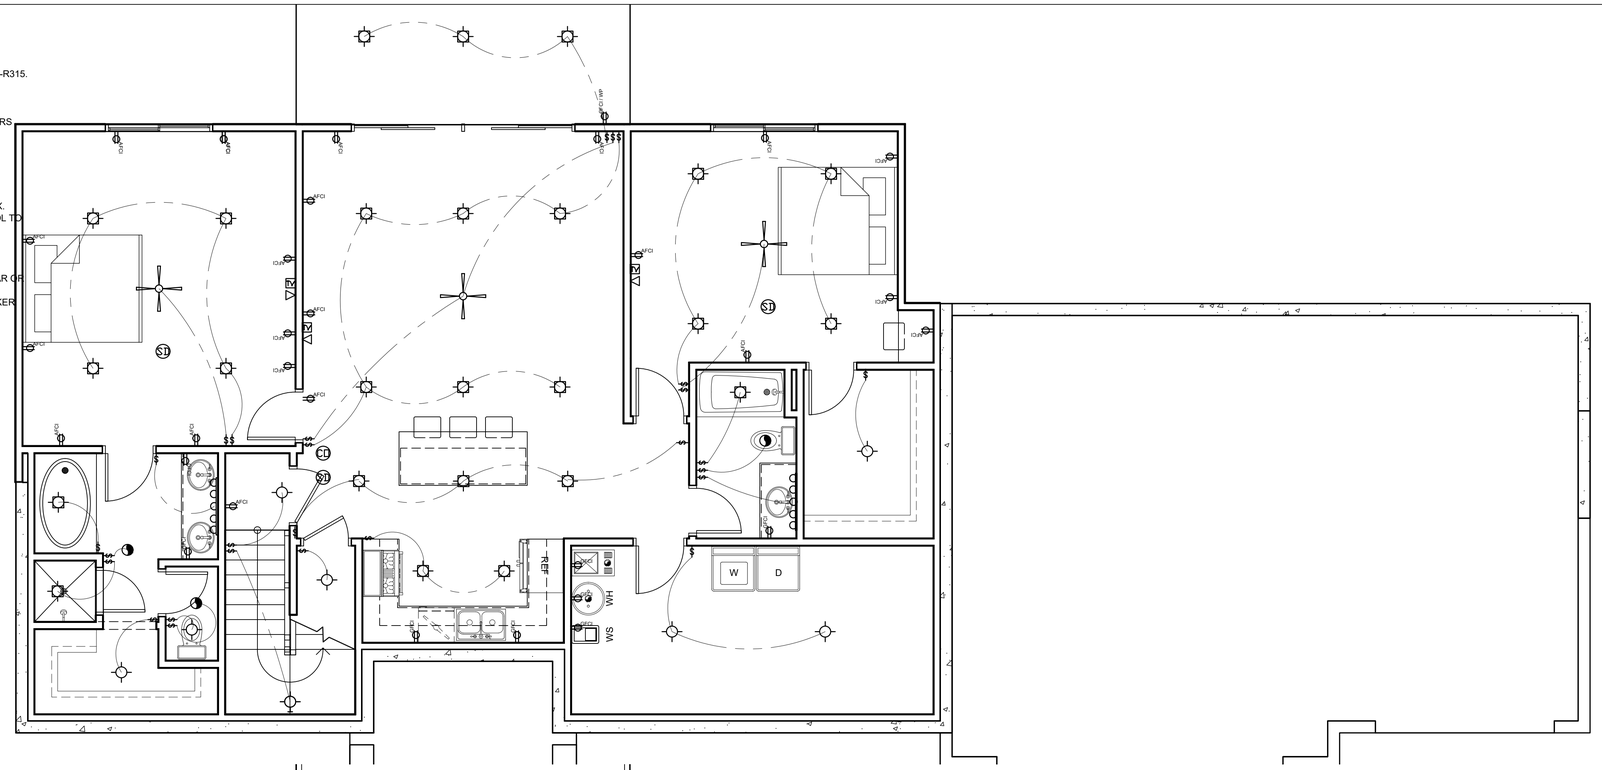

BASEMENT FLOOR ELECTRICAL PLAN

SCALE: ¼" = 1'-0"

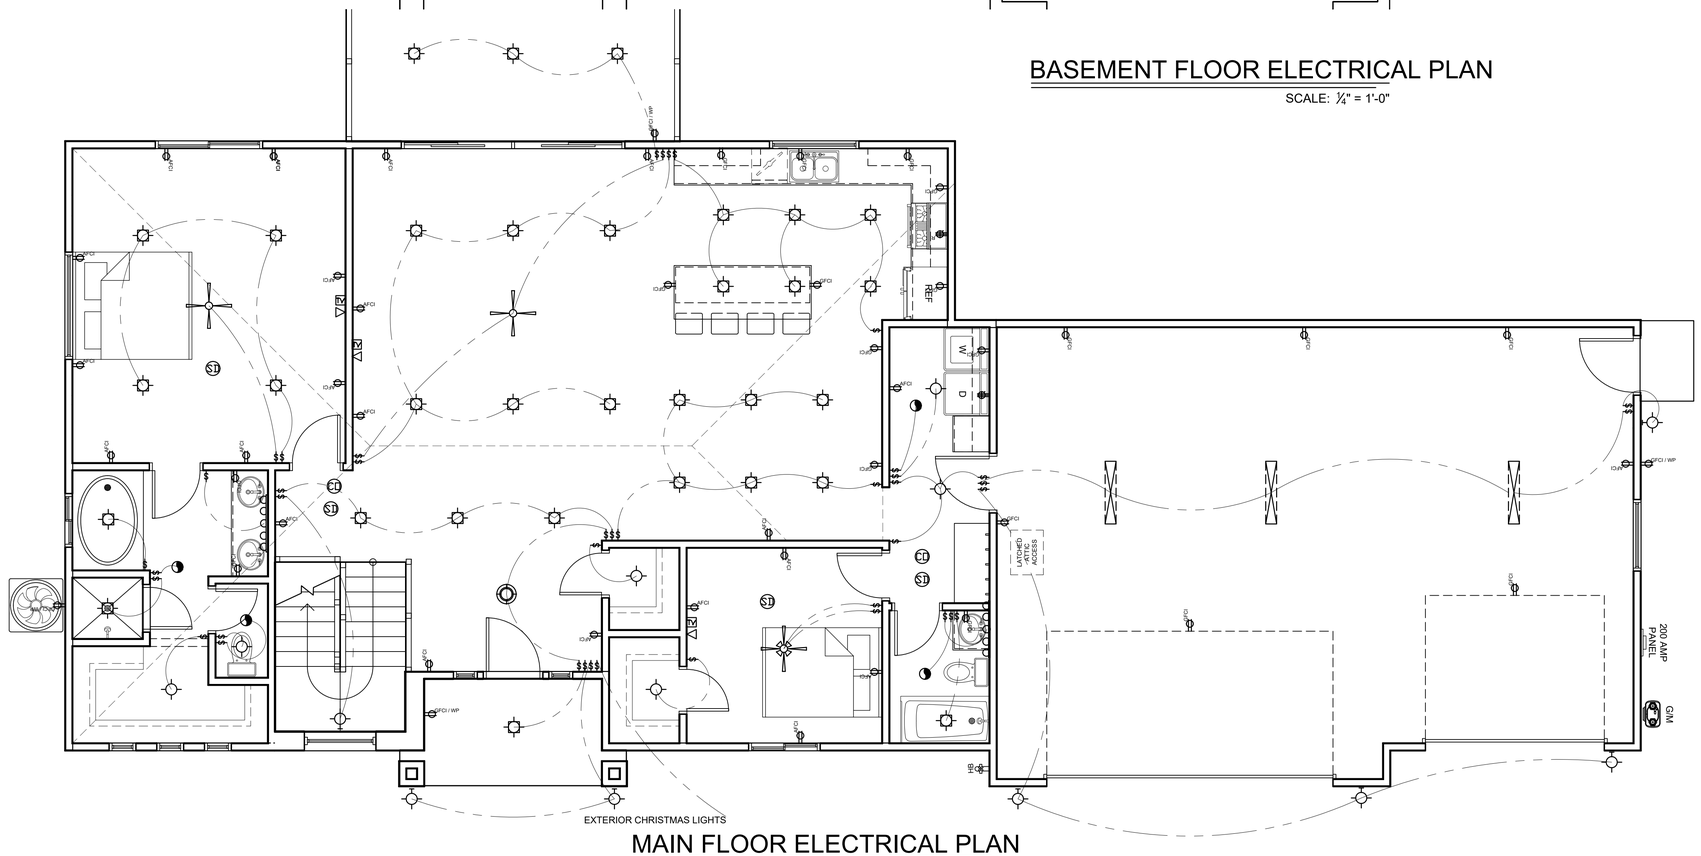

MAIN FLOOR ELECTRICAL PLAN

SCALE: ¼" = 1'-0"

DRAWN BY	JLF
PROJECT #	20-142
REV.1	-
REV.2	-
FINAL REV.	1/11/2021

COOPER RESIDENCE
305 W. Shangri-La
Toquerville, UT 84774

ELECTRICAL PLANS

J. LONNIE FOX
DRAFTING AND DESIGN
phone:(801) 781-1442 • jlonniefox@gmail.com • www.jlfdraftingdesign.com

BASEMENT SQFT	1713
MAIN FLR SQFT	1705
2ND FLR SQFT	0
GARAGE SQFT	909
TOTAL FIN SQFT	3418
TOTAL SQFT	3418

SHEET #
E1.1

COPYRIGHT 2020 J. LONNIE FOX DRAFTING AND DESIGN. THE PURCHASER IS GRANTED A SINGLE USE LICENSE FOR CONSTRUCTION ONLY. THESE PLANS ARE COPYRIGHTED AND ARE SUBJECT TO COPYRIGHT PROTECTION AS AN "ARCHITECTURAL WORK" UNDER THE COPYRIGHT ACT.