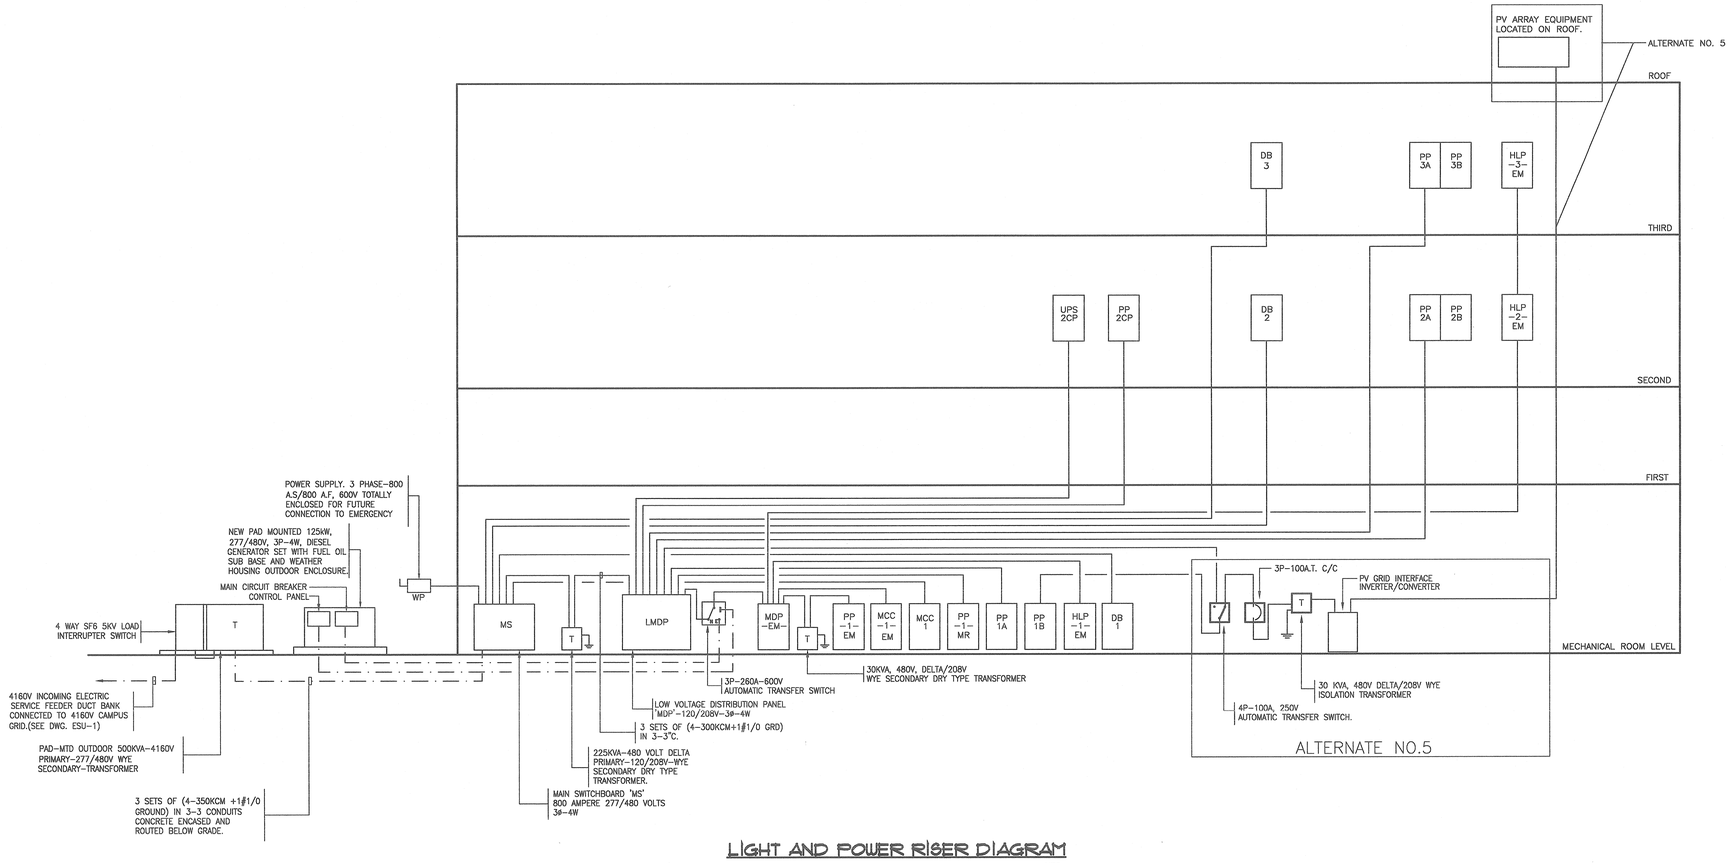

LIGHT AND POWER RISER DIAGRAM

NTS

SWITCHBOARD: MS — V L TO L: 480 — ϕ: 3 — WIRE: 4+G
BUS RATING: 800A — V L TO N: 277 — HZ: 60
SCA SYM: 60,000A

CKT#	SERVES	KVA(HP)	AMPS	CIRCUIT BREAKER POLES	FRAME	TRIP	FEEDER NO.	SIZE	GRD	CONDUIT NO.	SIZE	REMARKS
	INCOMING SERV. MTR SECT											
1	MAIN			3	800	800						
2	MDP VIA TRANSF.	225		3	400	300	3	500KCM	4	1	3-1/2"	
3	MDP-EM (VIA ATS)	156	186	3	225	225	4	250KCM	6	1	2"	HMCP C/B
4	DB-1			3	225	100	4	2	8	1	1-1/2"	
5	DB-2			3	225	100	4	2	8	1	1-1/2"	
6	DB-3			3	225	100	4	2	8	1	1-1/2"	
7	AHU-1			3	225	125	3	2	8	1	1-1/4"	HMCP C/B
8	AHU-2			3	225	125	3	2	8	1	1-1/4"	HMCP C/B
9	MCC-1			3	225	150	3	1/0	6	1	2"	
10	SPARE			3								
11	SPARE			3								
12	SPARE			3								
13												
14												
15												
16												
17												
18												

DISTR. PANEL: LMDP — V L TO L: 120/208 — ϕ: 3 — WIRE: 4+G
BUS RATING: 800A — V L TO N: 120/208 — HZ: 60
SCA SYM: 22,000A

CKT#	SERVES	KVA(HP)	AMPS	CIRCUIT BREAKER POLES	FRAME	TRIP	FEEDER NO.	SIZE	GRD	CONDUIT NO.	SIZE	REMARKS
	MAIN			3	800	800						
1	PP-1A			3	225	125	4	3/0	6	1	2 1/2"	
2	PP-1B			3	225	100	4	2	8	1	1 1/2"	
3	PP-2A			3	225	175	4	3/0	6	1	2 1/2"	
4	PP-2B			3	225	125	4	1/0	6	1	2"	
5	PP-3A			3	225	175	4	3/0	6	1	2 1/2"	
6	PP-3B			3	225	100	4	2	8	1	1 1/2"	
7	PP-2CP			3	225	175	4	3/0	6	1	2 1/2"	
8	UPS-2CP			3	225	175	4	3/0	6	1	2 1/2"	
9	PP-1MR			3	225	150	4	3/0	6	1	2 1/2"	
10	SPARE			3	225							
11	SPARE			3	225							
12	SPACE											

PANEL SCHEDULES

VOLTS: 120/208
PHASE: 3
WIRES: 4+G

PANEL DESIGN.	MOUNTING	BUS SIZE AMPERES	MAINS: BREAKERS SYM A.I.C.	TRIP AMPS	LUGS ONLY	SWITCH AMPS	FUSE AMPS	FUSE TYPE	BRANCH CIRCUITS POLES	TRIP AMPS	SYM A.I.C.	ACTIVE	SPARES	SPACES	TOTAL	REMARKS
PP-1A	S	225	22K	100					1	20	10K	23			42	
									1	30	10K	1	-	-		
PP-1B	S	225	22K	100					1	20	10K	42			42	
PP-2A	S	225	22K	100					1	20	10K	42			42	
SECT-I																
PP-2A	S	225	22K	100					1	20	10K	-	12	6	18	
SECT-II																
PP-2B	S	225	22K	100					1	20	10K	42			42	
PP-3A	S	225	22K	100					1	20	10K	42			42	
SECT-I																
PP-3A	S	225	22K	100					1	20	10K	-	12	6	18	
SECT-II																
PP-3B	S	225	22K	100					1	20	10K	42			42	

PANEL SCHEDULES

VOLTS: 277/480
PHASE: 3
WIRES: 4+G

PANEL DESIGN.	MOUNTING	BUS SIZE AMPERES	MAINS: BREAKERS SYM A.I.C.	TRIP AMPS	LUGS ONLY	SWITCH AMPS	FUSE AMPS	FUSE TYPE	BRANCH CIRCUITS POLES	TRIP AMPS	SYM A.I.C.	ACTIVE	SPARES	SPACES	TOTAL	REMARKS
HLP-1-EM	S	100	22K	50					1	20	10K	12			12	
HLP-2-EM	S	100	22K	50					1	20	10K	12			12	
HLP-3-EM	S	100	22K	50					1	20	10K	12			12	

M.E. RINKER, Sr. HALL
SCHOOL OF BUILDING CONSTRUCTION

UNIVERSITY OF FLORIDA-GAINESVILLE
PROJECT NO. BR-191

ARCHITECTS
CROXTON COLLABORATIVE/
GOULD EVANS ASSOCIATES

CROXTON COLLABORATIVE ARCHITECTS
475 FIFTH AVENUE
NEW YORK, NY 10017
TEL 212.683.1998
FAX 212.683.2799

GOULD EVANS ASSOCIATES
5405 WEST CYPRESS STREET
TAMPA, FL 33607
TEL 813.288.0729
FAX 813.288.0231

MECHANICAL ENGINEERS
LEHR ASSOCIATES
130 WEST 30TH STREET
NEW YORK, NY 10001-4092
TEL 212.947.8050
FAX 212.967.2059

STRUCTURAL ENGINEERS
WALTER P. MOORE
201 EAST KENNEDY BOULEVARD
TAMPA, FL 33602
TEL 813.221.2424
FAX 813.221.2289

CIVIL ENGINEERS
BROWN & CULLEN, INC.
3530 NW 43 STREET
GAINESVILLE, FL 32605
TEL 352.375.8999
FAX 352.375.0833

LANDSCAPE ENGINEERS
McCLAIN DESIGN GROUP, INC.
1843 NW 39 DRIVE
GAINESVILLE, FL 32605
TEL 352.372.2808
FAX 352.372.6622

CONSULTANT
SEEGY-BISCH
AUSSERE SULZBACHER STR. 118
NURNBERG, GERMANY
TEL 0911/59 90 99
FAX 0911/59 98 05

LOUIS J. LAY
CERTIFICATE No. 29915
STATE OF FLORIDA
REGISTERED PROFESSIONAL ENGINEER

THIS DRAWING, AS AN INSTRUMENT OF SERVICE, IS AND SHALL REMAIN, PROPERTY OF CROXTON COLLABORATIVE ARCHITECTS. THIS DRAWING SHALL NOT BE REPRODUCED, PUBLISHED, USED ON OTHER PROJECTS, USED FOR ADDITIONS, OR USED IN COMPLETION OF THIS PROJECT BY OTHERS EXCEPT BY AGREEMENT IN WRITING. ©2001 CROXTON COLLABORATIVE ARCHITECTS/ GOULD EVANS ASSOCIATES.

NO.	ISSUE/REVISION	DATE

100% CONSTRUCTION DOCUMENTS

DRAWING NAME
LIGHTING & POWER RISER DIAGRAM & PANEL SCHEDULE

DATE 11/21/01
SCALE NTS
DRAWN BY/CHECKED BY NA/JH
DRAWING NUMBER E004

G:\4440\ELEC\4440E004RBS.dwg Nov 20, 2001 - 10:41:55 nagata