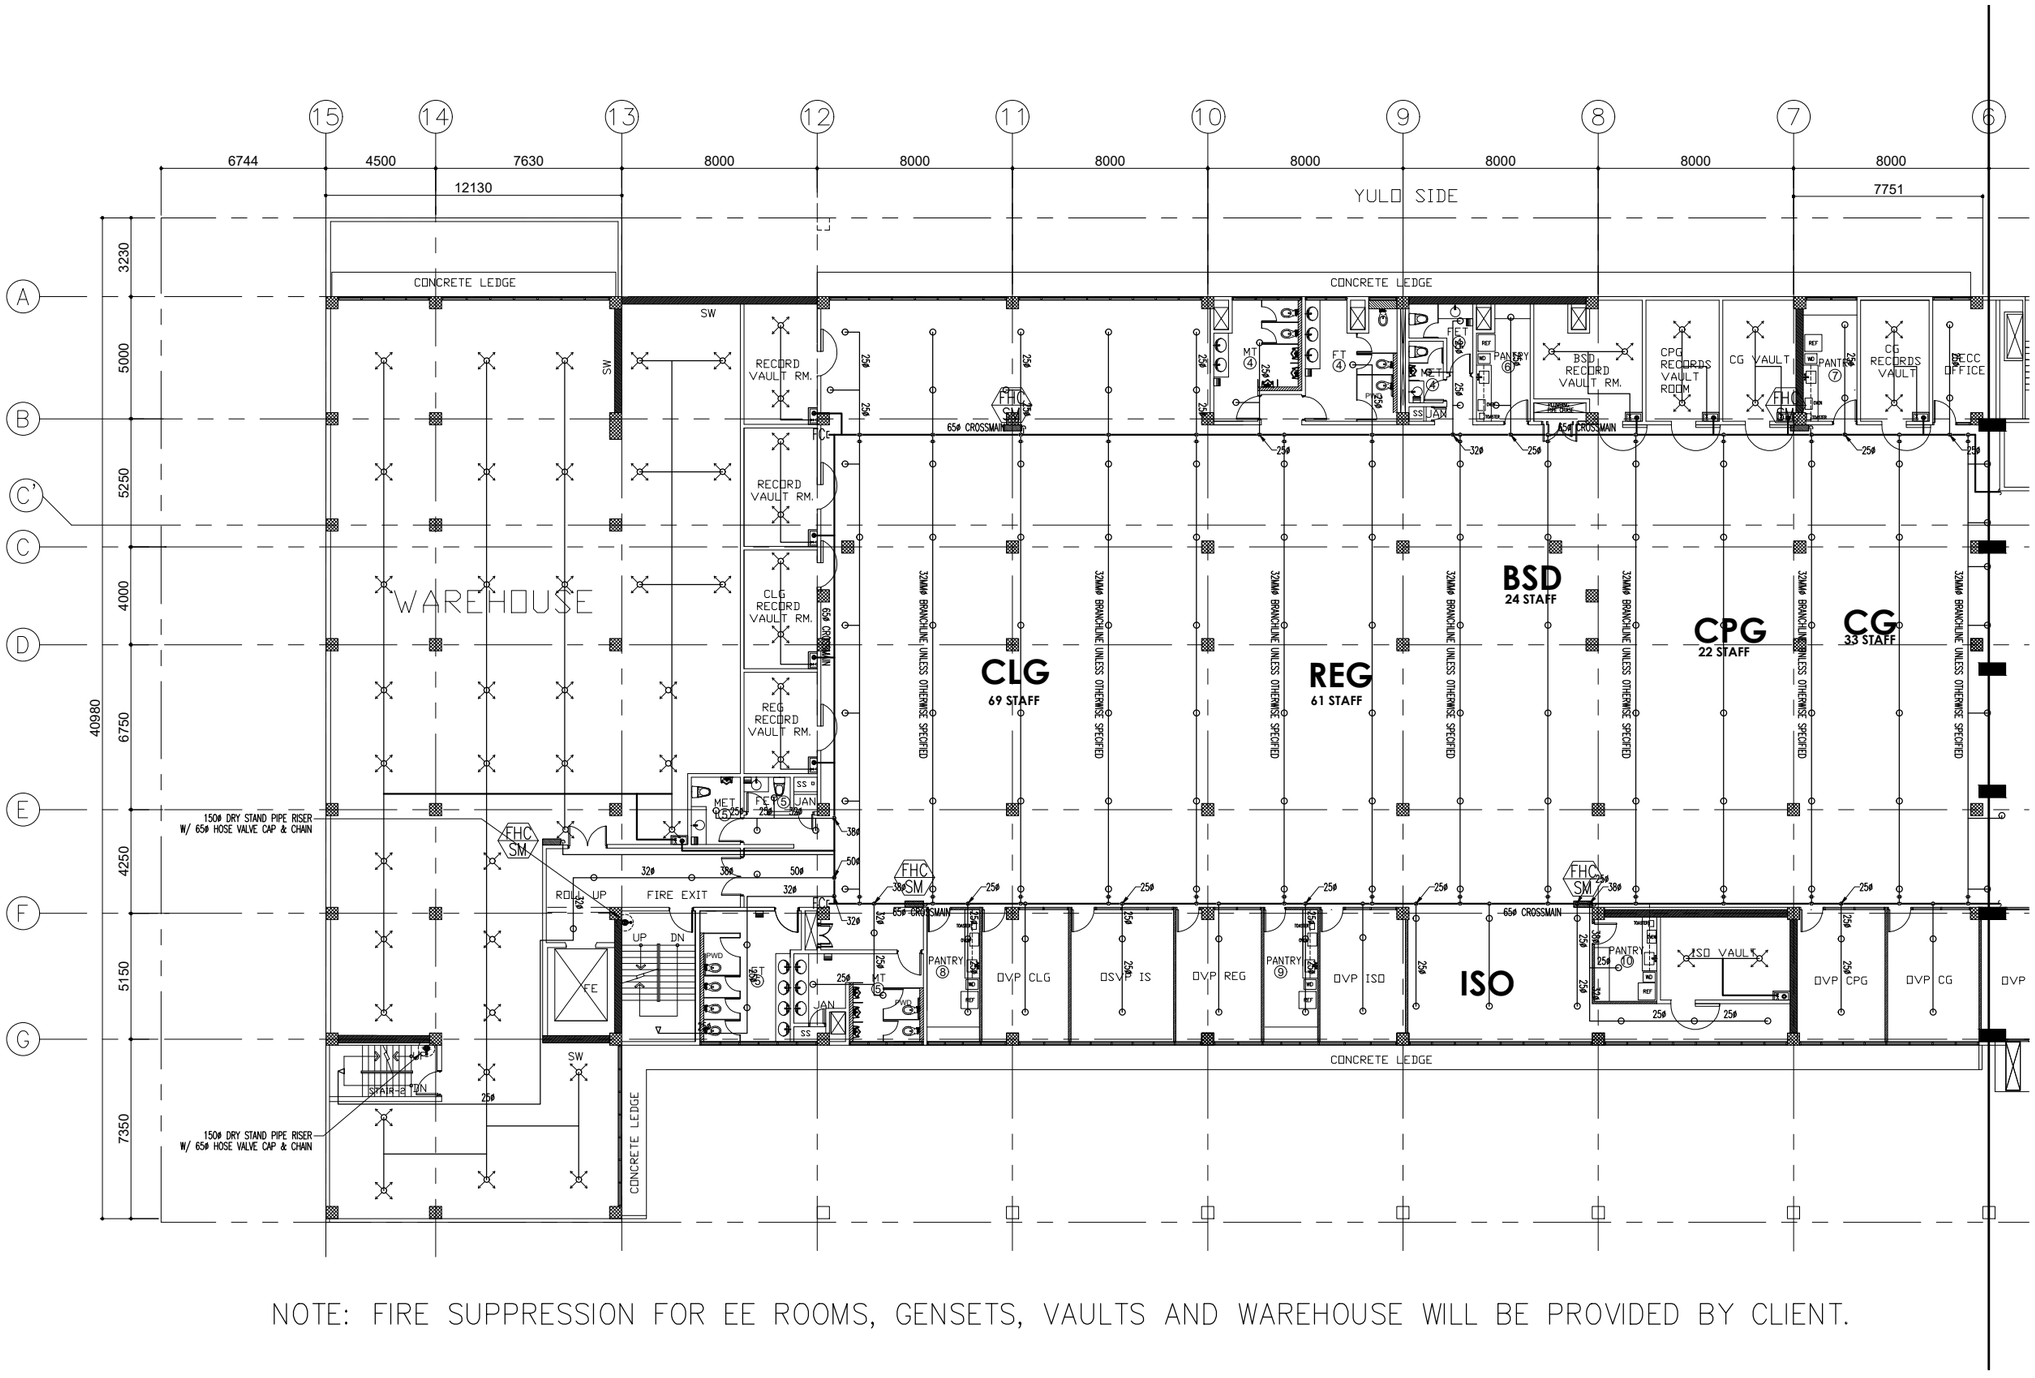

NOTE: FIRE SUPPRESSION FOR EE ROOMS, GENSETS, VAULTS AND WAREHOUSE WILL BE PROVIDED BY CLIENT.

FOURTH FLOOR PLAN FIRE PROTECTION LAYOUT

A / FP-05 SCALE 1:100

GRAPHIC SCALE: 0 2 4 6 8

SCALE 1:100 M

NOTE: CHECK GRAPHIC SCALE PRIOR TO SCALING

CONSULTANT		OWNER	APPROVED BY:	PROJECT TITLE	SHEET CONTENT/S :	ISSUE NO.	REVISIONS	NO.	DATE		DATE	SHEET NO.
E. H. SISON ENGINEERS, CO. ENGINEERS * PLANNERS * CONSULTANTS 3431 GUERNICA ST., PALANAN, MAKATI CITY TEL. Nos. 8317115, 8337030	RAMON D. AGUILOS PROFESSIONAL MECHANICAL ENGINEER PTR NO.: 2464195 D — PRC NO. : 2736 DATE : 01-05-22 — TIN NO. : 137-133-799 PLACE : QUEZON CITY	PDIC	CYRUS T. GALANG VICE PRESIDENT ADMINISTRATIVE SERVICES GROUP	RENOVATION OF PDIC BUILDING IN CHINO ROCES LOCATION: 2228 CHINO ROCES AVENUE, MAKATI CITY	FOURTH FLOOR PLAN FIRE PROTECTION LAYOUT					DESIGNED BY: RDAEC CADD BY: RJA CHECKED BY: APPROVED BY: SCALE: AS SHOWN		FP-05