© GRIMM AND PARKER, P.C. 2014

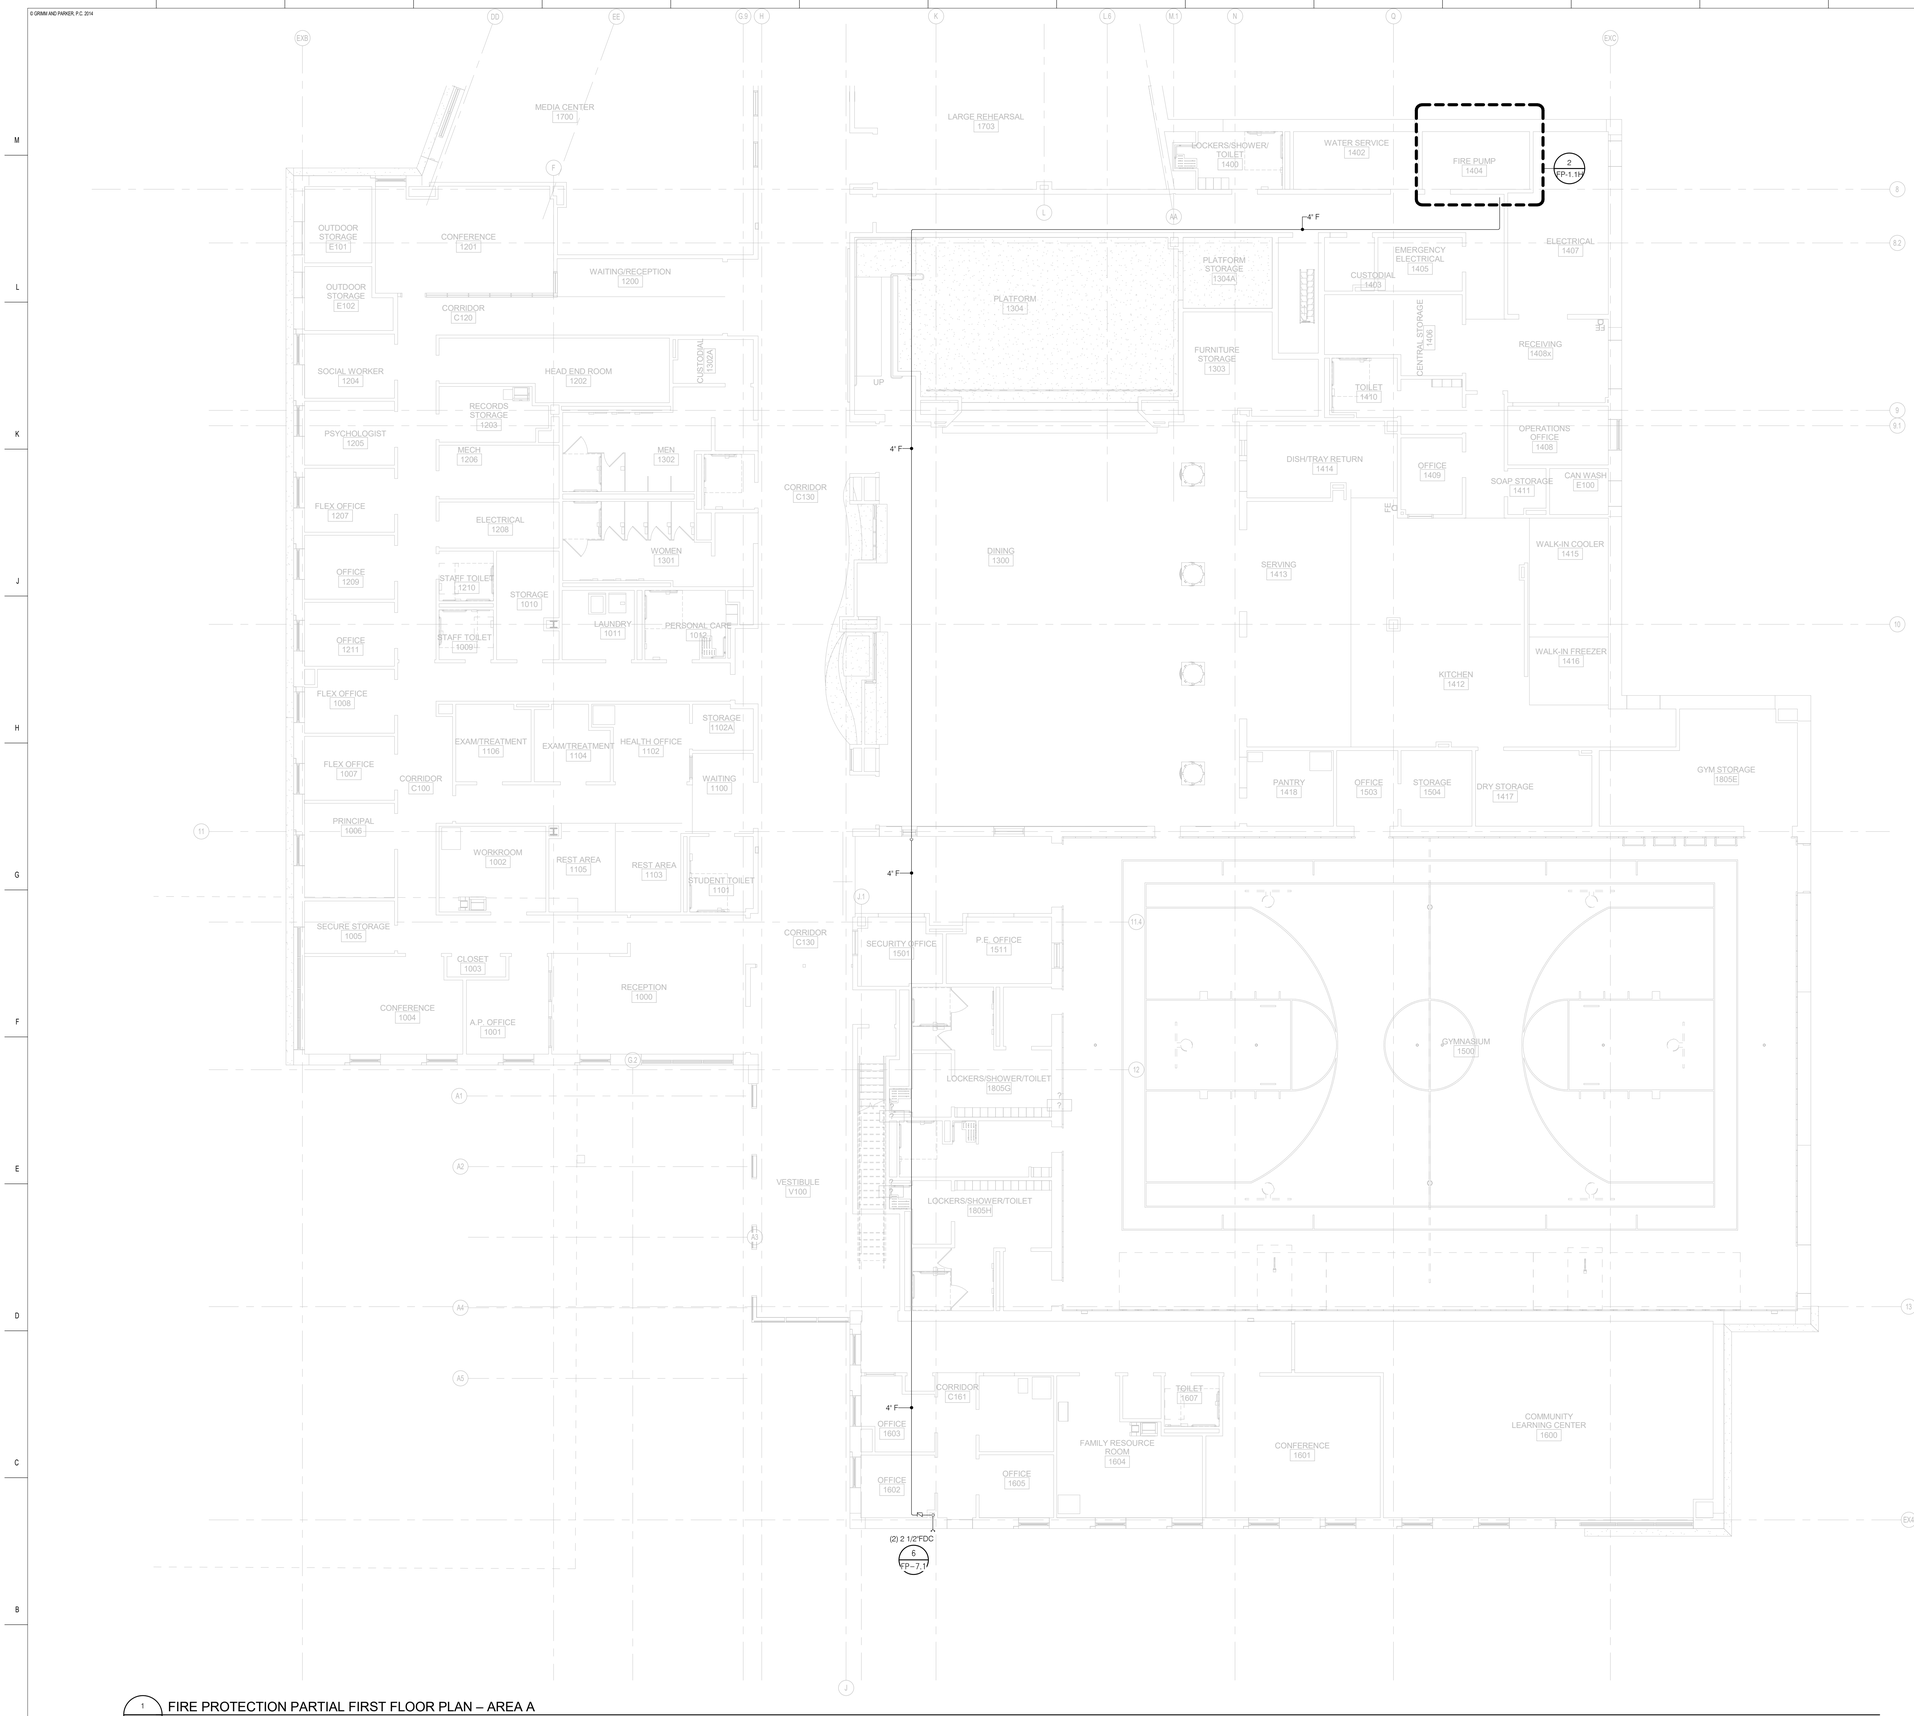

1 FP-1.1H FIRE PROTECTION PARTIAL FIRST FLOOR PLAN – AREA A
SCALE: 1/8" = 1'-0"

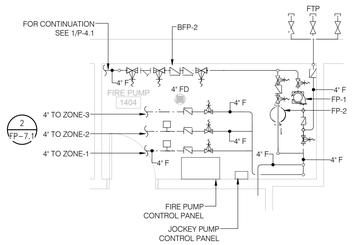

2 FP-1.1H FIRE PROTECTION ENLARGE PLAN- AREA A
SCALE: NOT TO SCALE

KEY PLAN

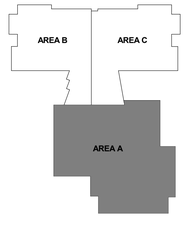

SETTY
ONE SOUTH STREET, SUITE 1130
BALTIMORE, MARYLAND 21202
TEL 667-329-5035
MAINTENANCE MANAGEMENT · ENERGY MANAGEMENT
ENERGY MANAGEMENT SERVICES · CITIZEN BUILDER SERVICES
CAPITAL PROJECT MANAGEMENT · CAPITAL PROJECT SERVICES
DISTRICT OF COLUMBIA · MARYLAND
www.SETTY.com

SAC#17-1 # # # #

PROJECT NUMBER

11720 Beltsville Drive
Suite 600
Calverton, MD 20705
Tel: 301.595.1000

www.grimmandparker.com

GRIMM AND PARKER

GP# 21553

FIRE PROTECTION PARTIAL FIRST FLOOR PLAN – AREA A

HOLABIRD ACADEMY PK-8
CITY OF BALTIMORE, MARYLAND

DATE	DESCRIPTION

FP-1.1H

03/13/2017
BID SET

© GRIMM AND PARKER, P.C. 2014