© GRIMM AND PARKER, P.C. 2014

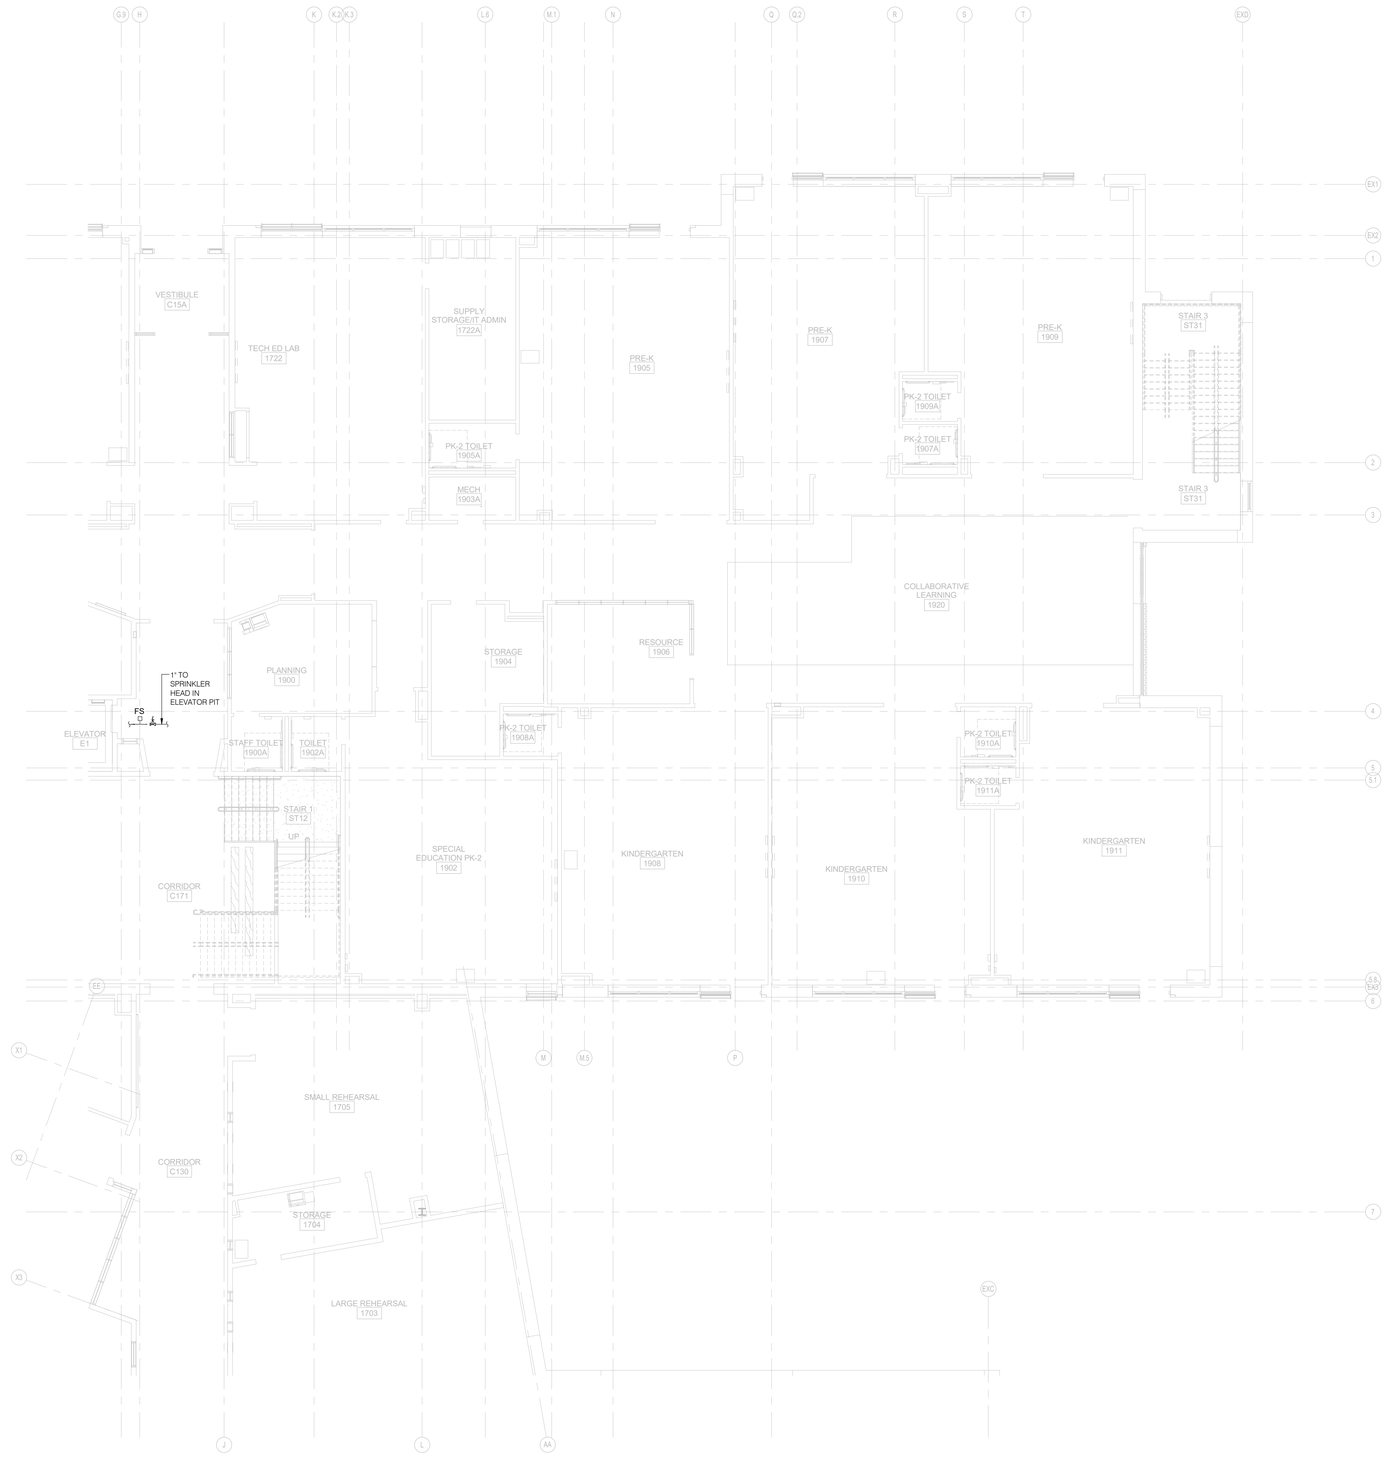

1 FP-1.2 FIRE PROTECTION PARTIAL FIRST FLOOR PLAN – AREA C

SCALE: 1/8" = 1'-0"

KEY PLAN

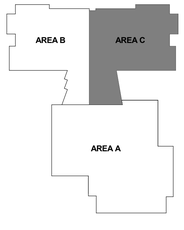

SETTY
ONE SOUTH STREET, SUITE 1110
BALTIMORE, MARYLAND 21202
TEL 667-329-0035
MAINTENANCE MANAGEMENT SERVICES • ENERGY MANAGEMENT
ENERGY MANAGEMENT SERVICES • DESIGN BUILD SERVICES
CAPITAL PROJECT MANAGEMENT SERVICES
DISTRICT OF COLUMBIA • MARYLAND
www.SETTY.com
SAMPLE TITLE BLOCK
PROJECT NUMBER

11720 Beltsville Drive
Suite 600
Calverton, MD 20705
Tel: 301.595.1000
www.grimmandparker.com
GRIMM AND PARKER

GP# 21553

FIRE PROTECTION PARTIAL FIRST FLOOR PLAN – AREA C

HOLABIRD ACADEMY PK-8
CITY OF BALTIMORE, MARYLAND

DATE	DESCRIPTION

FP-1.2

03/13/2017
BID SET

© GRIMM AND PARKER, P.C. 2014