© GRIMM AND PARKER, P.C. 2014

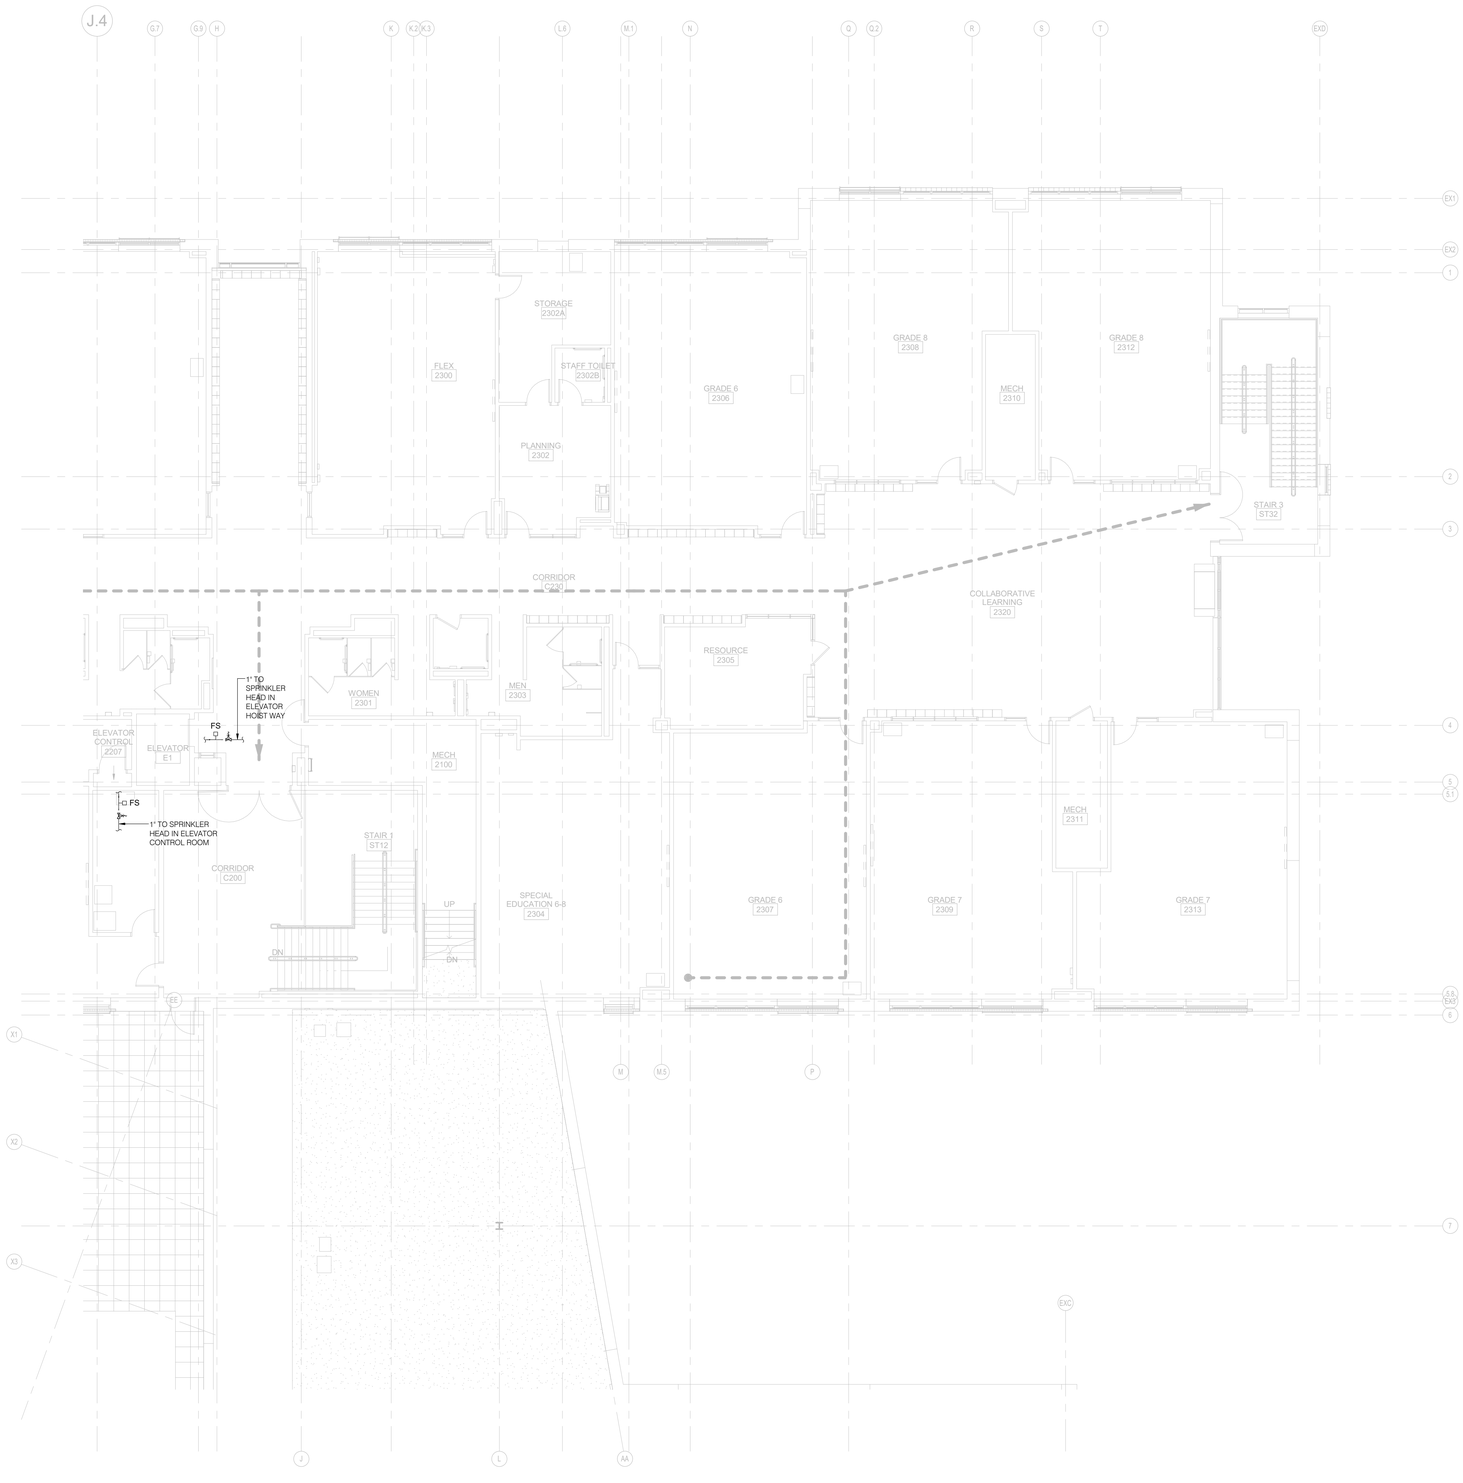

1 / FP-1.3 FIRE PROTECTION PARTIAL SECOND FLOOR PLAN – AREA C

SCALE: 1/8" = 1'-0"

KEY PLAN

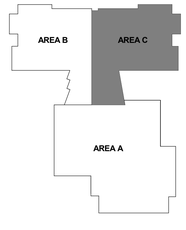

SETTY
ONE SOUTH STREET, SUITE 1110
BALTIMORE, MARYLAND 21202
TEL 410-539-5035
MAYOR'S OFFICE OF INFORMATION TECHNOLOGY
ENERGY MANAGEMENT SERVICES – DESIGN & CONSTRUCTION
CITY OF BALTIMORE, MARYLAND
CITY OF COLUMBIA, MARYLAND
www.SETTY.com

PROJECT NUMBER: 2016-CITY-B-P-P-P

11720 Beltsville Drive
Suite 600
Calverton, MD 20705
Tel: 301.595.1000
www.grimmandparker.com
GRIMM AND PARKER

GP# 21553

FIRE PROTECTION PARTIAL SECOND FLOOR PLAN – AREA C

HOLABIRD ACADEMY PK-8
CITY OF BALTIMORE, MARYLAND

DATE	DESCRIPTION

FP-1.3

03/13/2017
BID SET

© GRIMM AND PARKER, P.C. 2014