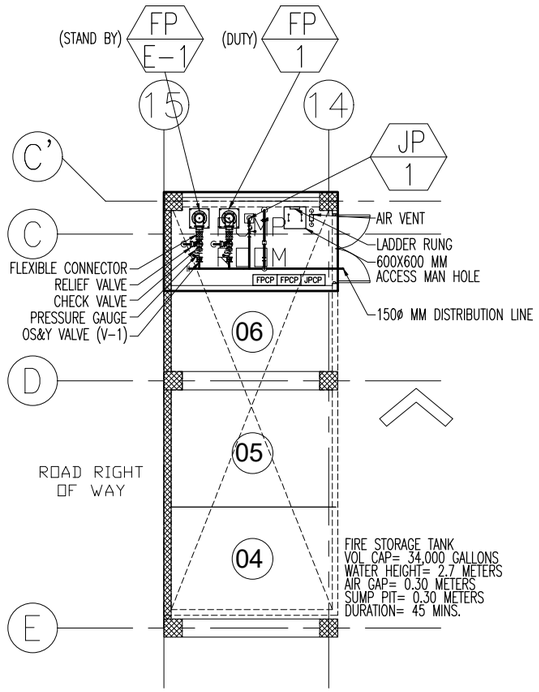

A FP-09 FIRE PUMP FLOOR PLAN
SCALE 1 : 150 mts.

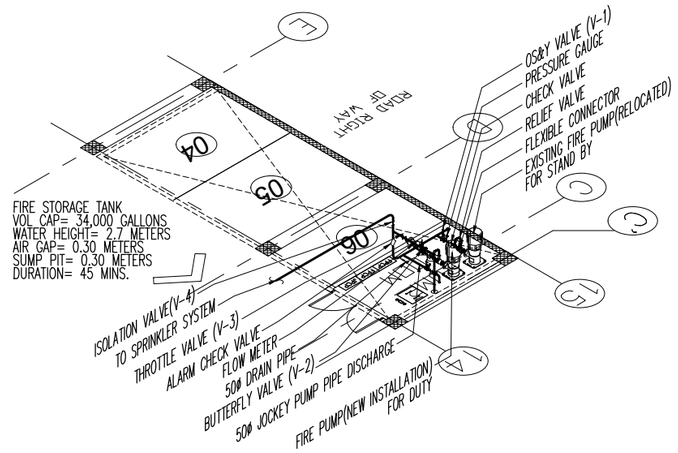

B FP-09 FIRE PUMP ISOMETRIC LAYOUT
SCALE 1 : 150 mts.

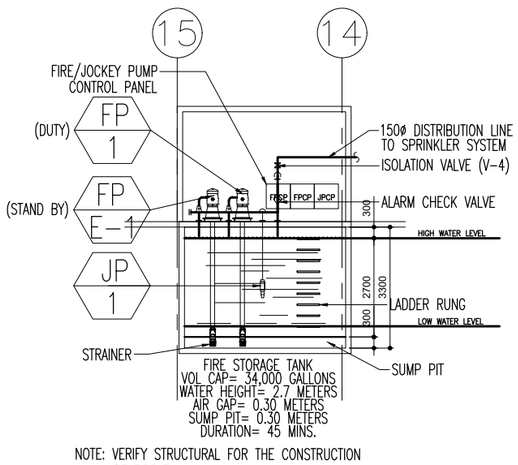

C FP-09 SECTION THRU "A"
SCALE 1 : 150 mts.

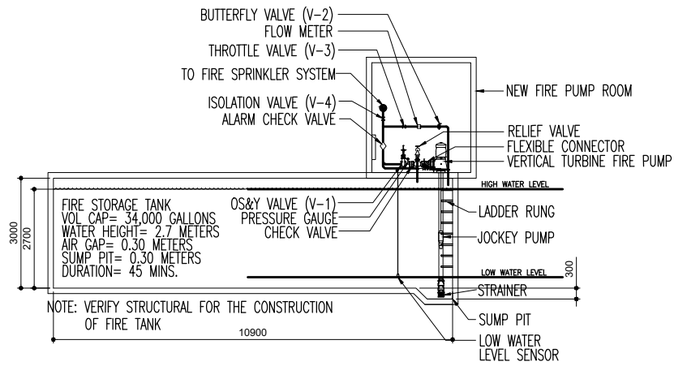

D FP-09 SECTION THRU "B"
SCALE 1 : 150 mts.

CONSULTANT		OWNER	APPROVED BY:	PROJECT TITLE	SHEET CONTENT/S :	ISSUE NO.	REVISIONS	NO.	DATE		DATE	SHEET NO.
E. H. SISON ENGINEERS, CO. ENGINEERS * PLANNERS * CONSULTANTS 3431 GUERNICA ST., PALANAN, MAKATI CITY TEL. Nos. 8317115, 8337030	RAMON D. AGUILOS PROFESSIONAL MECHANICAL ENGINEER PTR NO.: 2464195 D — PRC NO.: 2736 DATE : 01-05-22 — TIN NO. : 137-133-799 PLACE : QUEZON CITY	PHILIPPINE DEPOSIT INSURANCE CORPORATION PDIC	CYRUS T. GALANG VICE PRESIDENT ADMINISTRATIVE SERVICES GROUP	RENOVATION OF PDIC BUILDING IN CHINO ROCES LOCATION: 2228 CHINO ROCES AVENUE, MAKATI CITY	FIRE PUMP ARRANGEMENT DETAILS					DESIGNED BY: RDAEC CADD BY: RJA CHECKED BY: APPROVED BY: SCALE: AS SHOWN		FP-09