© GRIMM AND PARKER, P.C. 2014

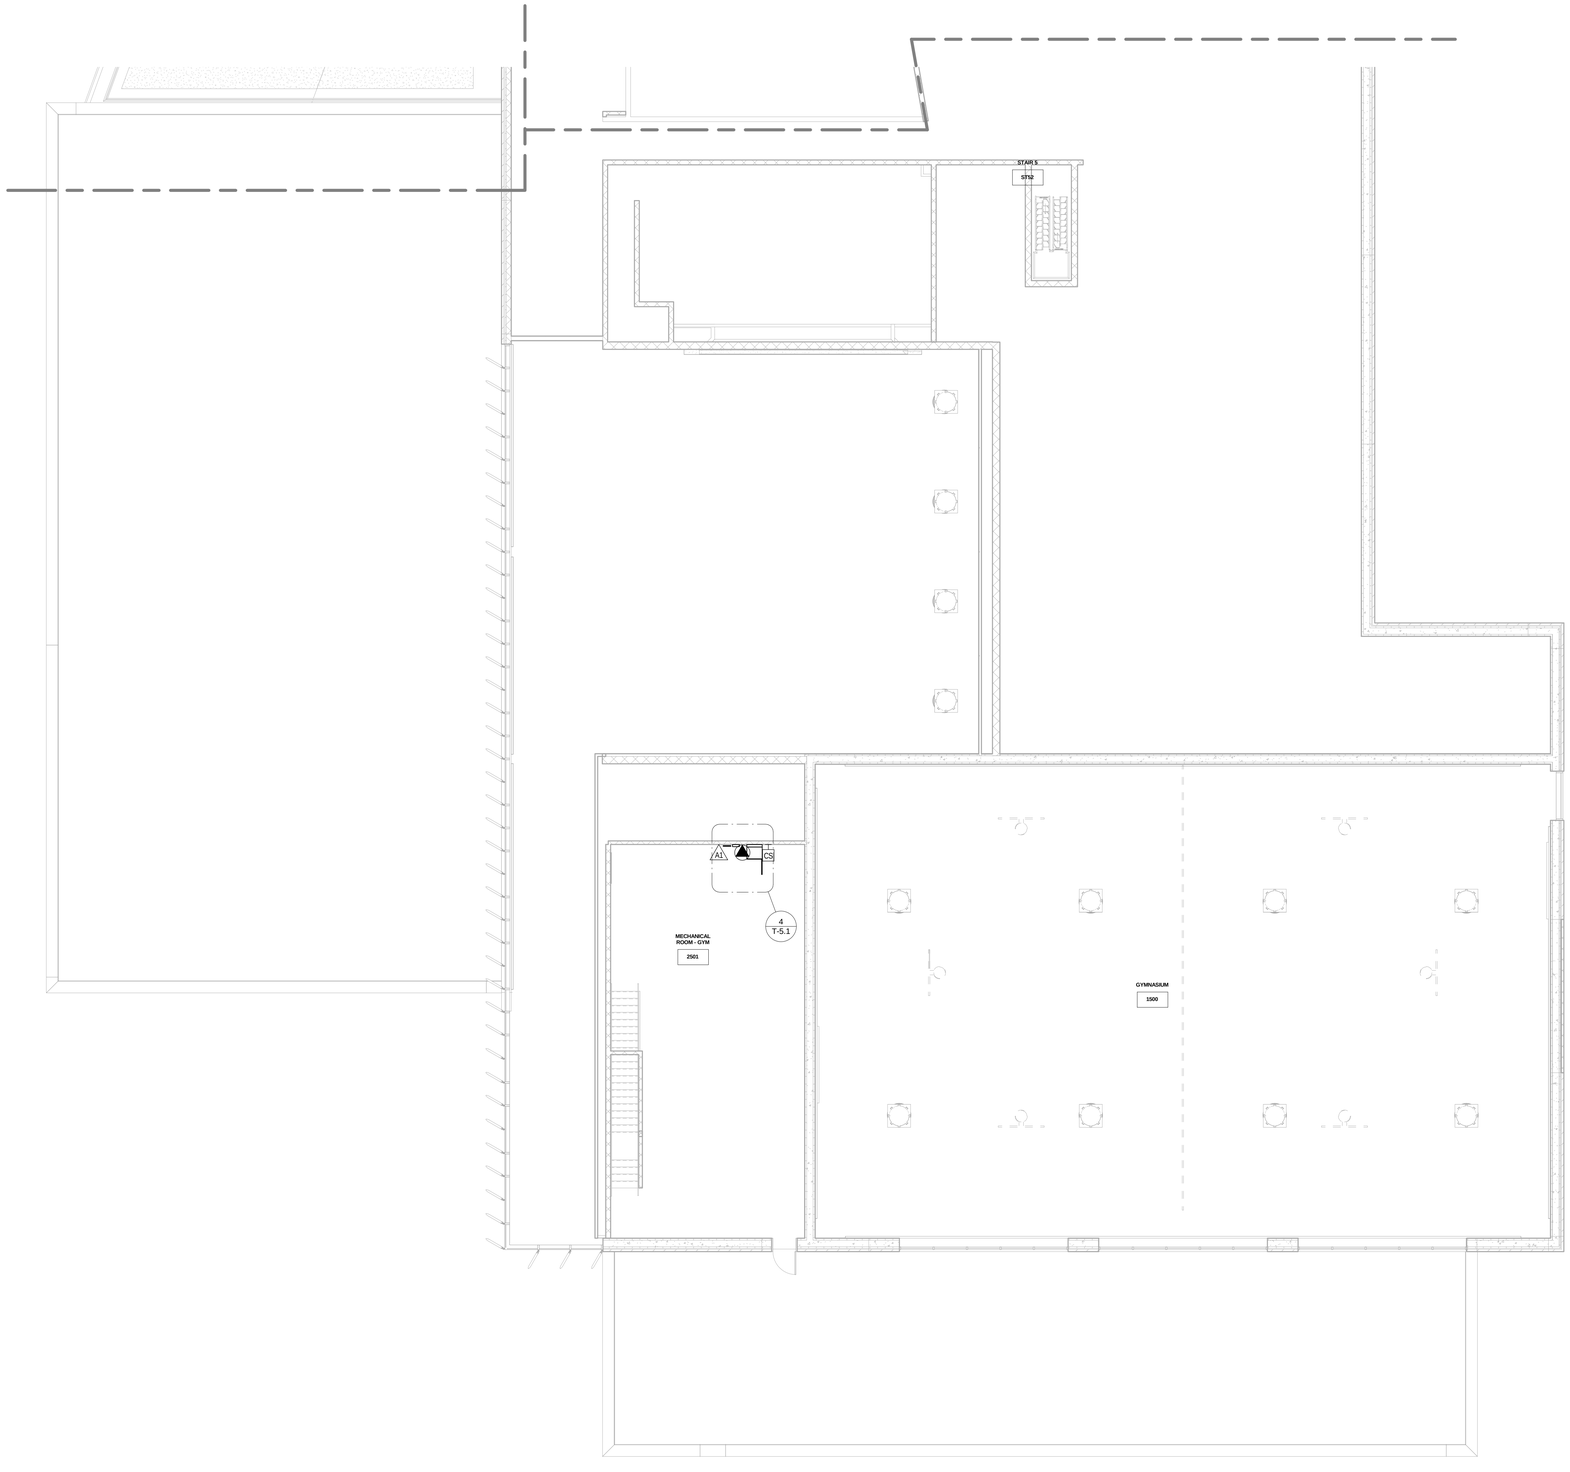

1 PARTIAL SECOND FLOOR PLAN - AREA A
1/8" = 1'-0"

Scale: 1 inch = 8 feet

0 4' 8' 16' 24' 32'

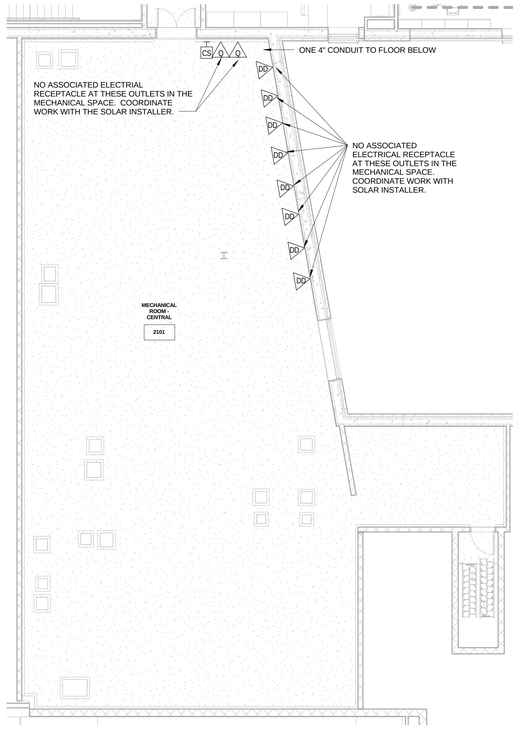

2 MECHANICAL LEVEL
1/8" = 1'-0"

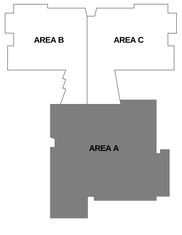

N

49 Old Solomons Island Rd.
Suite 301
Annapolis, MD 21401
Tel: 410.573.9148

Educational Facilities Planning
Designs for Learning

11720 Beltsville Drive
Suite 600
Calverton, MD 20705
Tel: 301.595.1000

www.grimmandparker.com

GRIMM AND PARKER

GP# 21553

PARTIAL SECOND FLOOR PLAN - AREA A

HOLABIRD ACADEMY PK-8
CITY OF BALTIMORE, MARYLAND

DATE	DESCRIPTION

T-1.4

03/13/2017
BID SET

© GRIMM AND PARKER, P.C. 2014