© GRIMM AND PARKER, P.C. 2014

TAGGED NOTES	
A32	EXHAUST FAN SERVING KITCHEN HOOD. REFER TO SHEET M-4.1 FOR CONTINUATION.
A34	EXHAUST FAN SERVING DISHWASHER CONDENSATE HOOD. REFER TO SHEET M-4.1 FOR CONTINUATION.
A73	MAINTAIN A MINIMUM OF 10'-0" FROM ROOF EDGE.
A74	ROOF HATCH. REFER TO ARCHITECTURAL ROOF PLAN.
A75	ACCESS DOOR FROM ROOF TO MECHANICAL ROOM - GYM 2501.

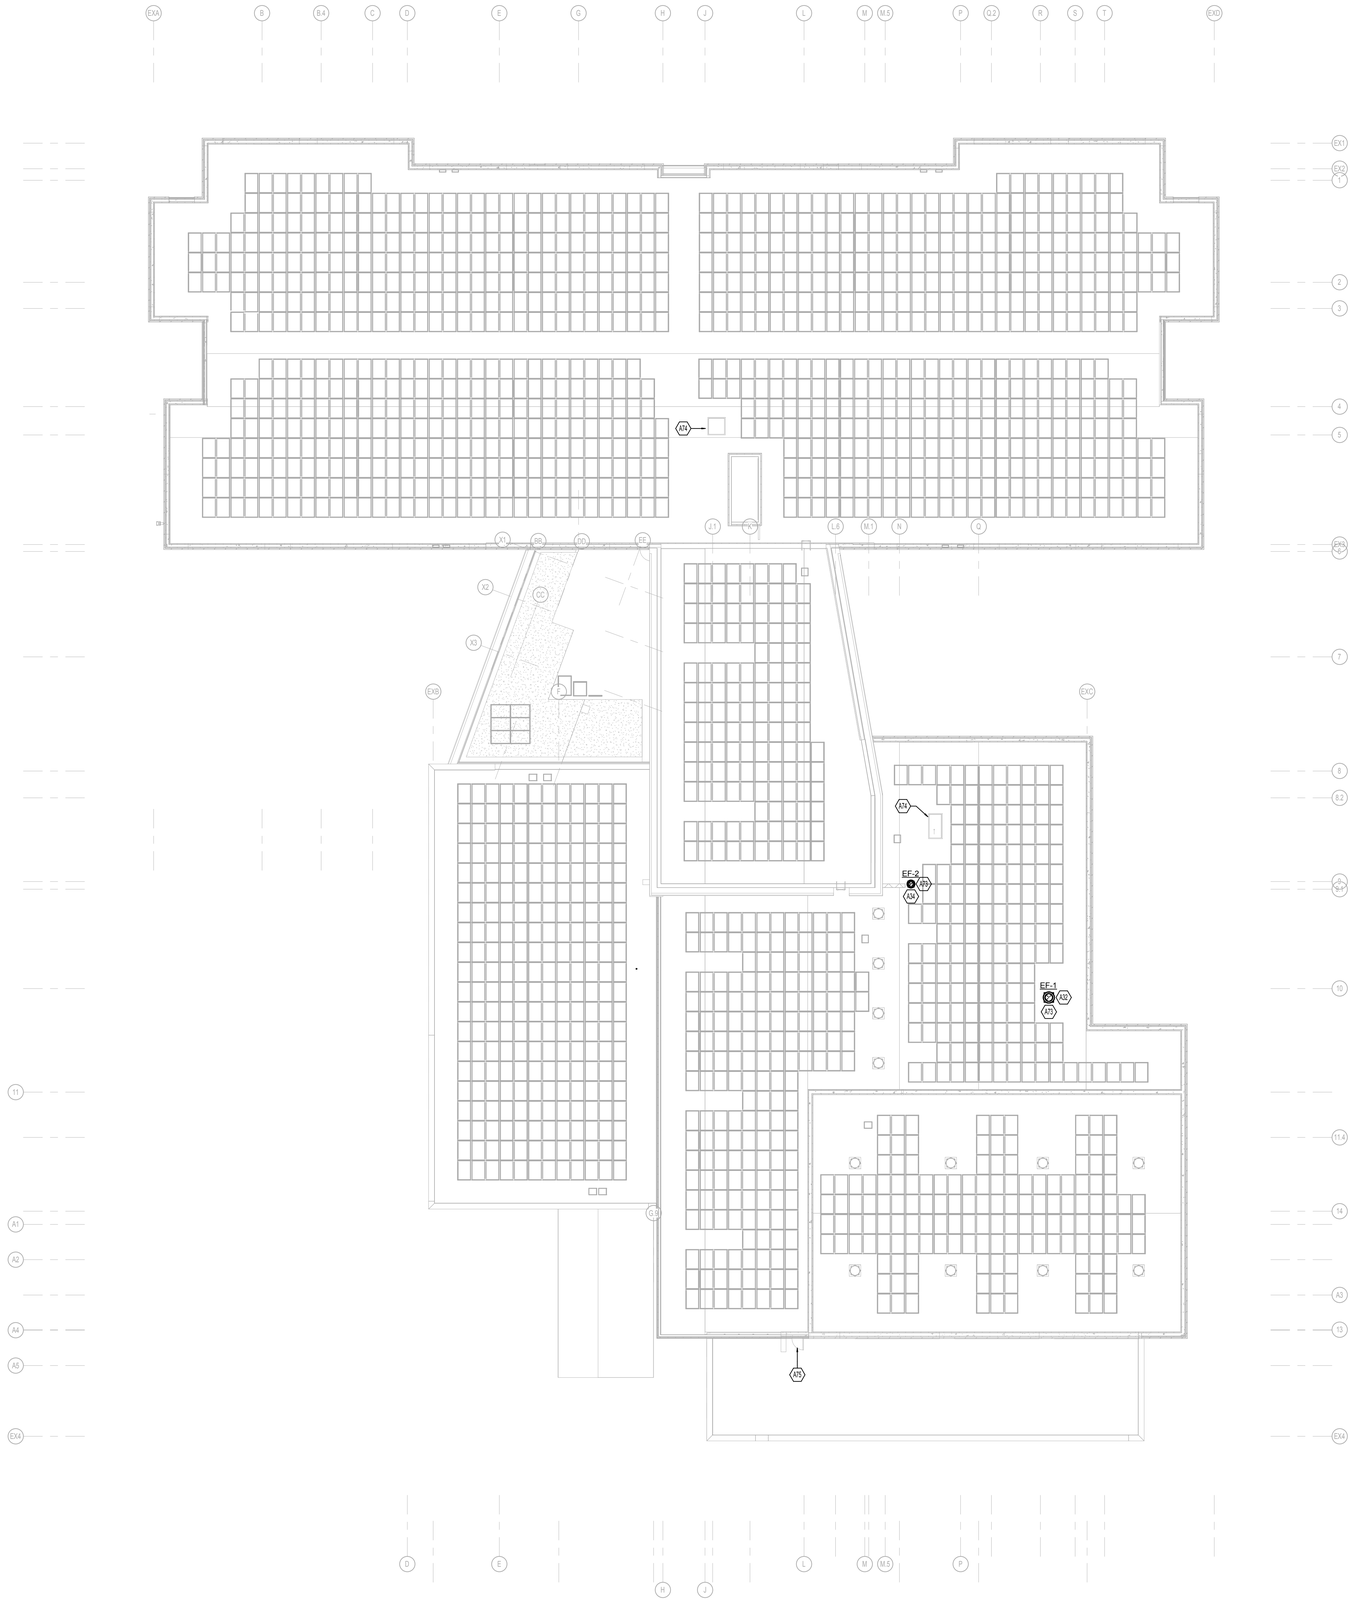

1 ROOF PLAN - MECHANICAL
SCALE: 1/16" = 1'-0"
0' 4' 8' 16' 32' 48' 64'

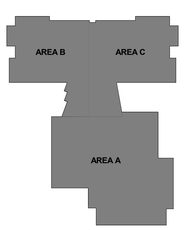

KEYPLAN

N

2429 Members Way
Lexington, Ky 40504
Tel: 859.253.0892
http://www.cmtaegis.com/

11720 Beltsville Drive
Suite 600
Calverton, MD 20705
Tel: 301.595.1000
www.grimmandparker.com

GRIMM AND PARKER

GP# 21553

MECHANICAL ROOF PLAN

HOLABIRD ACADEMY PK-8
CITY OF BALTIMORE, MARYLAND

DATE	DESCRIPTION

M-3.0

03/13/2017
BID SET

© GRIMM AND PARKER, P.C. 2014