© GRIMM AND PARKER, P.C. 2014

TAGGED NOTES

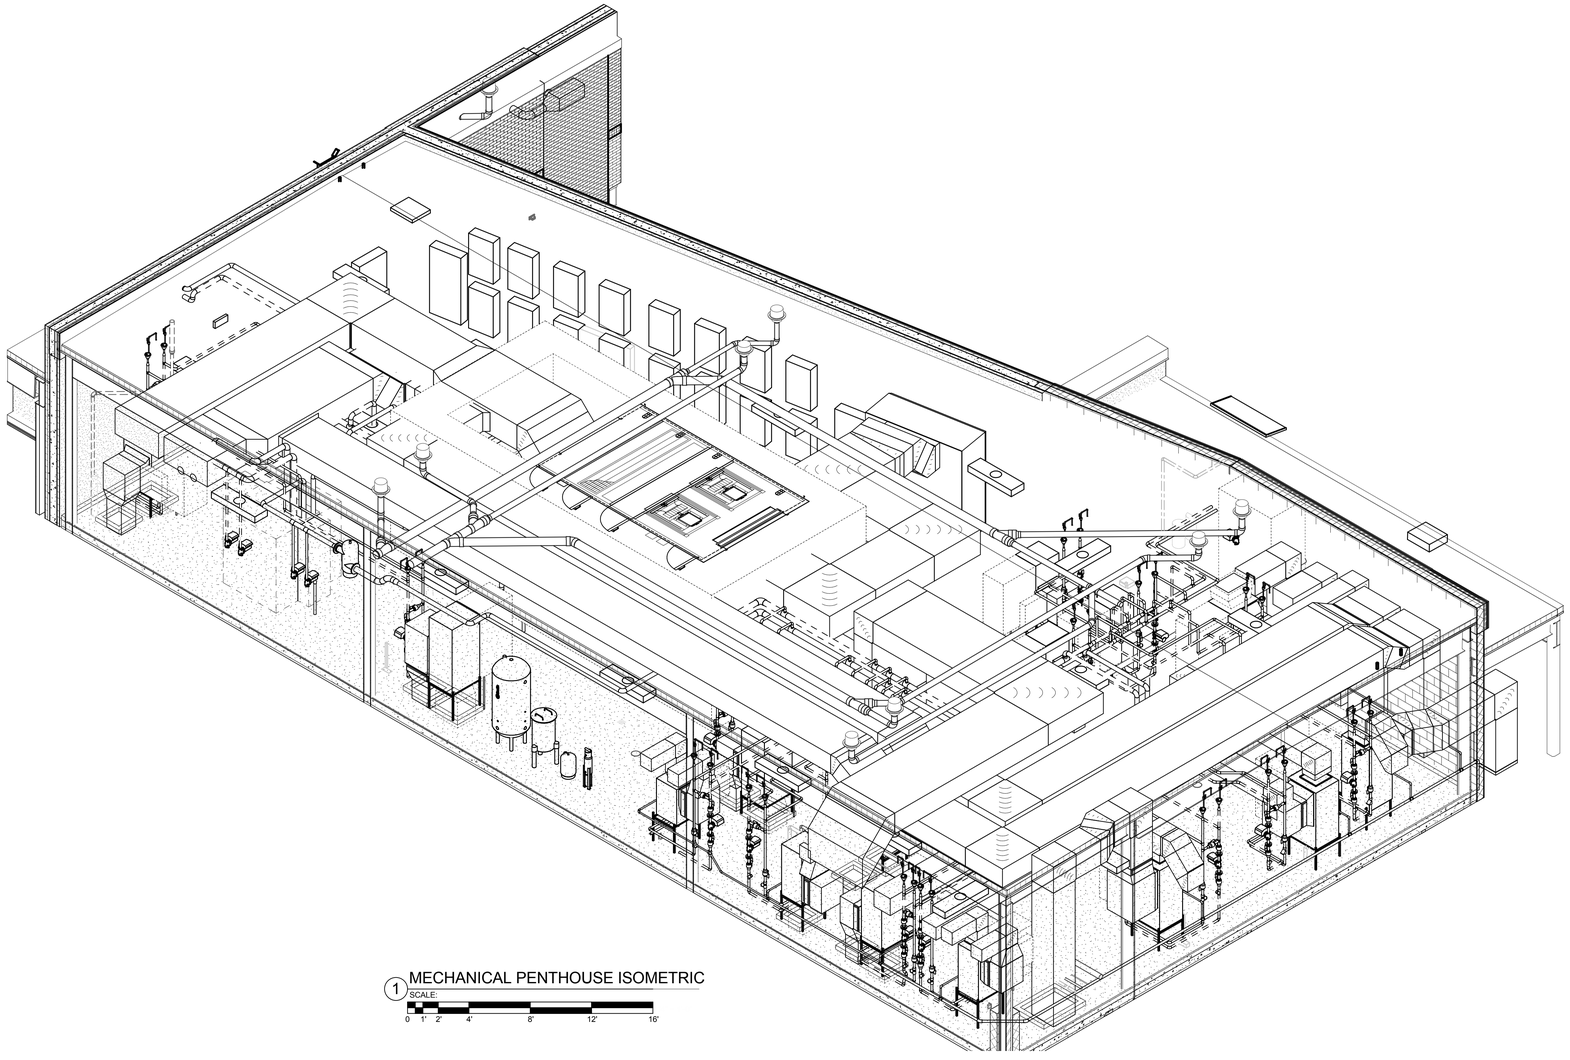

1 MECHANICAL PENTHOUSE ISOMETRIC

SCALE:

0 1' 2' 4' 8' 12' 16'

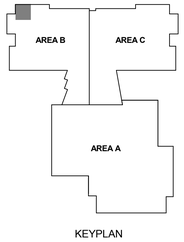

KEYPLAN

N

2429 Members Way
Lexington, Ky 40504
Tel: 859.253.0892

http://www.cmtaegis.com/

11720 Beltsville Drive
Suite 600
Calverton, MD 20705
Tel: 301.595.1000

www.grimmandparker.com

G+P GRIMM AND PARKER

GP# 21553

SECTIONS & ISOMETRICS

HOLABIRD ACADEMY PK-8
CITY OF BALTIMORE, MARYLAND

DATE	DESCRIPTION

M-5.0

03/13/2017
BID SET

© GRIMM AND PARKER, P.C. 2014