© GRIMM AND PARKER, P.C. 2014

GENERAL AIR DISTRIBUTION NOTES	
A	REFER TO R,G,D RUNOUT SCHEDULE FOR R,G,D DUCT SIZE.
B	REFER TO TYPICAL BRANCH DUCT SUPPLY/OUTSIDE/RETURN/EXHAUST AIR DETAIL.
C	REFER TO TRANSFER AIR GRILLE DETAIL.
D	COORDINATE REGISTERS, GRILLES, AND DIFFUSERS WITH REFLECTED CEILING PLANS AND LIGHTING PLANS.
E	REFER TO CAV/VAV BOX DETAIL.
F	REFER TO AIR TERMINAL UNIT SCHEDULE FOR ALL RUNOUT SIZED OF VAV AND CAV BOXES.
G	REFER TO REFLECTED CEILING PLANS. PROVIDE 12"x12" ACCESS PANEL PREPARED FOR PAINTING AND PAINTED IN ACCORDANCE WITH ARCHITECTURAL REQUIREMENTS. PROVIDE ACCESS PANELS FOR DAMPERS WHERE INDICATED ABOVE GYPSUM CEILINGS IN AREAS SUCH AS RESTROOMS, LOCKER ROOMS, CUSTODIAL AREAS, ETC.

TAGGED NOTES	
A38	ROUND DUCTWORK IS EXPOSED AND SHALL BE DOUBLE WALL DUCTWORK PREPARED FOR PAINTING AND PAINTED IN ACCORDANCE TO ARCHITECTURAL REQUIREMENTS.
A51	MOUNT R,G,D 10'-6" FROM FF.
A52	MOUNT R,G,D 10'-8" FROM FF. MATCH BLOCK COURSING.
A53	MOUNT CURVED SUPPLY DIFFUSERS MATCHING RADIUS OF DUCT 30 DEGREES DOWN FROM HORIZONTAL. TYPICAL IN MEDIA CENTER 1700.
A54	GEOTHERMAL PUMP ROOM 0001 LOCATED BELOW DASHED OUTLINE IN BASEMENT. REFER TO SHEET M4.0 FOR GEOTHERMAL PUMP ROOM 0001 MECHANICAL PLANS.
A55	40"x20" OA UP. REFER TO SHEET M4.0 FOR CONTINUATION.
A56	40"x20" EA UP. REFER TO SHEET M4.0 FOR CONTINUATION.
A78	
A79	
A80	

R, G, D RUNOUT SCHEDULE

MARK	BRANCH DUCT SIZE
E-1	6" DIA
E-1A	6" DIA
E-2	8" DIA
E-2A	10" DIA
E-3	10" DIA
E-4	12" DIA
E-5	14" DIA
E-7	SEE PLANS
E-9	SEE PLANS
E-10	48"x12"
R-1	6" DIA
R-2	8" DIA
R-3	10" DIA
R-4	12" DIA
R-5	14" DIA
R-6	16" DIA
R-7	SEE PLANS
R-8	12"x8"
R-9	SEE PLANS
R-10	SEE PLANS
R-11	18"x12"
R-13	SEE PLANS
R-14	SEE PLANS
S-1	6" DIA
S-1A	6" DIA
S-2	8" DIA
S-3	10" DIA
S-4	12" DIA
S-7	SEE PLANS
S-8	SEE PLANS
S-9	48"x5.25"
S-10	SEE PLANS
S-11	-
S-12	-
S-13	-
S-14	SEE PLANS
T-1	SEE PLANS

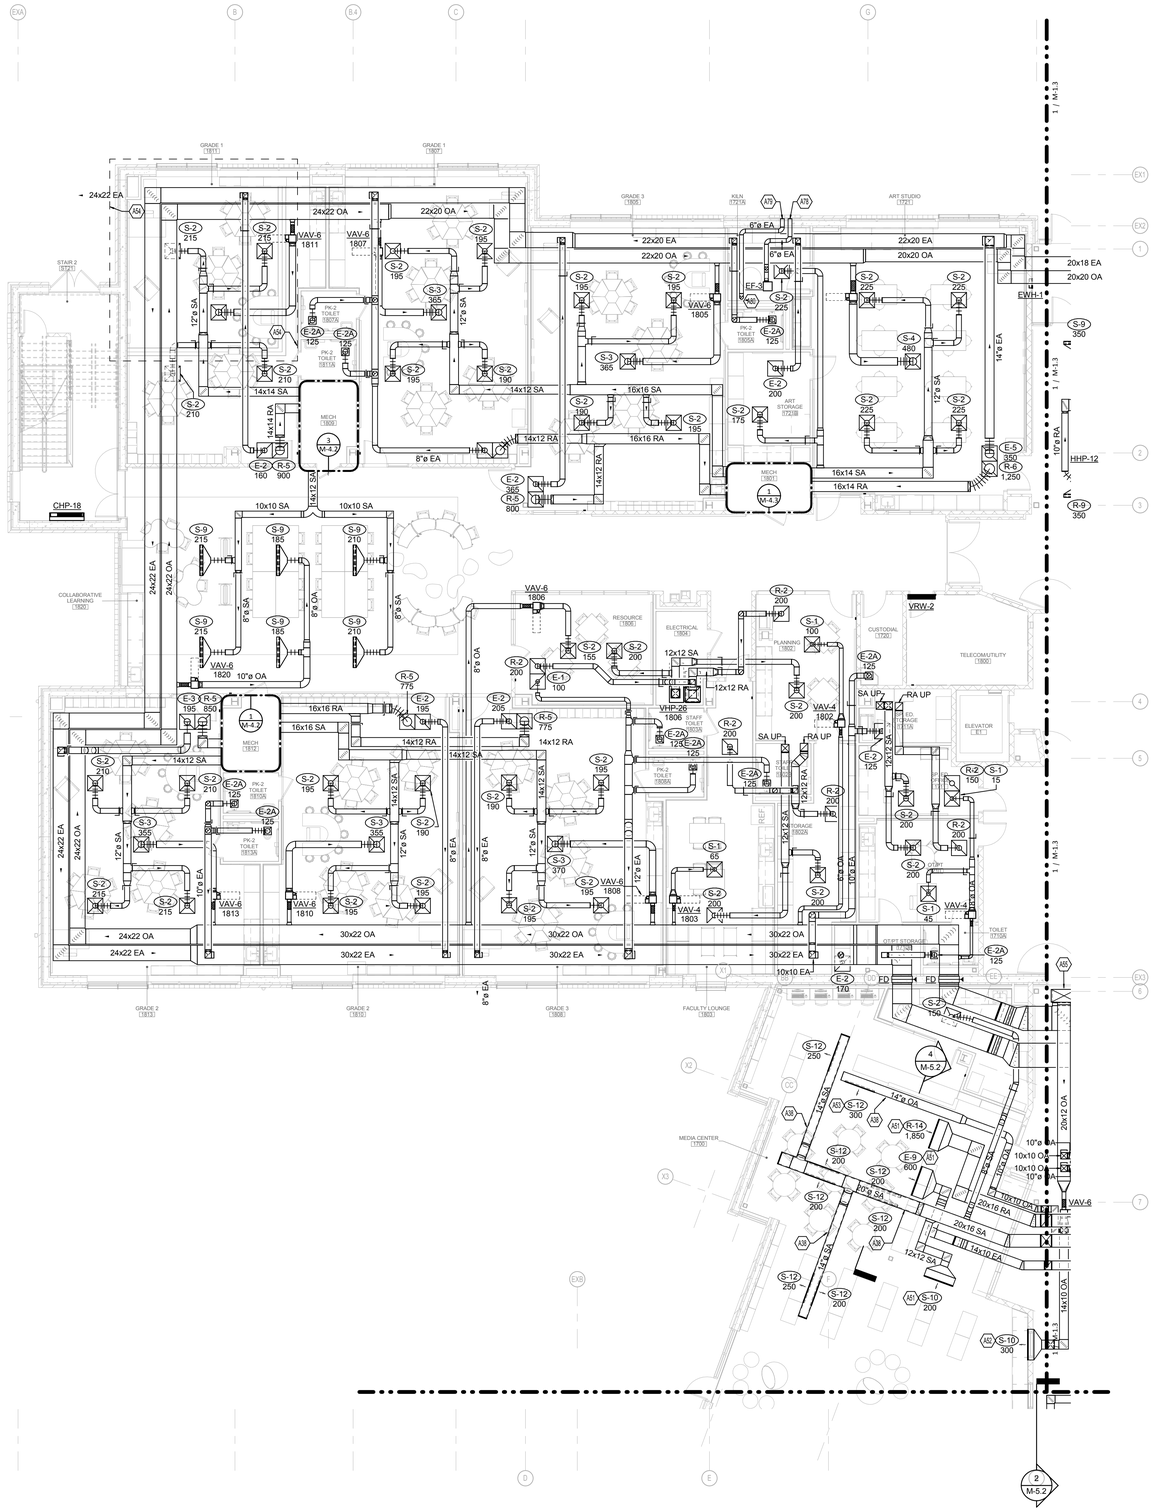

1 FIRST FLOOR - AREA B - AIR DISTRIBUTION

SCALE: 1/8" = 1'-0"

0' 2' 4' 8' 16' 24' 32'

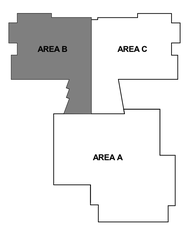

KEYPLAN

2429 Members Way
Lexington, Ky 40504
Tel: 859.253.0892
http://www.cmtaegis.com/

11720 Beltsville Drive
Suite 600
Calverton, MD 20705
Tel: 301.595.1000
www.grimmandparker.com

GP# 21553

AIR DISTRIBUTION - FIRST FLOOR AREA B

HOLABIRD ACADEMY PK-8
CITY OF BALTIMORE, MARYLAND

DATE	DESCRIPTION

M-1.2

03/13/2017
BID SET

© GRIMM AND PARKER, P.C. 2014