© GRIMM AND PARKER, P.C. 2014

TAGGED NOTES	
H17	2" CD TO SPILL TO STORM INLET GRATE. REFER TO SITE PLAN ON SHEET C2.00G FOR EXACT LOCATION. REFER TO SHEET UM1.0 FOR CONTINUATION.

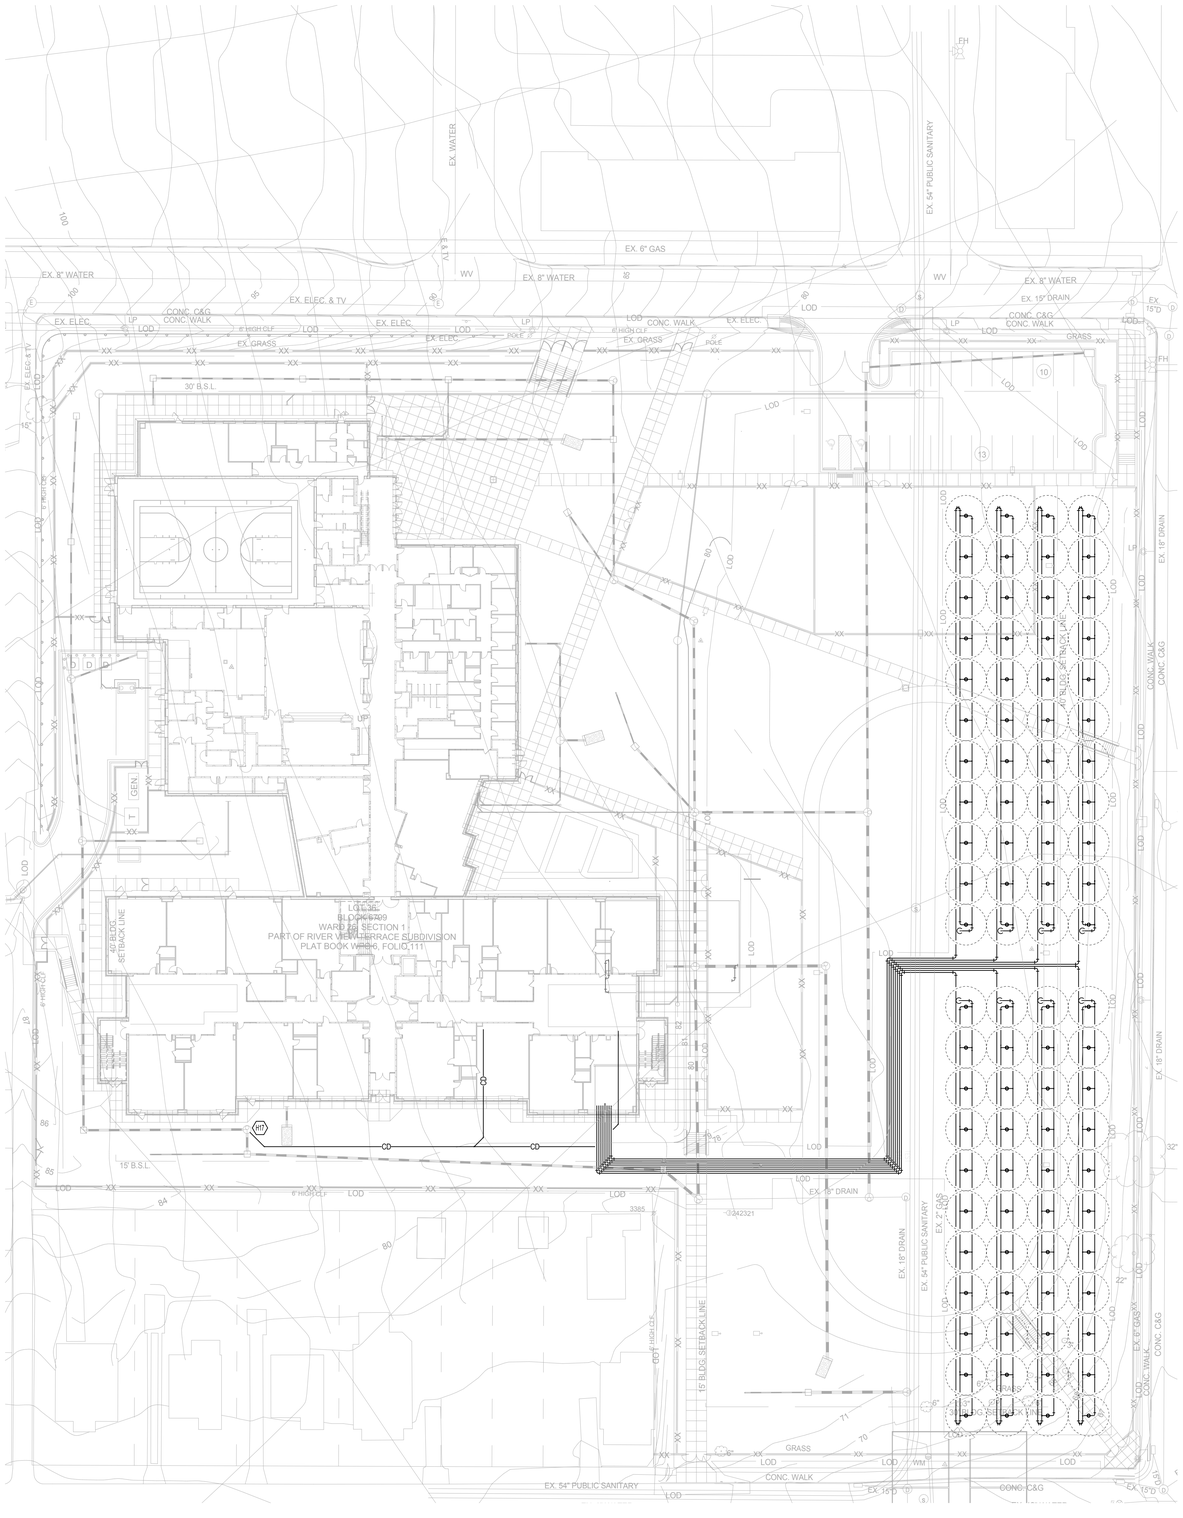

1 MECHANICAL SITE UTILITIES
SCALE: 1" = 30'-0"
0 15' 30' 60' 90' 120'

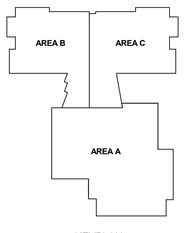

KEYPLAN

N

2429 Members Way
Lexington, Ky 40504
Tel: 859.253.0892
http://www.cmtaegis.com/

11720 Beltsville Drive
Suite 600
Calverton, MD 20705
Tel: 301.595.1000
www.grimmandparker.com

GRIMM AND PARKER

GP# 21553

MECHANICAL UTILITIES
HOLABIRD ACADEMY PK-8
CITY OF BALTIMORE, MARYLAND

DATE	DESCRIPTION

UM-1.0H
03/13/2017
BID SET

© GRIMM AND PARKER, P.C. 2014