© GRIMM AND PARKER, P.C. 2014

GENERAL AIR DISTRIBUTION NOTES	
A	REFER TO R,G,D RUNOUT SCHEDULE FOR R,G,D DUCT SIZE.
B	REFER TO TYPICAL BRANCH DUCT SUPPLY/OUTSIDE/RETURN/EXHAUST AIR DETAIL.
C	REFER TO TRANSFER AIR GRILLE DETAIL.
D	COORDINATE REGISTERS, GRILLES, AND DIFFUSERS WITH REFLECTED CEILING PLANS AND LIGHTING PLANS.
E	REFER TO CAV/VAV BOX DETAIL.
F	REFER TO AIR TERMINAL UNIT SCHEDULE FOR ALL RUNOUT SIZED OF VAV AND CAV BOXES.
G	REFER TO REFLECTED CEILING PLANS. PROVIDE 12"x12" ACCESS PANEL PREPARED FOR PAINTING AND PAINTED IN ACCORDANCE WITH ARCHITECTURAL REQUIREMENTS. PROVIDE ACCESS PANELS FOR DAMPERS WHERE INDICATED ABOVE GYPSUM CEILINGS IN AREAS SUCH AS RESTROOMS, LOCKER ROOMS, CUSTODIAL AREAS, ETC.

TAGGED NOTES	
A71	DUCT ROUTES UP AND BETWEEN STRUCTURE.

R, G, D RUNOUT SCHEDULE

MARK	BRANCH DUCT SIZE
E-1	6" DIA
E-1A	6" DIA
E-2	8" DIA
E-2A	10" DIA
E-3	10" DIA
E-4	12" DIA
E-5	14" DIA
E-7	SEE PLANS
E-9	SEE PLANS
E-10	48"x12"
R-1	6" DIA
R-2	8" DIA
R-3	10" DIA
R-4	12" DIA
R-5	14" DIA
R-6	16" DIA
R-7	SEE PLANS
R-8	12"x8"
R-9	SEE PLANS
R-10	SEE PLANS
R-11	18"x12"
R-13	SEE PLANS
R-14	SEE PLANS
S-1	6" DIA
S-1A	6" DIA
S-2	8" DIA
S-3	10" DIA
S-4	12" DIA
S-7	SEE PLANS
S-8	SEE PLANS
S-9	48"x5.25"
S-10	SEE PLANS
S-11	-
S-12	-
S-13	-
S-14	SEE PLANS
T-1	SEE PLANS

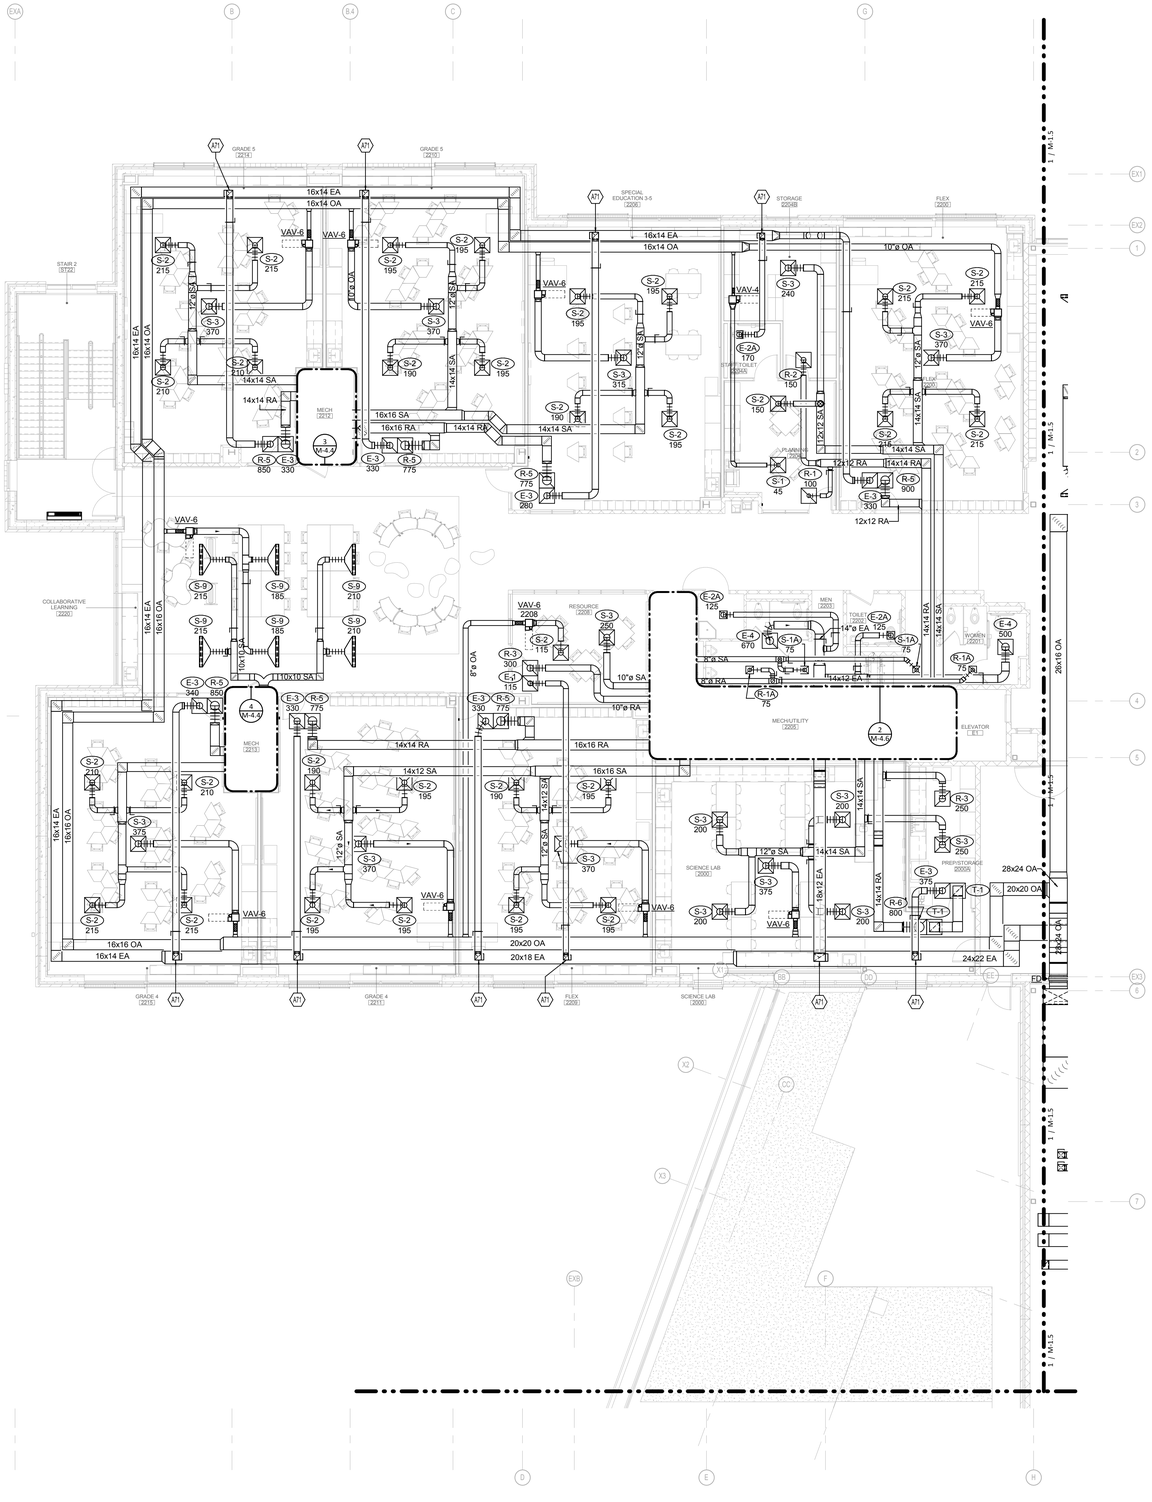

1 Second Floor - HVAC - Area B

SCALE: 1/8" = 1'-0"

0 2' 4' 8' 16' 24' 32'

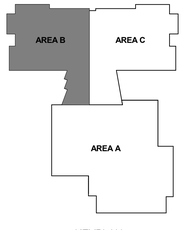

KEYPLAN

2429 Members Way
Lexington, Ky 40504
Tel: 859.253.0892
http://www.cmtaegs.com/

11720 Baltisville Drive
Suite 600
Calverton, MD 20705
Tel: 301.595.1000
www.grimmandparker.com

GRIMM AND PARKER

GP# 21553

AIR DISTRIBUTION - SECOND FLOOR AREA B

HOLABIRD ACADEMY PK-8
CITY OF BALTIMORE, MARYLAND

DATE	DESCRIPTION

M-1.4

03/13/2017
BID SET

© GRIMM AND PARKER, P.C. 2014