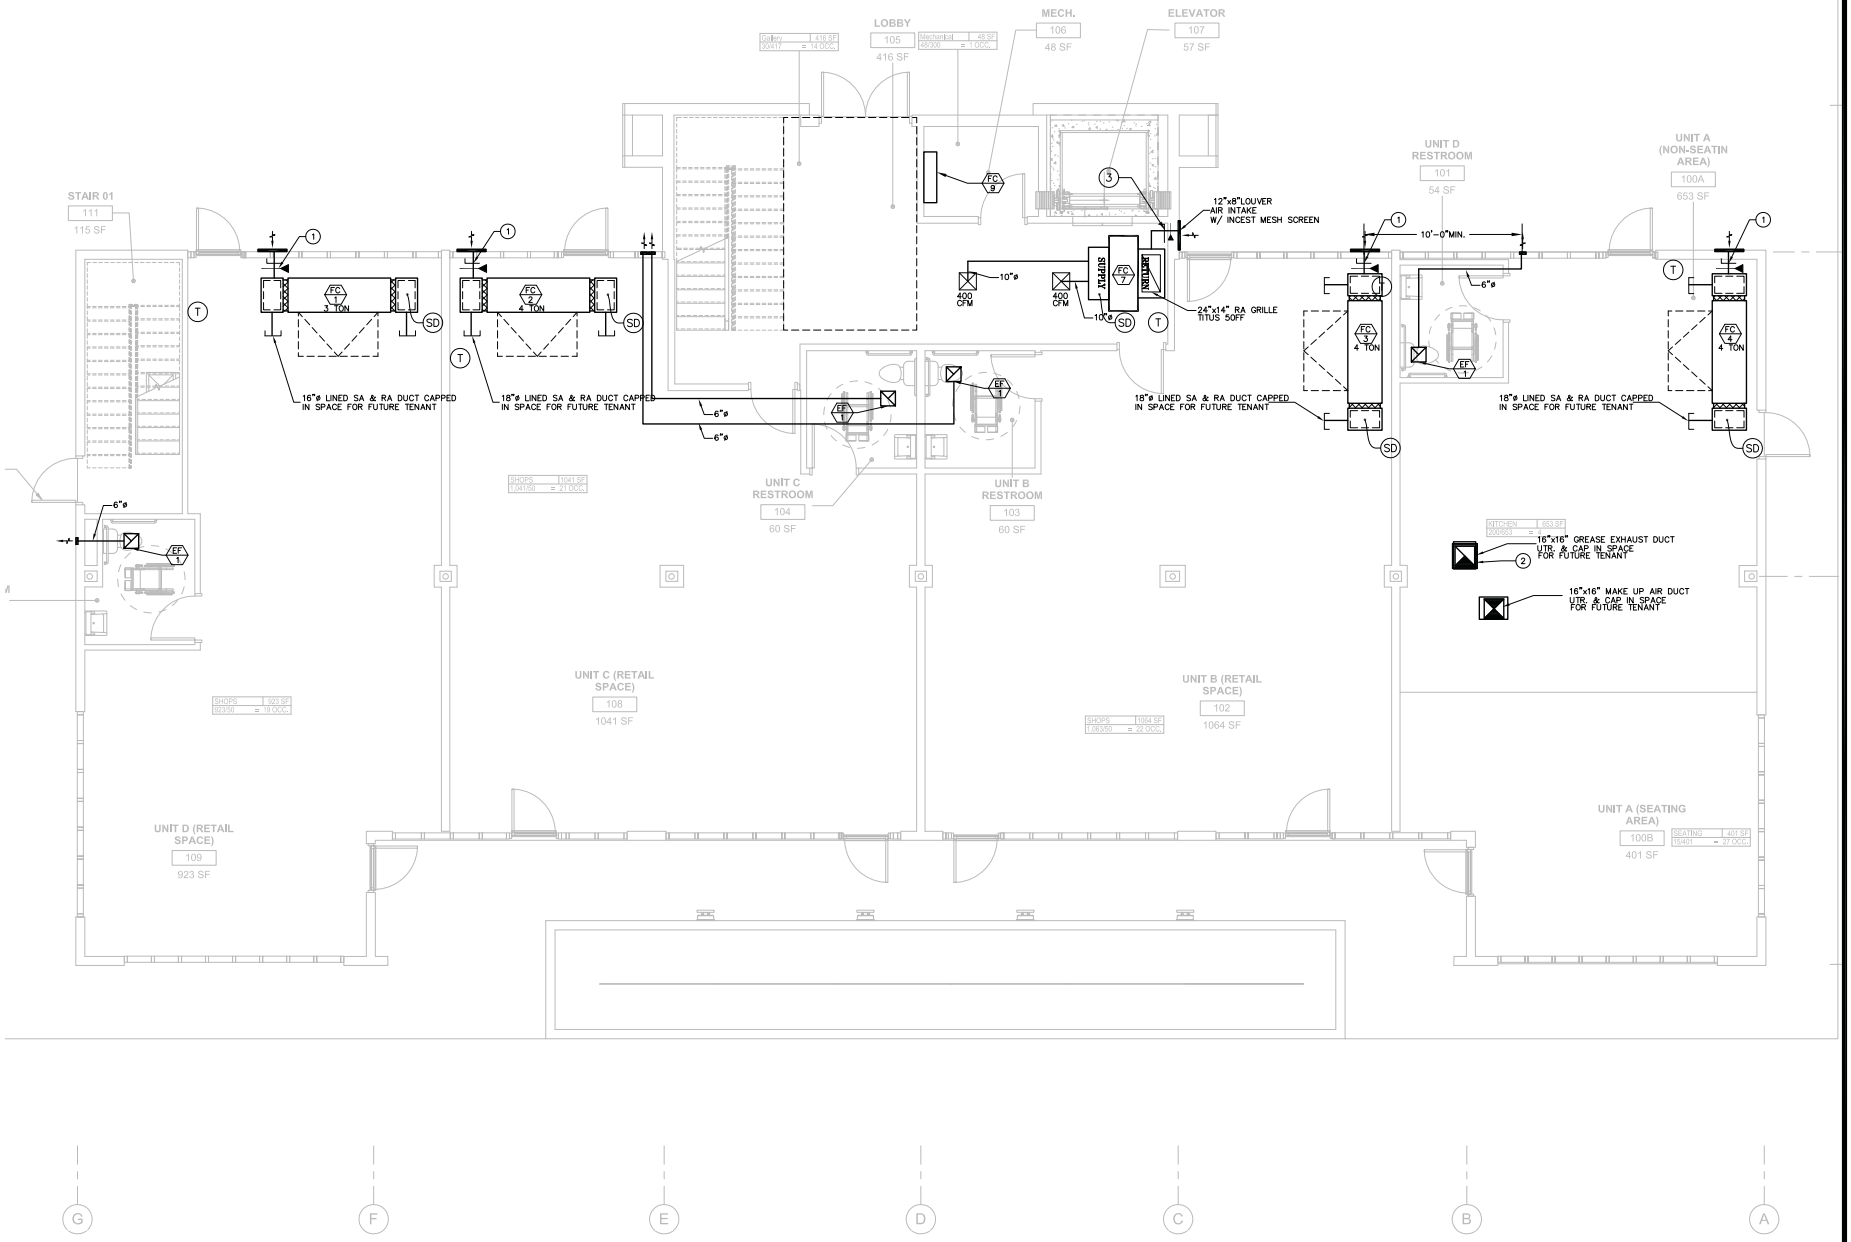

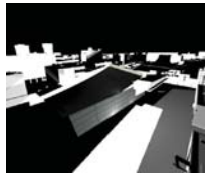

Stitch Studio

Contact: Jorge Escamilla
4082 Pomona Street
Ventura, California 93003
Direct: 818.523.7201
Email: stitchstudio3d@gmail.com

A & N DESIGN GROUP
MECHANICAL · PLUMBING · ELECTRICAL
19126 HAYNES STREET #2
RESEDA, CA 91335
TEL: (818)-288-4361
FAX: (818)-758-0087

REGISTERED PROFESSIONAL ENGINEER
ARASH NOORI
No. M-34638
EXP. 12-31-17
MECHANICAL
STATE OF CALIFORNIA

No.	Description	Date

PRAJIN DEVELOPMENT

NEW BUILDING
PRAJIN BROTHERS, LLC
5707 PACIFIC BLVD.
HUNTINGTON PARK, CA 90255

FIRST FLOOR PLAN

Project number	Project Number
Date	02-23-17
Drawn by	A.N.
Checked by	A.N.

M201

Scale	1/4" = 1'-0"

8/6/2015 8:44:07 PM