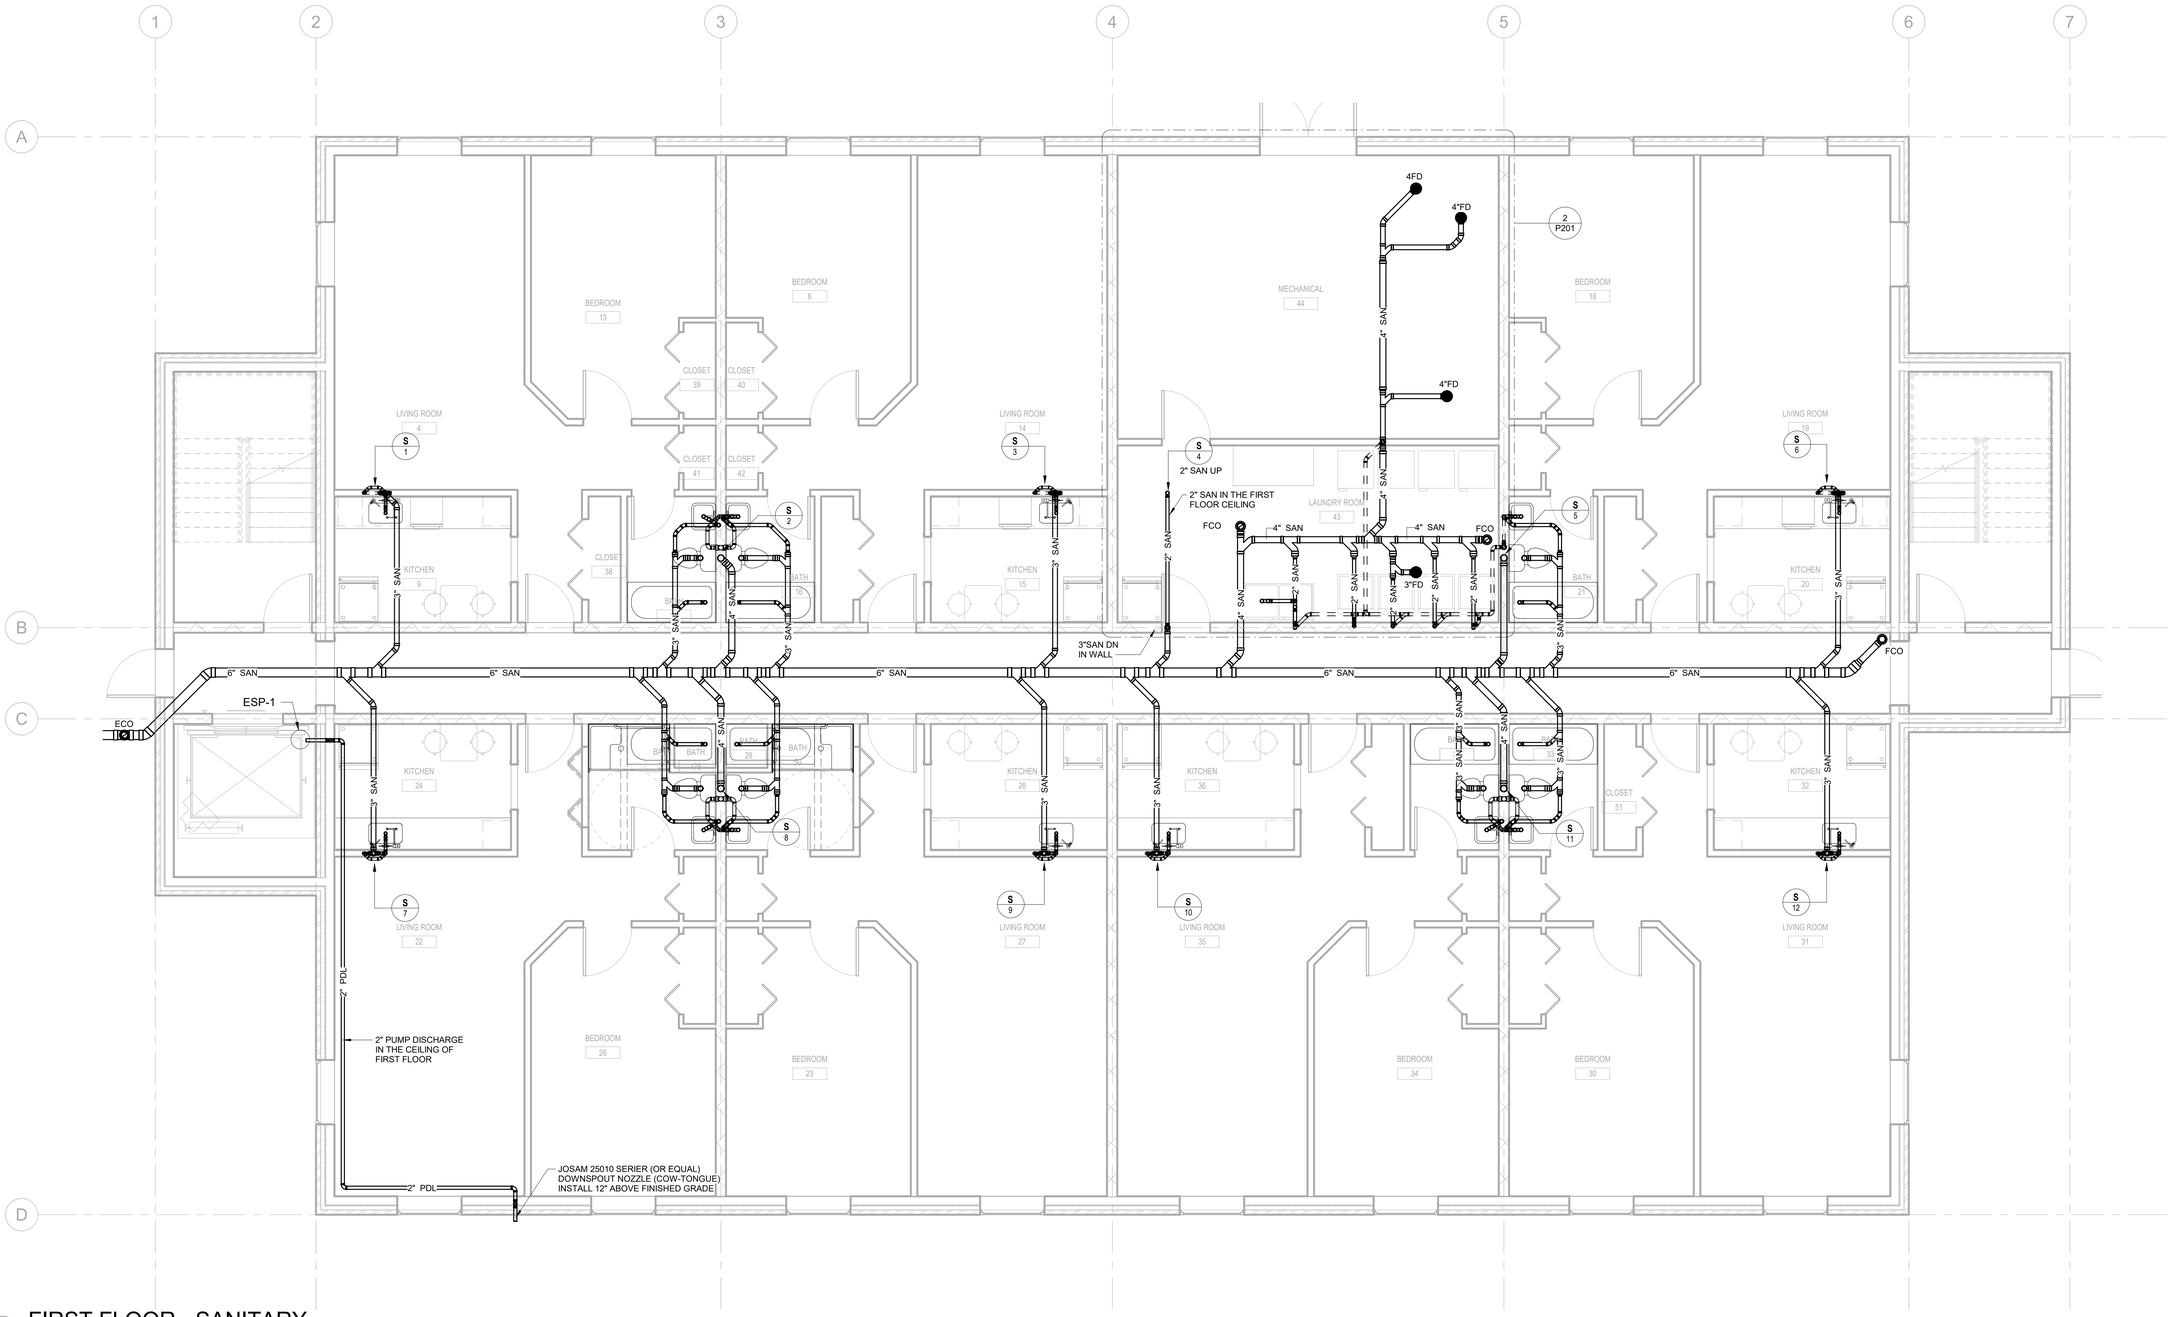

1 FIRST FLOOR - SANITARY

1/4" = 1'-0"

REVISION	DESCRIPTION	BY	DATE

ARCHITECT

MEP. ENG.

NIST

FOR OFFICIAL USE ONLY

U.S. DEPARTMENT OF COMMERCE

OFFICE OF FACILITIES & PROPERTY MANAGEMENT

NIST – MID RISE APARTMENT

PLUMBING FIRST FLOOR PLAN – SANITARY

P111

APPROVED BY	DATE	SPONSOR	DATE	MAINTENANCE ENG. OFF.	DATE	ENVIRONMENTAL MANAGEMENT	DATE	SAFETY	DATE	SHED – NIST FIRE MARSHAL/AHJ	DATE	FACILITIES ENGR. OFF.	DATE	PROJECT LEADER: VAY	DATE	DRAWN BY: AA	DATE: 08/15/2022	PROJECT/ W.O. #: Project Number

SH. NO. ___ OF ___ DWG. P111