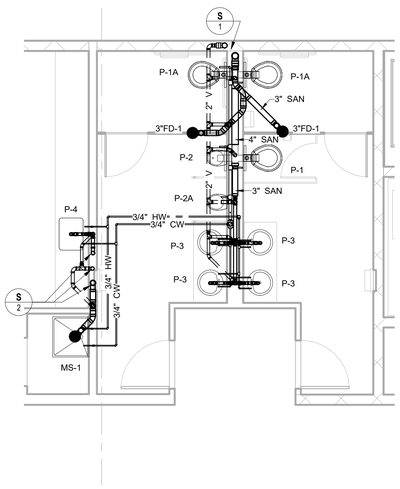

2 2ND FLR - REST ROOM ENLARGED PLAN
1/4" = 1'-0"

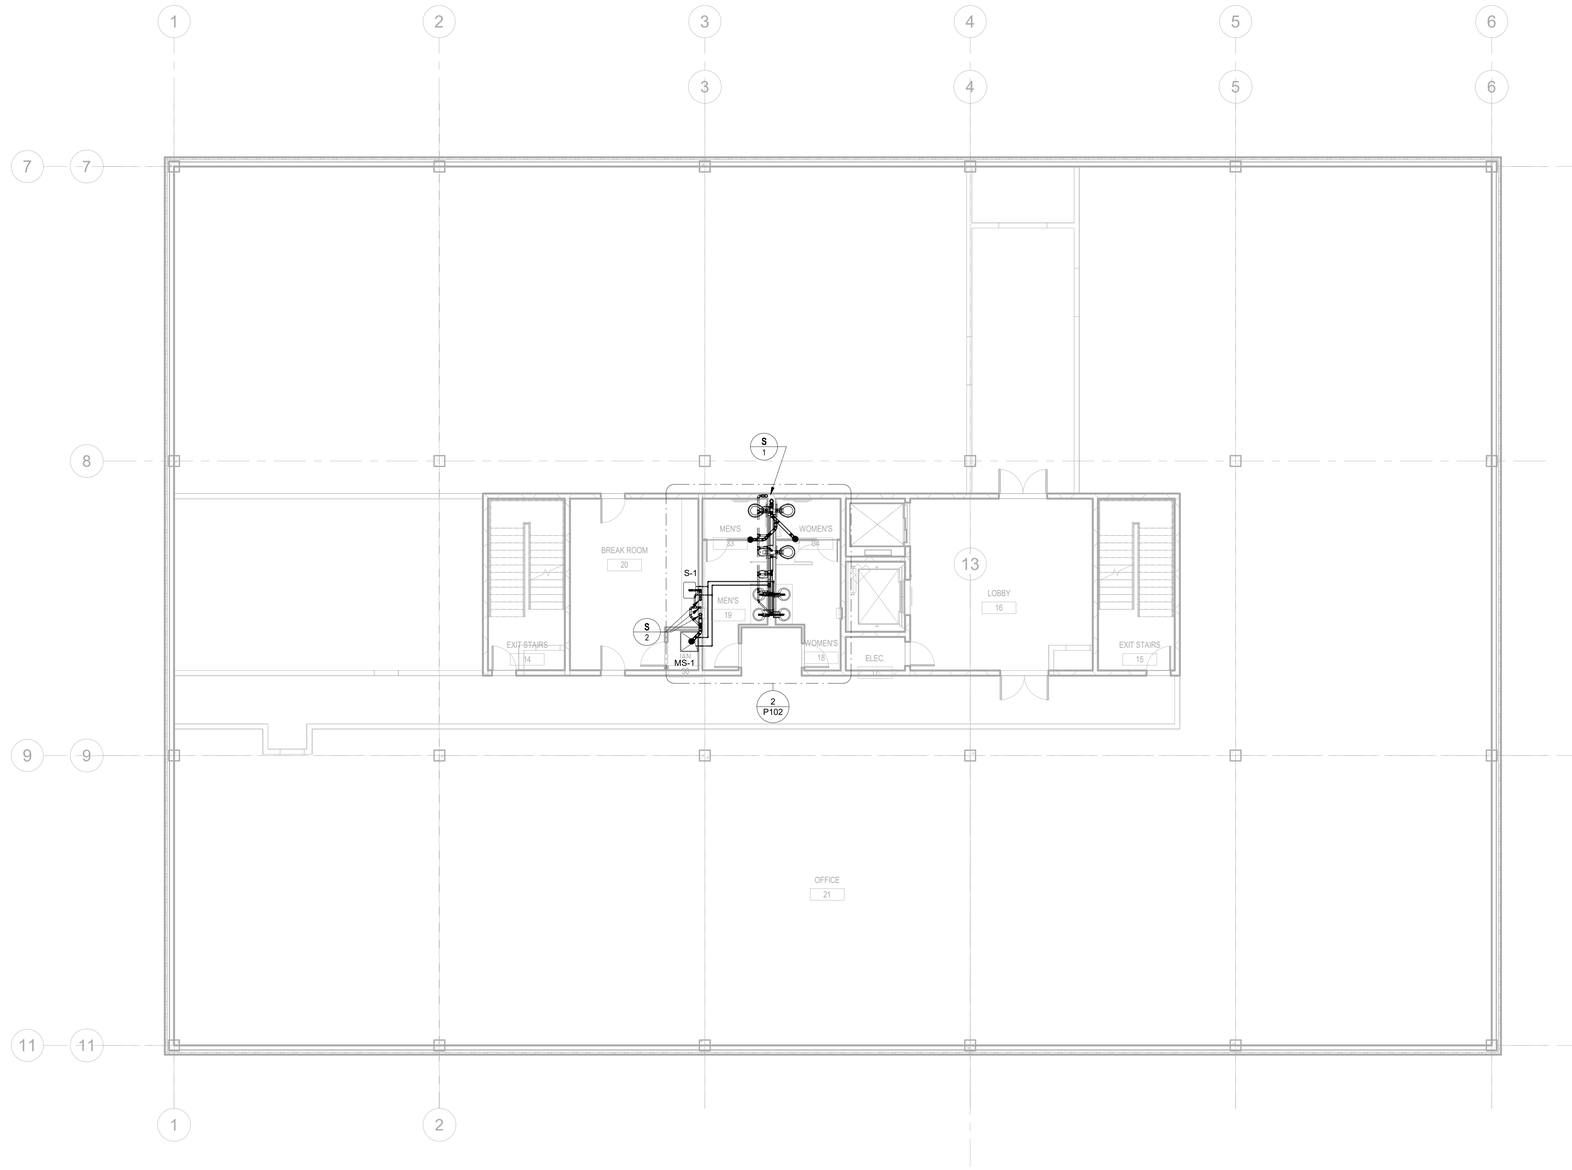

1 SECOND FLOOR - SANITARY, WATER & GAS
1/8" = 1'-0"

REVISION	DESCRIPTION	BY	DATE

GENERAL NOTES

1. REFER TO P001 FOR GENERAL NOTES, SYMBOL LEGEND AND LIST OF ABBREVIATIONS.

ARCHITECT

MEP. ENG.

NIST

FOR OFFICIAL USE ONLY

U.S. DEPARTMENT OF COMMERCE

OFFICE OF FACILITIES & PROPERTY MANAGEMENT

NIST – MEDIUM OFFICE

PLUMBING SECOND FLOOR PLAN

P102

SH. NO.___OF___ DWG. P102

APPROVED BY	DATE	SPONSOR	DATE	MAINTENANCE ENG. OFF.	DATE	ENVIRONMENTAL MANAGEMENT	DATE	SAFETY	DATE	SHED – NIST FIRE MARSHAL/AHJ	DATE	FACILITIES ENGR. OFF.	DATE	PROJECT LEADER	DATE	DRAWN BY	DATE	PROJECT/ W.O. #
														VAY		AA	08/15/2022	Project Number