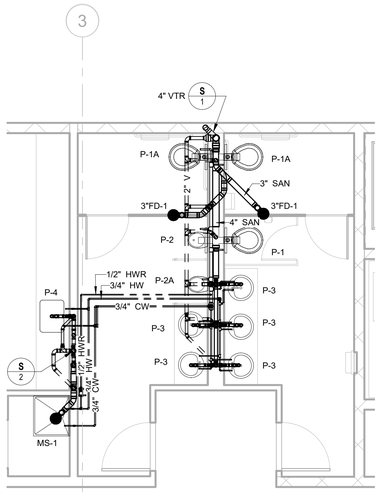

2 THIRD FLOOR - REST ROOM ENLARGED PLAN
1/4" = 1'-0"

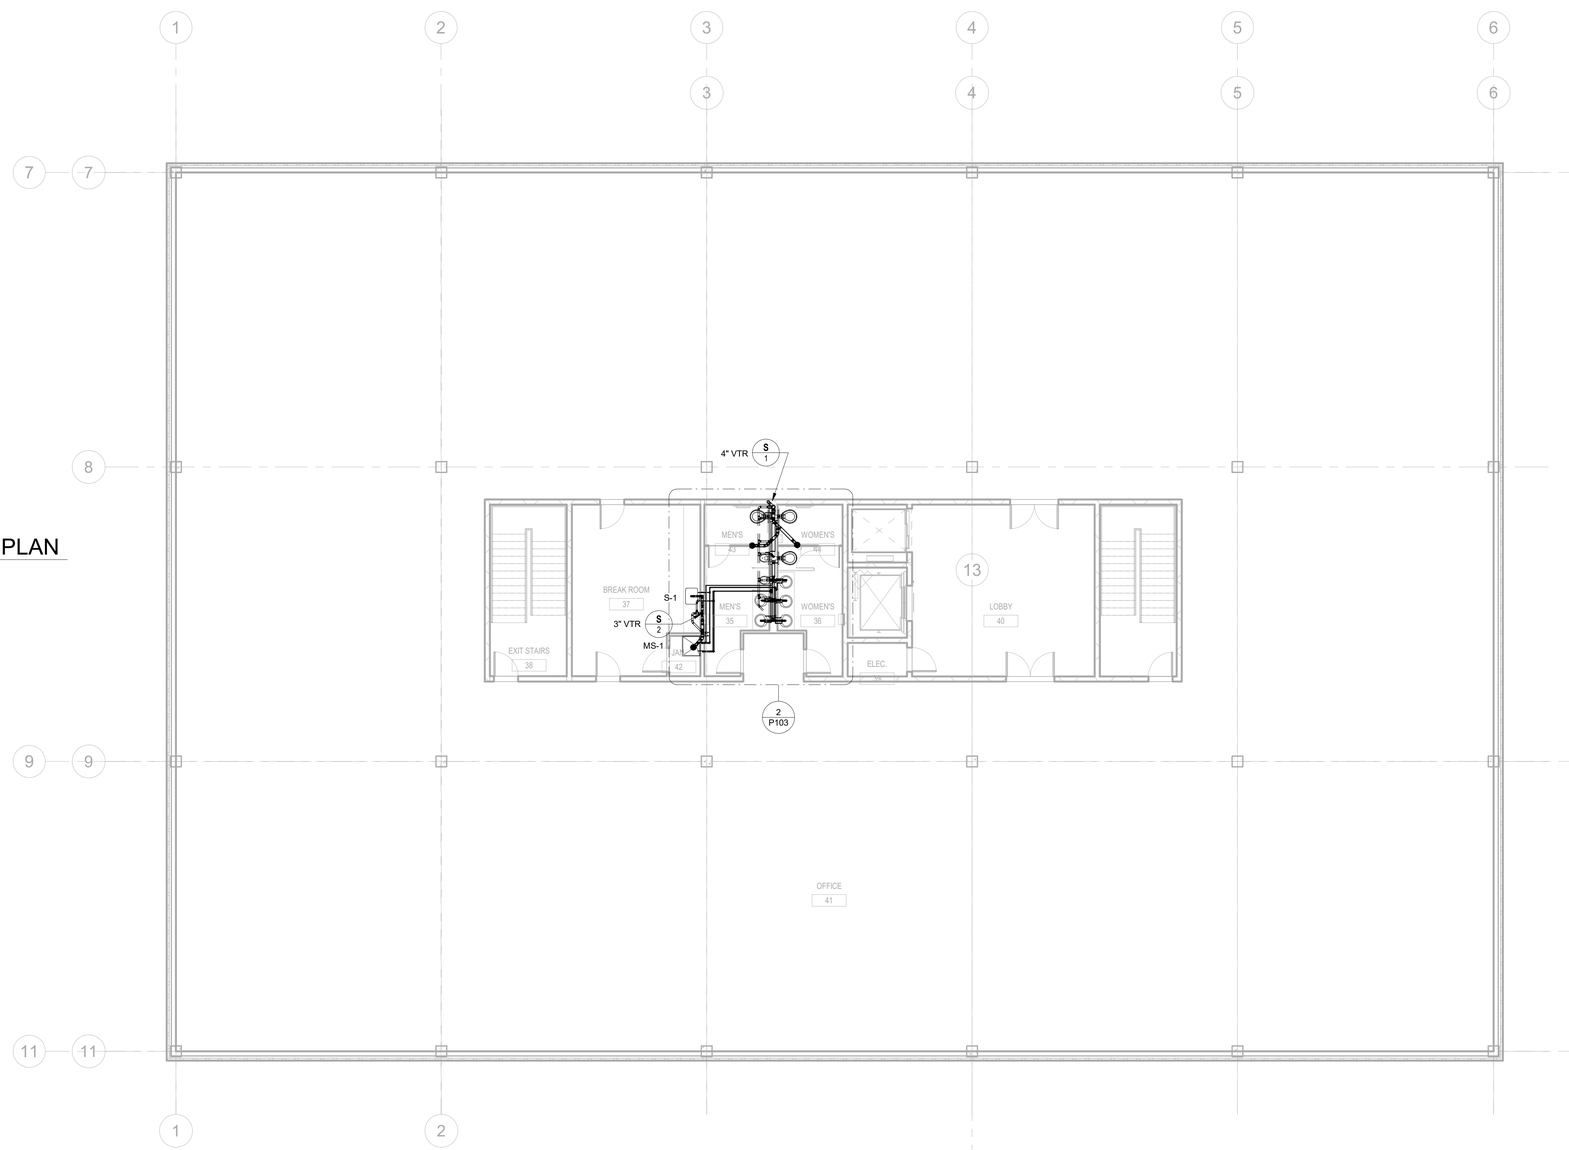

1 THIRD FLOOR - SANITARY, WATER & GAS
1/8" = 1'-0"

REVISION	DESCRIPTION	BY	DATE

GENERAL NOTES

1. REFER TO P001 FOR GENERAL NOTES, SYMBOL LEGEND AND LIST OF ABBREVIATIONS.

ARCHITECT

MEP. ENG.

NIST

FOR OFFICIAL USE ONLY

U.S. DEPARTMENT OF COMMERCE

OFFICE OF FACILITIES & PROPERTY MANAGEMENT

NIST – MEDIUM OFFICE

PLUMBING THIRD FLOOR PLAN

P103

APPROVED BY	DATE	SPONSOR	DATE	MAINTENANCE ENG. OFF.	DATE	ENVIRONMENTAL MANAGEMENT	DATE	SAFETY	DATE	SHED – NIST FIRE MARSHAL/AHJ	DATE	FACILITIES ENGR. OFF.	DATE	PROJECT LEADER: VAY	DATE	DRAWN BY: AA	DATE: 08/15/2022	Project Number / PROJECT/ W.O. #

SH. NO. ___ OF ___ DWG. P103