PRODUCED BY AN AUTODESK STUDENT VERSION

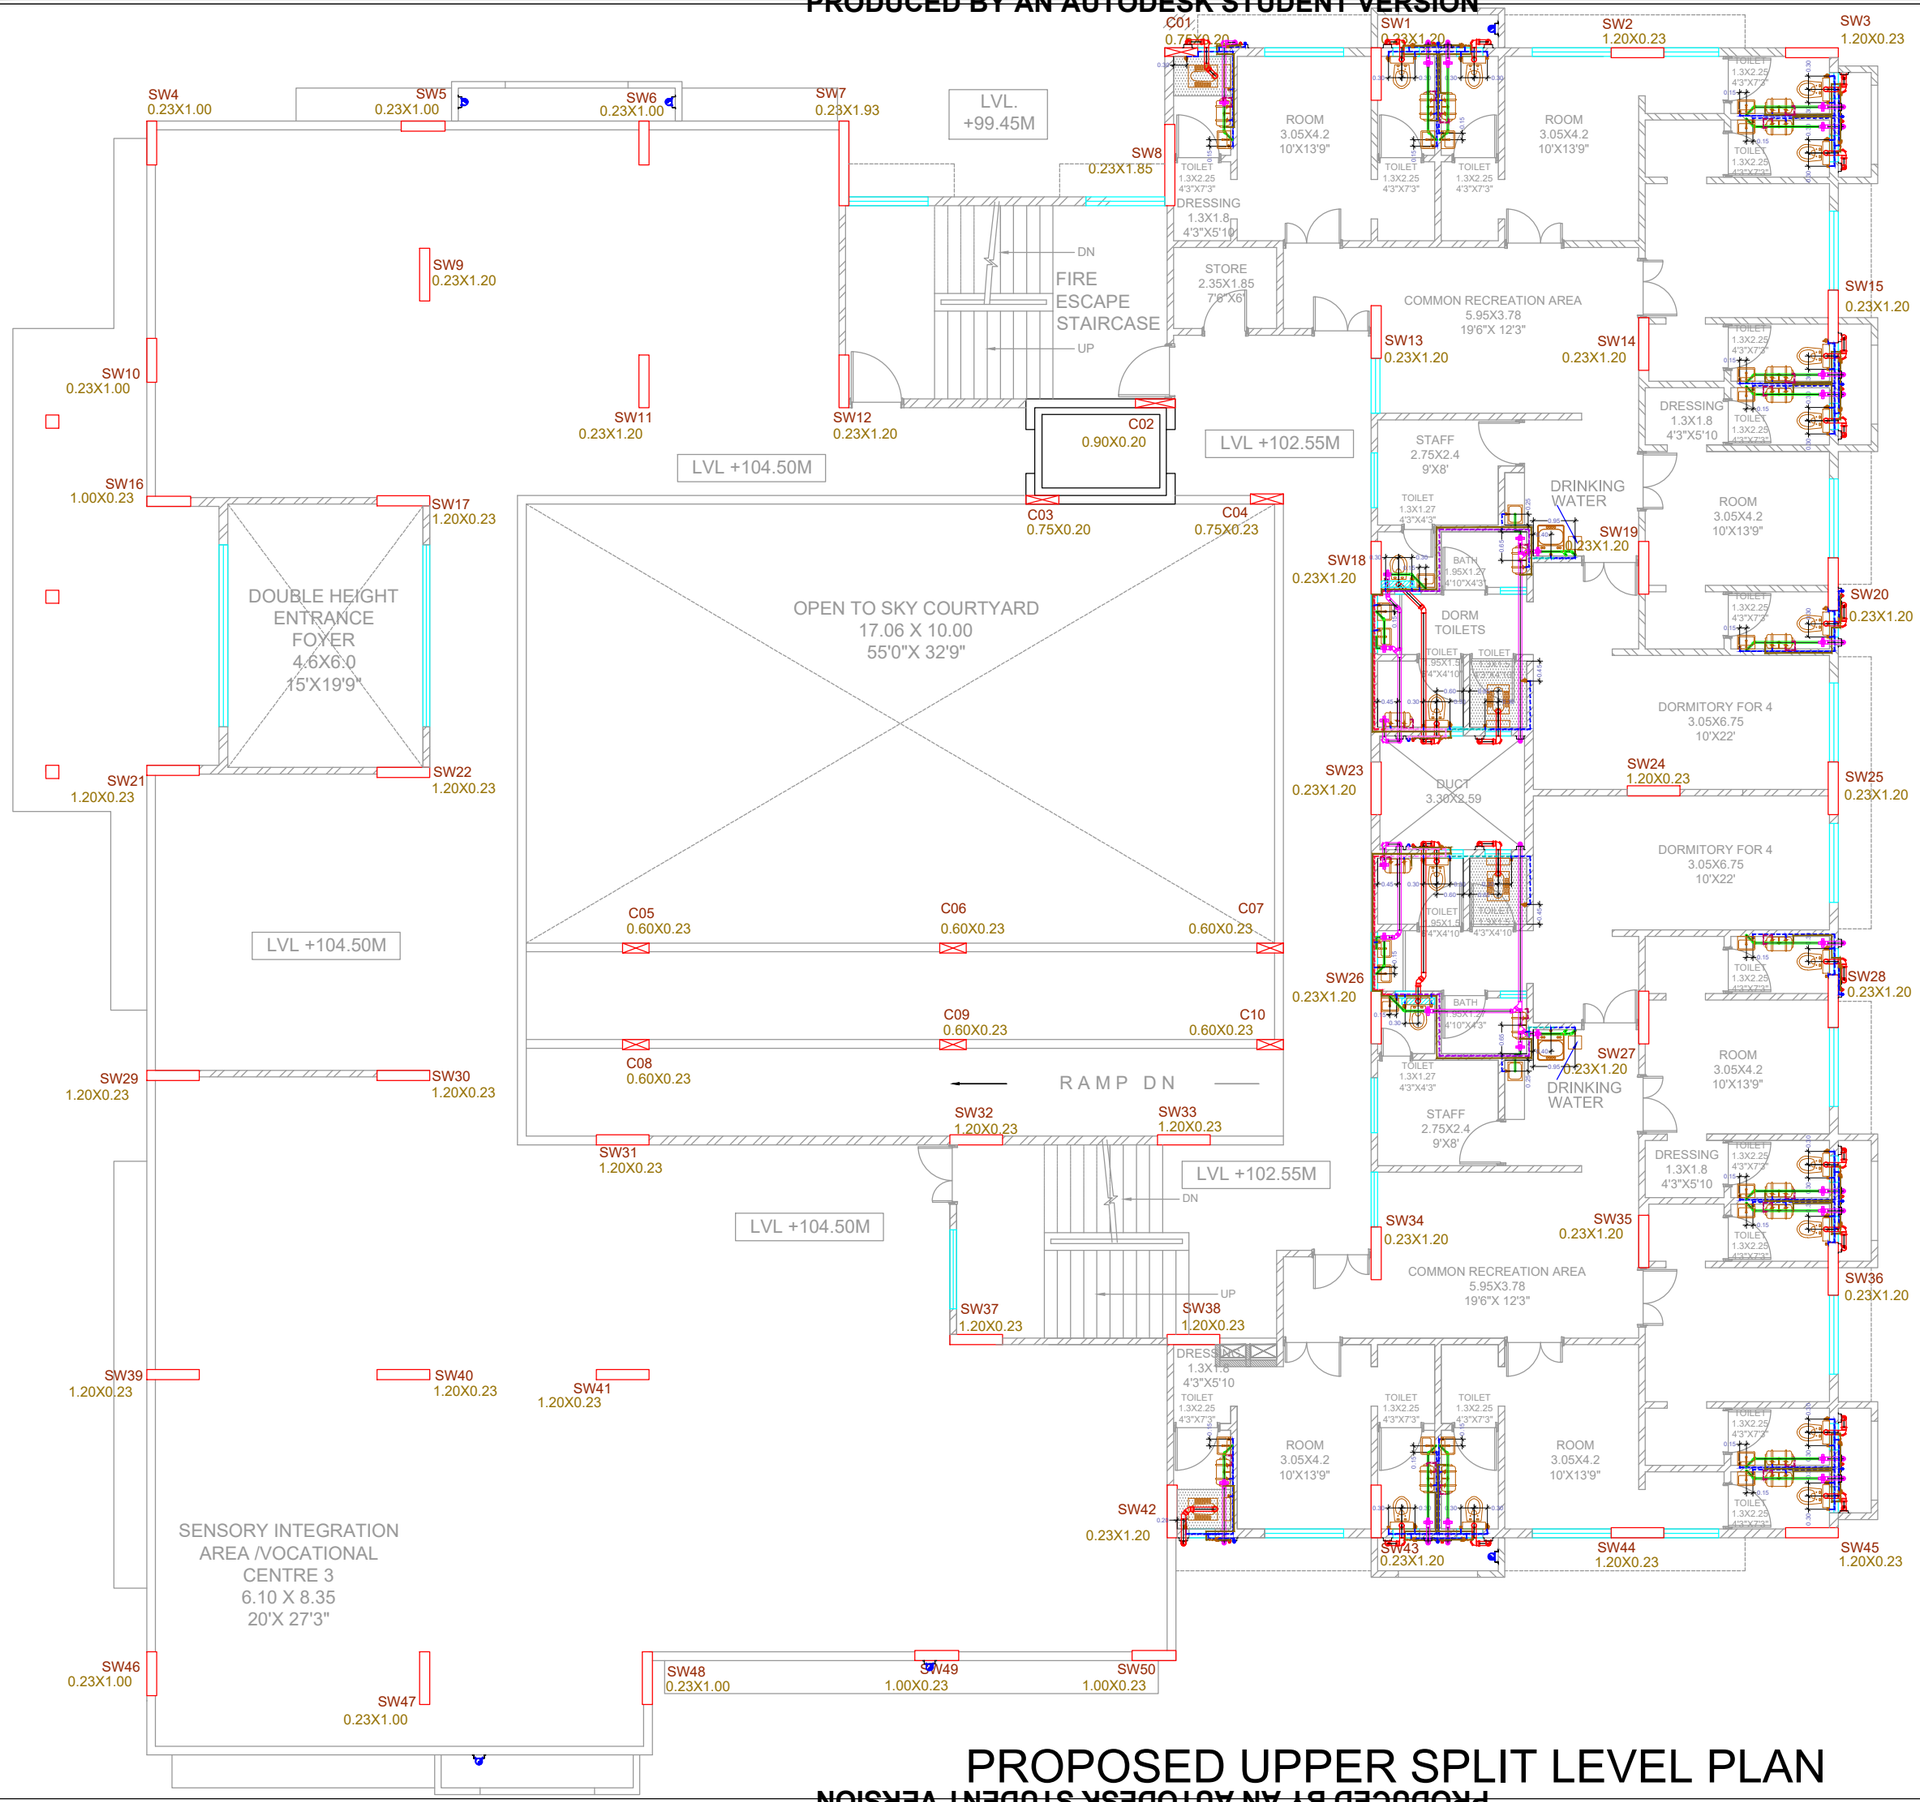

PROPOSED UPPER SPLIT LEVEL PLAN

PRODUCED BY AN AUTODESK STUDENT VERSION

DRG NO.	M/167/04 R5	03/03

STAMP & SIGNATURE

McLIN Consultants Pvt. Ltd. ADVANCE COPY Pune-30

NOTES:

	SOIL PIPE (SWR 'B' TYPE) Ø 110 mm
	WASTE PIPE (SWR 'B' TYPE) Ø 75 mm
	WASTE PIPE (SWR 'B' TYPE) Ø 50 mm
	WASTE PIPE (SWR 'B' TYPE) Ø 40 mm
CWS	CPVC SDR 11 DOMESTIC WATER LINE Ø 40 mm
CWS	CPVC SDR 11 DOMESTIC WATER LINE Ø 32 mm
CWS	CPVC SDR 11 DOMESTIC WATER LINE Ø 25 mm
CWS	CPVC SDR 11 DOMESTIC WATER LINE Ø 20 mm
CWS	CPVC SDR 11 DOMESTIC WATER LINE Ø 15 mm
HW	CPVC SDR 11 HOT WATER LINE Ø 15 mm
	KiTEC COMPOSITE SOLAR HOT WATER LINE Ø 12-16 MM
	MULTI FLOOR TRAP
	SHOWER WITH MIXER
	BIB COCK WITH HEALTH FAUCET
	ANGULAR STOP COCK
	BALL VALVE
	NON RETURN VALVE
	BOILER
	WALL MOUNTED EWC WITH FLUSH TANK
	WASH BASIN
	URINAL
	LEDGE WALL

REV NOS	DATE	REMARK / SUBJECT
R5	02.04.21	REVISED ARCH. PLAN
R4	28.12.19	REVISED ARCH. PLAN
R3	27.11.19	REVISED ARCH. PLAN
R2	19.11.19	REVISED ARCH. PLAN
R1	03.10.19	EWC LOCATION CHANGE

REVISIONS

DRAWING TITLE	UPPER SPLIT LEVEL PLUMBING DETAILS FLOOR PLAN
PROJECT	ARC AUTISM RESEARCH & TRAINING CENTER

McLIN CONSULTANTS PVT.LTD.
CONSULTANCY IN PLUMBING AND ENVIRONMENTAL ENGINEERING
'GIRIJA' 5, Sitabaug Colony, Vithalwadi Road,
Pune - 411 030 Tel - 2432 0010
e-mail - mclincpl@gmail.com

CLIENT	MR. SUBHASH LELE	
ARCHITECT	INDESIGN ARCHITECTS	
NORTH	DATE:-	01.10.2019
	DRAWN BY	PANKAJ G.
	CHECKED BY	MOHANISH P.
	APPROVED BY	MOHANISH P.
SCALE:-NTS		

C:\Users\Dell\Downloads\ARC Plumbing Drawings (1)\ARC Plumbing Drawings\R5 Toilet Details 02.04.21.dwg

PRODUCED BY AN AUTODESK STUDENT VERSION