PRODUCED BY AN AUTODESK STUDENT VERSION

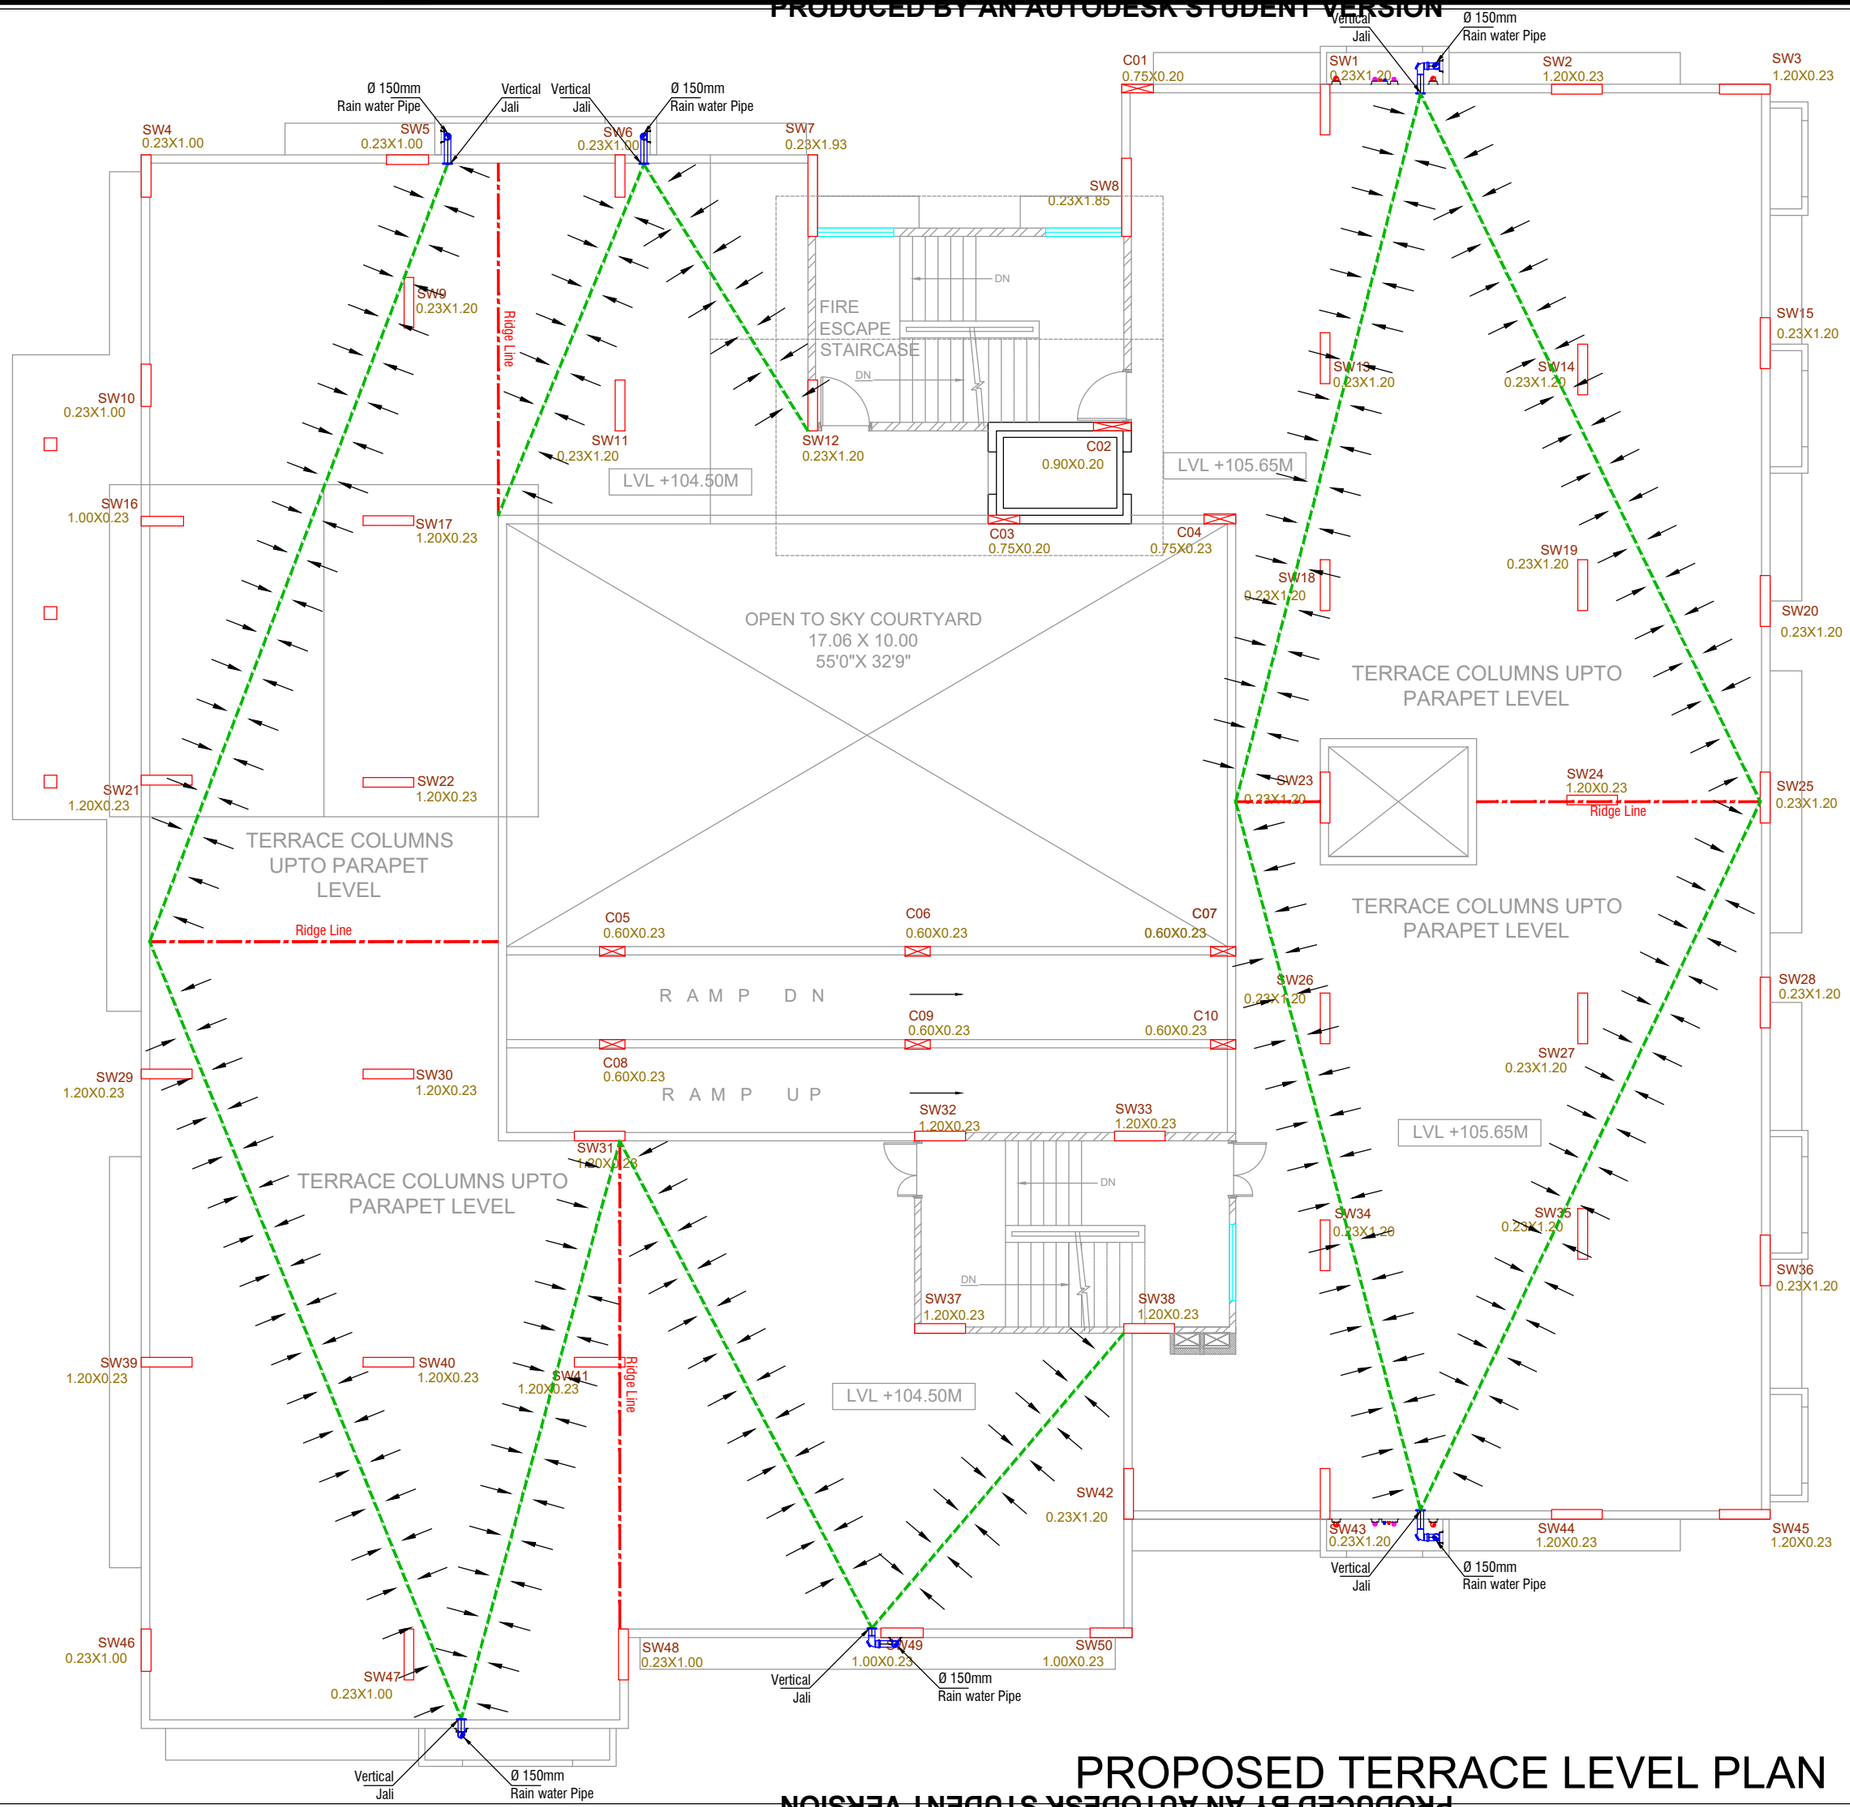

PROPOSED TERRACE LEVEL PLAN

DRG NO.	M/167/05	01/01
	R5	

STAMP & SIGNATURE

McLIN Consultants Pvt. Ltd. ADVANCE COPY Pune-30

NOTES:

	RAIN WATER PIPE (SWR 'A' TYPE) Ø150MM
	VERTICAL JALI
	VALLEY LINE
	RIDGE LINE

REV NOS	DATE	REMARK / SUBJECT
R5	02.04.21	REVISED ARCH. PLAN
R4	28.12.19	REVISED ARCH. PLAN
R3	27.11.19	REVISED ARCH. PLAN
R2	19.11.19	REVISED ARCH. PLAN
R1	03.10.19	EWC LOCATION CHANGE

REVISIONS

DRAWING TITLE	TERRACE LEVEL RAIN WATER PIPE DETAILS FLOOR PLAN
PROJECT	ARC AUTISM RESEARCH & TRAINING CENTER

McLIN CONSULTANTS PVT.LTD.
CONSULTANCY IN PLUMBING AND ENVIRONMENTAL ENGINEERING
'GIRIJA' 5, Sitabaug Colony, Vithalwadi Road,
Pune - 411 030 Tel - 2432 0010
e-mail - mclincpl@gmail.com

CLIENT	MR. SUBHASH LELE	
ARCHITECT	INDESIGN ARCHITECTS	
NORTH	DATE:-	01.10.2019
	DRAWN BY	PANKAJ G.
	CHECKED BY	MOHANISH P.
SCALE:-NTS	APPROVED BY	MOHANISH P.

C:\Users\Dell\Downloads\ARC Plumbing Drawings (1)\ARC Plumbing Drawings\R5 Toilet Details 02.04.21.dwg

PRODUCED BY AN AUTODESK STUDENT VERSION