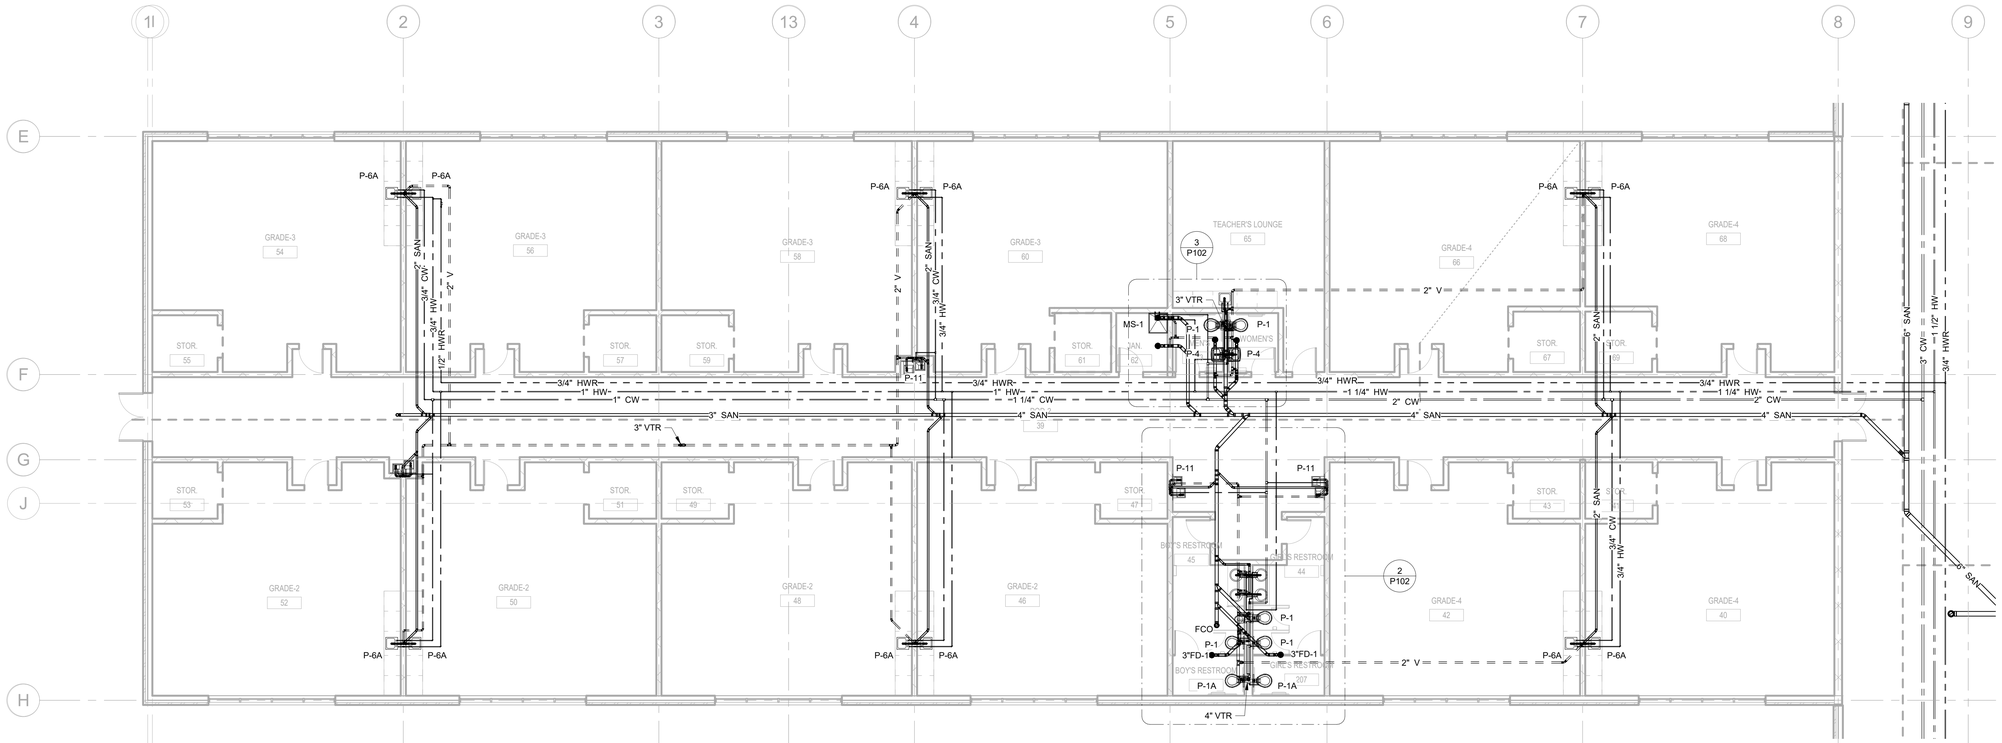

1 FIRST FLOOR - SANITARY - WATER & GAS - AREA B
1/8" = 1'-0"

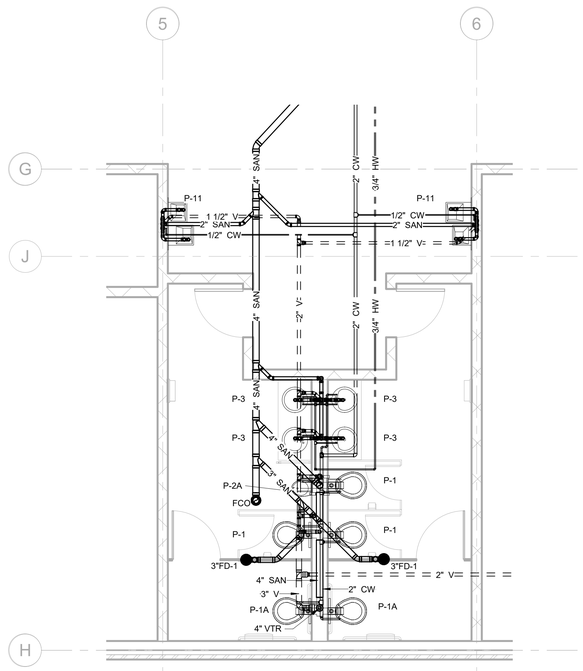

2 FIRST FLOOR - AREA B - BOYS & GIRLS RESTROOM
1/4" = 1'-0"

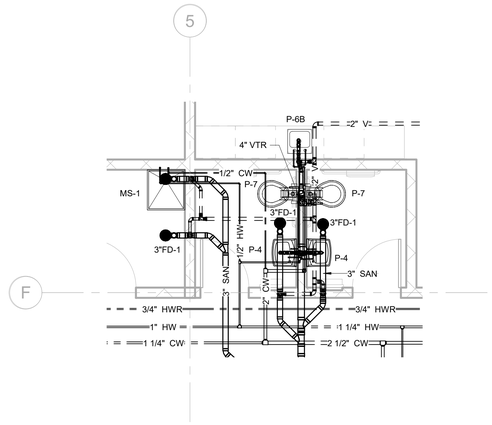

3 FIRST FLOOR - AREA B - MEN'S & WOMEN'S RESTROOM
1/4" = 1'-0"

REVISION	DESCRIPTION	BY	DATE

GENERAL NOTES

1. REFER TO P001 FOR GENERAL NOTES, SYMBOL LEGEND AND LIST OF ABBREVIATIONS.

ARCHITECT

MEP. ENG.

NIST

FOR OFFICIAL USE ONLY

U.S. DEPARTMENT OF COMMERCE

OFFICE OF FACILITIES & PROPERTY MANAGEMENT

NIST – PRIMARY SCHOOL

PLUMBING FLOOR PLAN – AREA B

P102

SH. NO. ___ OF ___ DWG. P102

APPROVED BY	DATE	SPONSOR	DATE	MAINTENANCE ENG. OFF.	DATE	ENVIRONMENTAL MANAGEMENT	DATE	SAFETY	DATE	SHED – NIST FIRE MARSHAL/AHJ	DATE	FACILITIES ENGR. OFF.	DATE	PROJECT LEADER	DATE	DRAWN BY	DATE	PROJECT/ W.O. #
														VAY		AA	08/15/2022	Project Number