© GRIMM AND PARKER, P.C. 2014

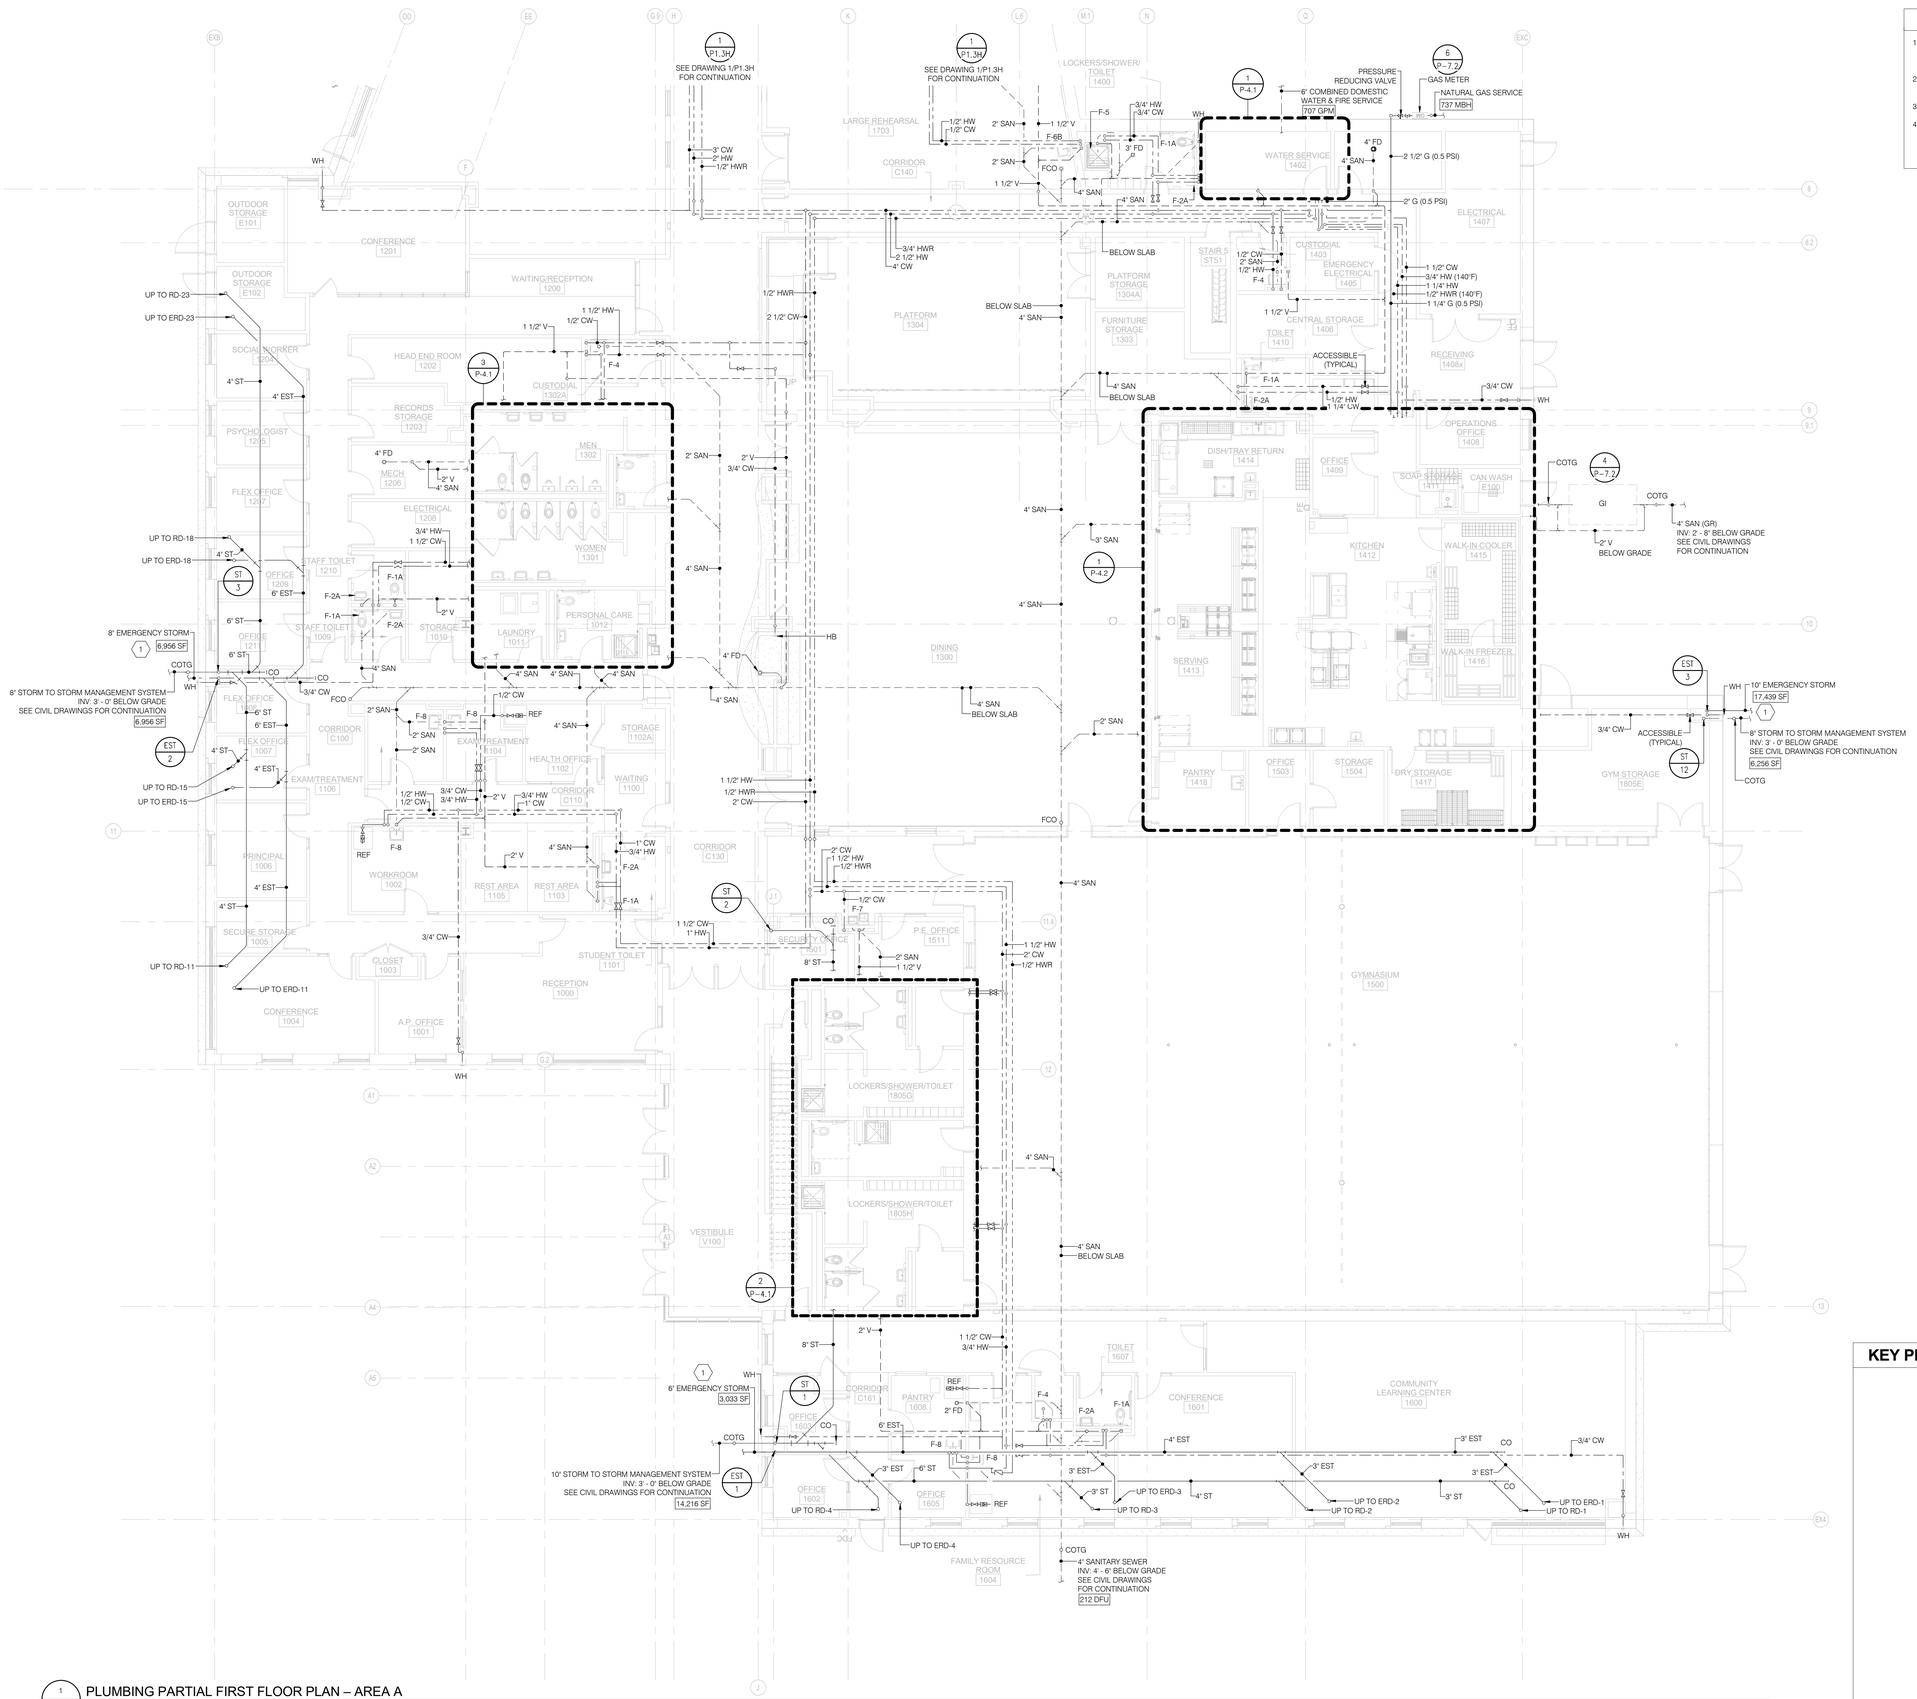

SHEET KEY NOTES

1. EMERGENCY STORM DRAIN DISCHARGE TO GRADE PIPE 18"-24" ABOVE FINISHED GRADE. PROVIDE DISCHARGE NOZZLE WITH SCREEN. COORDINATE WITH CIVIL PLANS FOR GRADE ELEVATION.
2. PROVIDE TRAP PRIMING TO ALL FLOOR DRAINS, FLOOR SINKS AND OPEN SITE DRAINS.
3. PROVIDE ACCESS PANELS TO ALL DOMESTIC SUPPLY VALVES.
4. PROVIDE ACCESS PANELS TO ALL WATER HAMMER ARERESTORS. REFER TO PLUMBING RISER DIAGRAM FOR WATER HAMMER ARRESTOR LOCATION.

1 P-1.1H PLUMBING PARTIAL FIRST FLOOR PLAN – AREA A
SCALE: 1/8" = 1'-0"

KEY PLAN

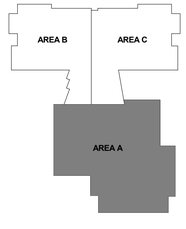

SETTY
ONE SOUTH STREET, SUITE 1130
BALTIMORE, MARYLAND 21202
TEL 667-329-5035
WASHINGTON DC | BALTIMORE | MONTGOMERY
ENERGY MANAGEMENT SERVICES • DESIGN BUILD SERVICES
CONSULTING • ENGINEERING • CONSTRUCTION MANAGEMENT
DISTRICT OF COLUMBIA • MARYLAND
www.SETTY.com
SA2017111 # # # #
PROJECT NUMBER

GRIMM AND PARKER
11720 Baltimore Drive
Suite 600
Calverton, MD 20705
Tel: 301.595.1000
www.grimmandparker.com
GP# 21553

PLUMBING PARTIAL FIRST FLOOR PLAN – AREA A

HOLABIRD ACADEMY PK-8
CITY OF BALTIMORE, MARYLAND

DATE	DESCRIPTION

P-1.1H

03/13/2017
BID SET

© GRIMM AND PARKER, P.C. 2014