© GRIMM AND PARKER, P.C. 2014

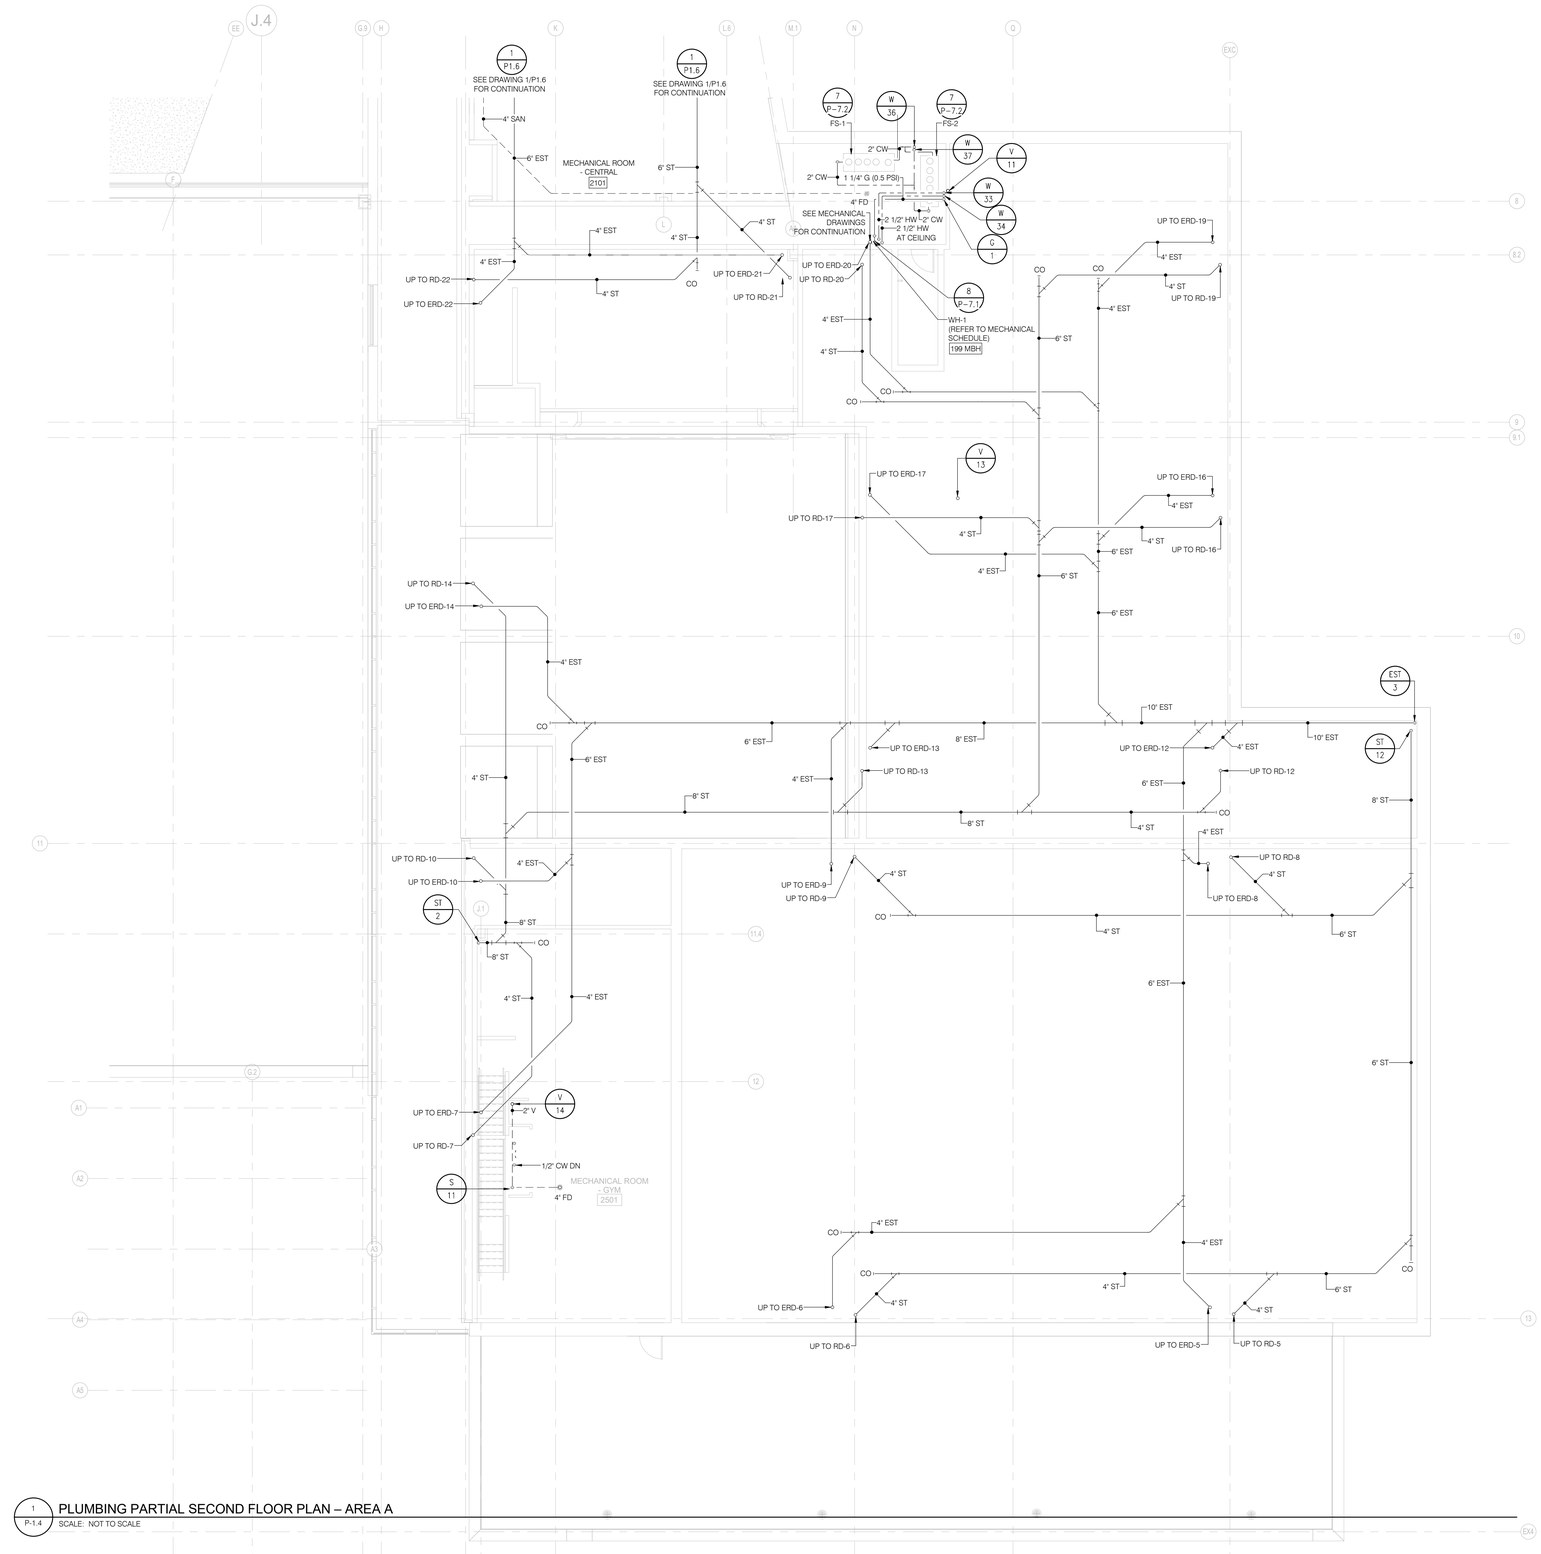

1 P-1.4 PLUMBING PARTIAL SECOND FLOOR PLAN – AREA A

SCALE: NOT TO SCALE

KEY PLAN

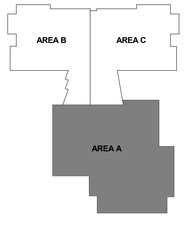

SETTY
ONE SOUTH STREET, SUITE 1130
BALTIMORE, MARYLAND 21202
TEL 667-329-5035
MAINTENANCE MANAGEMENT SERVICES • ENERGY MANAGEMENT
ENERGY MANAGEMENT SERVICES • DESIGN AND CONSTRUCTION
CITY OF COLUMBIA, MARYLAND
www.SETTY.com
SACOTY# # # # #
PROJECT NUMBER

11720 Beltsville Drive
Suite 600
Calverton, MD 20705
Tel: 301.595.1000
www.grimmandparker.com
GRIMM AND PARKER

GP# 21553

PLUMBING PARTIAL SECOND FLOOR PLAN - AREA A

HOLABIRD ACADEMY PK-8
CITY OF BALTIMORE, MARYLAND

DATE	DESCRIPTION

P-1.4

03/13/2017
BID SET

© GRIMM AND PARKER, P.C. 2014