© GRIMM AND PARKER, P.C. 2014

SHEET KEY NOTES

1. PROVIDE TRAP PRIMING TO ALL FLOOR DRAINS, FLOOR SINKS AND OPEN SITE DRAINS.
2. SEE AREA B ROOF PLAN FOR ROOF DRAIN DETAILS.
3. PROVIDE ACCESS PANELS TO ALL DOMESTIC SUPPLY VALVES.
4. PROVIDE ACCESS PANELS TO ALL WATER HAMMER ARERESTORS. REFER TO PLUMBING RISER DIAGRAM FOR WATER HAMMER ARRESTOR LOCATION.

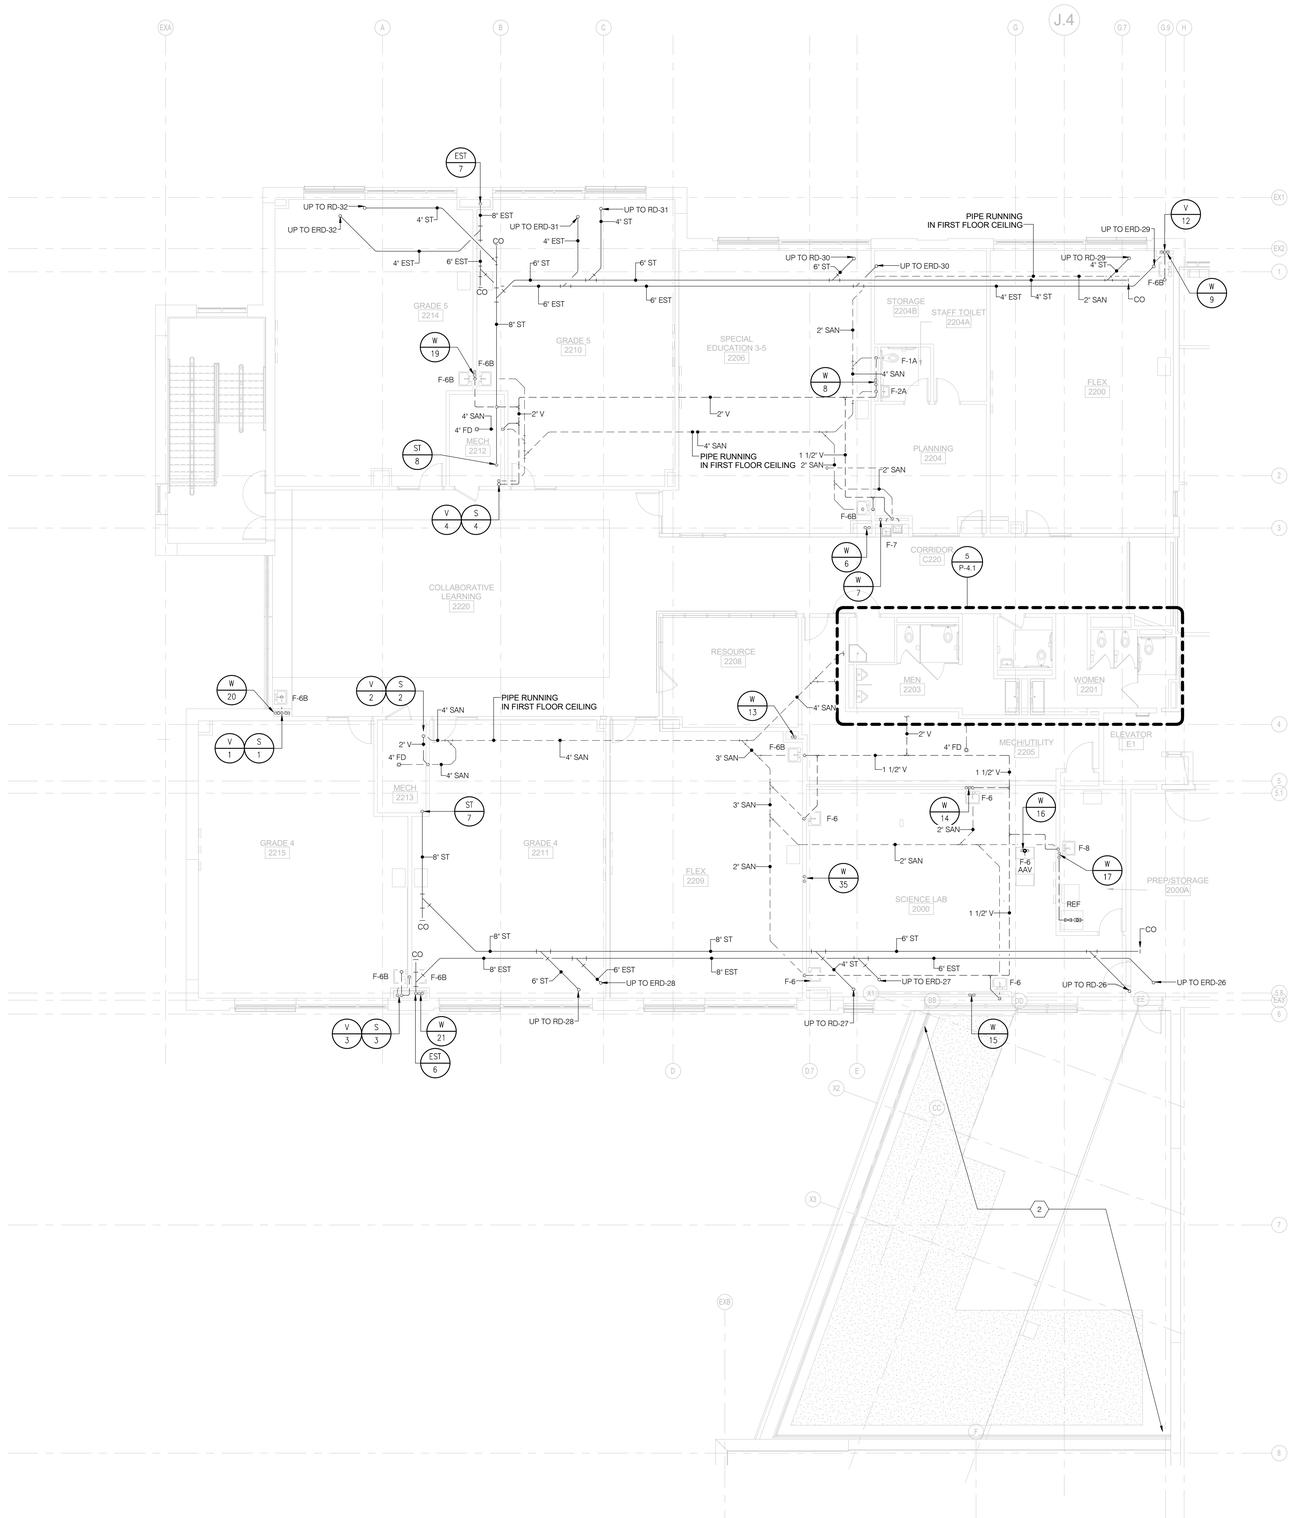

1 / P-1.5 PLUMBING PARTIAL SECOND FLOOR PLAN – AREA B
SCALE: 1/8" = 1'-0"

KEY PLAN

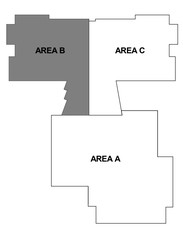

SETTY
ONE SOUTH STREET, SUITE 1130
BALTIMORE, MARYLAND 21202
TEL 667-329-6035
MAYOR'S OFFICE OF CAPITAL MANAGEMENT
ENERGY MANAGEMENT SERVICES • DESIGN & BUILD SERVICES
CAPITAL PROJECT MANAGEMENT • CONSTRUCTION MANAGEMENT
DISTRICT OF COLUMBIA • MARYLAND
www.SETTY.com

PROJECT NUMBER: SA2017-17 # # # #

11720 Beltsville Drive
Suite 600
Calverton, MD 20705
Tel: 301.595.1000
www.grimmandparker.com
GRIMM AND PARKER

GP# 21553

PLUMBING PARTIAL SECOND FLOOR PLAN – AREA B

HOLABIRD ACADEMY PK-8
CITY OF BALTIMORE, MARYLAND

DATE	DESCRIPTION

P-1.5

03/13/2017
BID SET

© GRIMM AND PARKER, P.C. 2014