© GRIMM AND PARKER, P.C. 2014

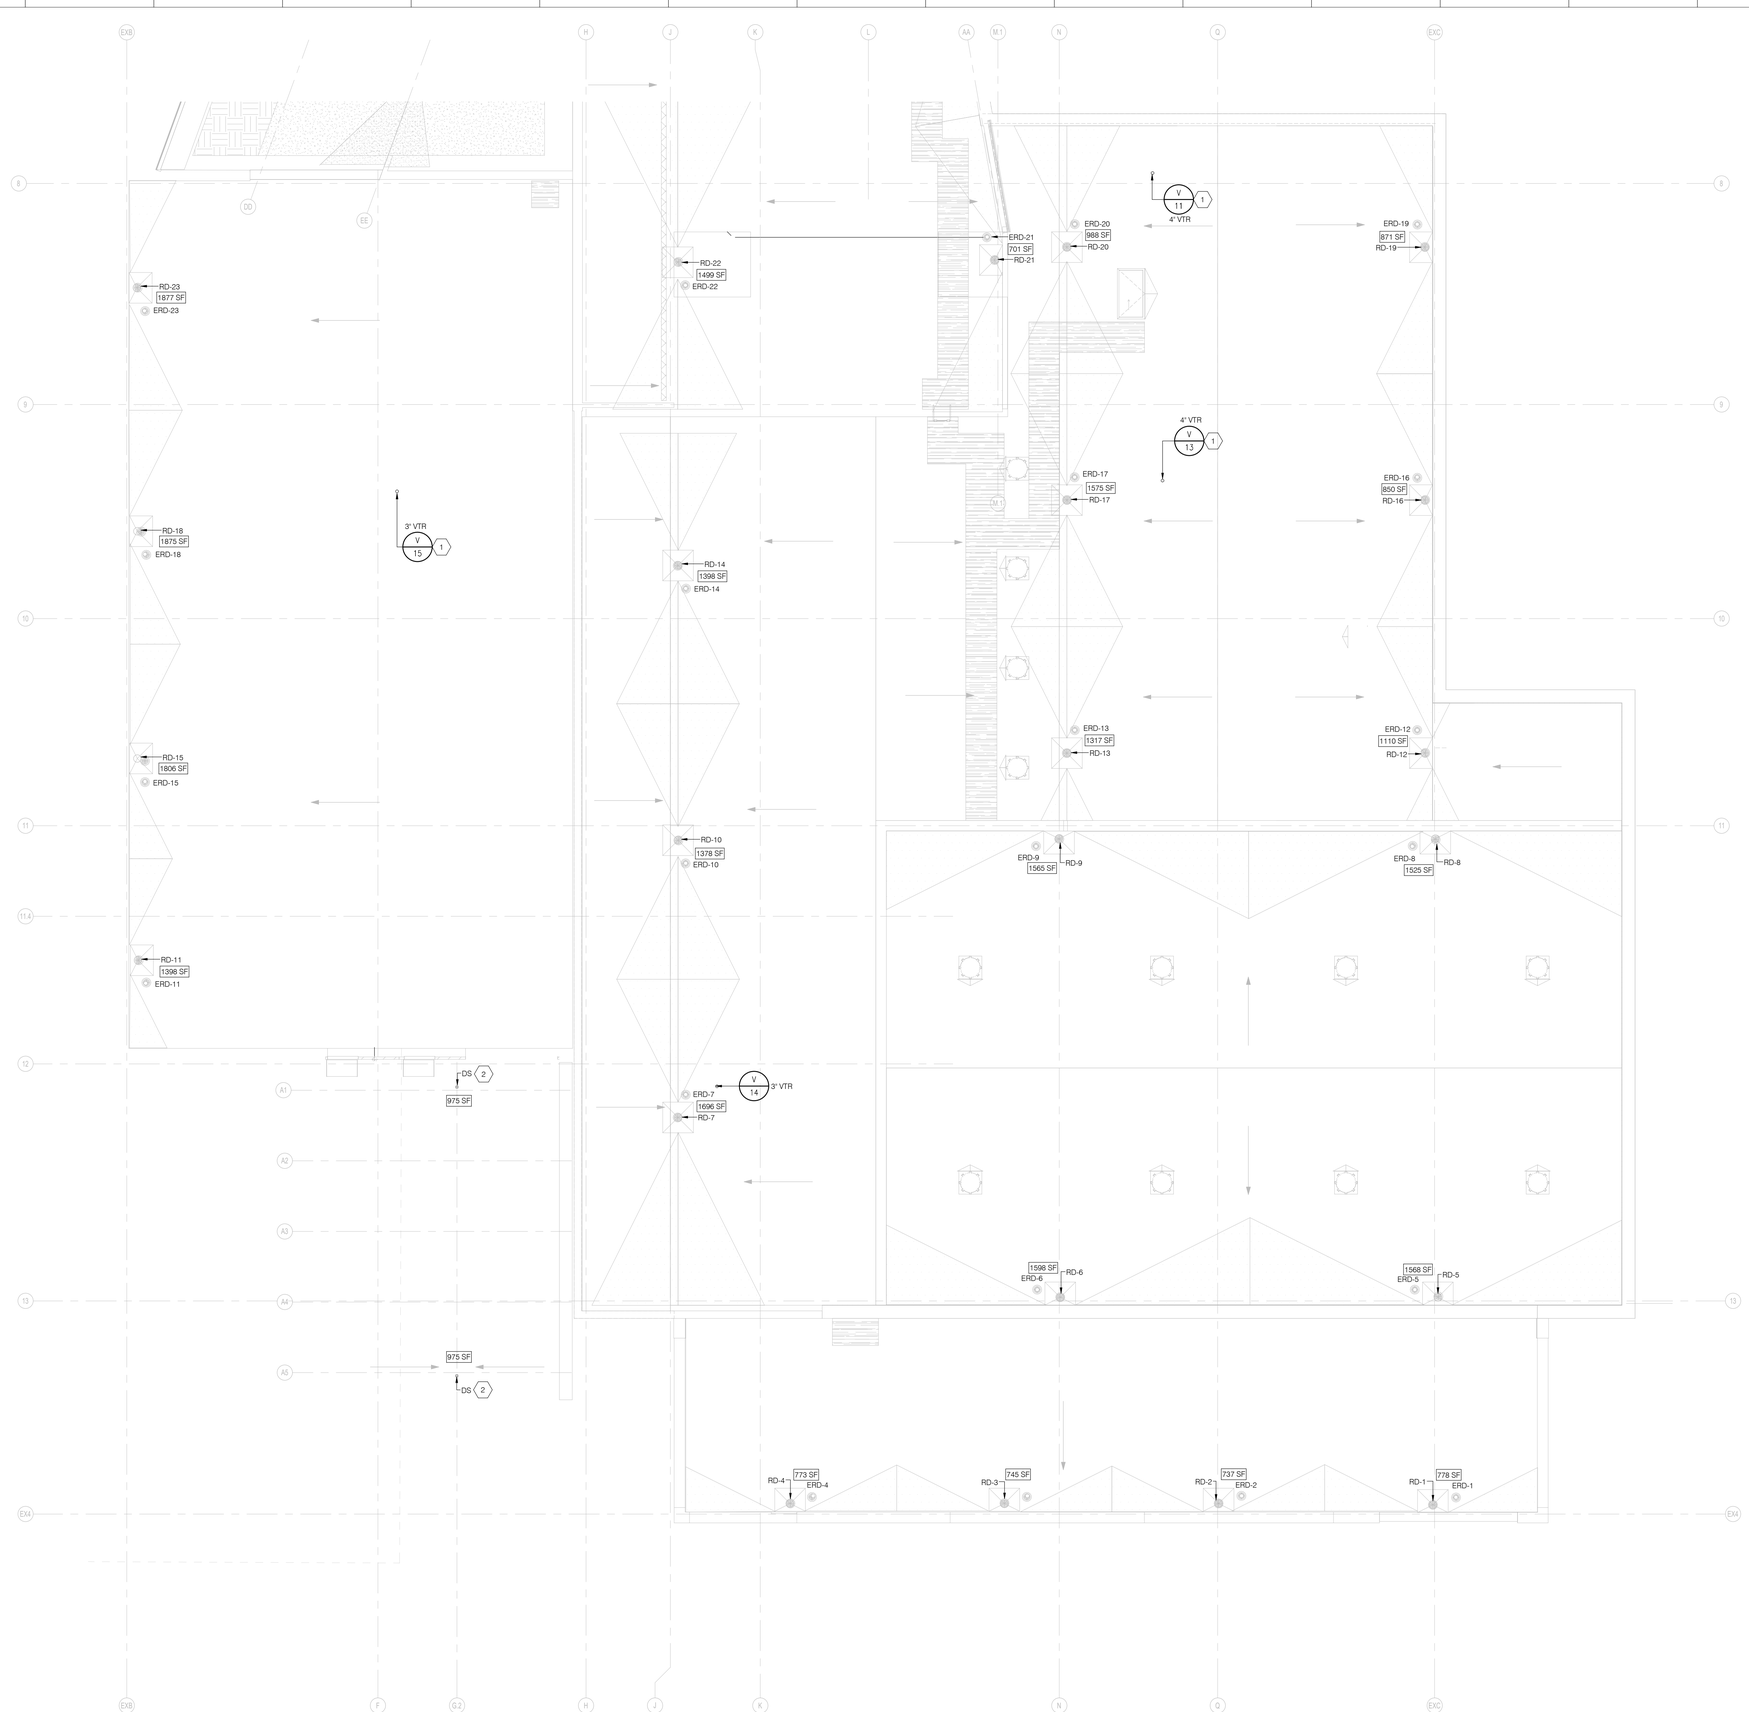

1 P-1.7H PLUMBING PARTIAL ROOF PLAN – AREA A

SCALE: 1/8" = 1'-0"

SHEET KEY NOTES

1. OFFSET SANITARY VENT IN CEILING SPACE BELOW IF NECESSARY AND PROVIDE MIN 10'-0" CLEARANCE FROM ANY MECHANICAL EQUIPMENT AND FRESH AIR INTAKE.
2. DOWNSPOUT TO BOOT AT GRADE FROM CANOPY GUTTER. REFER TO ARCHITECTURAL DRAWINGS FOR MORE DETAILS.

KEY PLAN

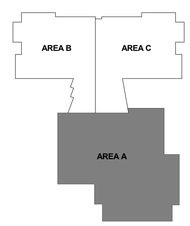

SETTY
ONE SOUTH STREET, SUITE 1130
BALTIMORE, MARYLAND 21202
TEL 667-329-6035
MAINTENANCE MANAGEMENT SERVICES • ENERGY MANAGEMENT
ENERGY MANAGEMENT SERVICES • DESIGN BUILD SERVICES
CONSULTING • ENGINEERING • DESIGN • CONSTRUCTION
DISTRICT OF COLUMBIA • MARYLAND
www.SETTY.com

PROJECT NUMBER: SA2017-F-R-F-F

11720 Baltimore Drive
Suite 600
Calverton, MD 20705
Tel: 301.595.1000
www.grimmandparker.com
GRIMM AND PARKER

GP# 21553

PLUMBING PARTIAL ROOF PLAN - AREA A

HOLABIRD ACADEMY PK-8
CITY OF BALTIMORE, MARYLAND

DATE	DESCRIPTION

P-1.7H

03/13/2017
BID SET

© GRIMM AND PARKER, P.C. 2014