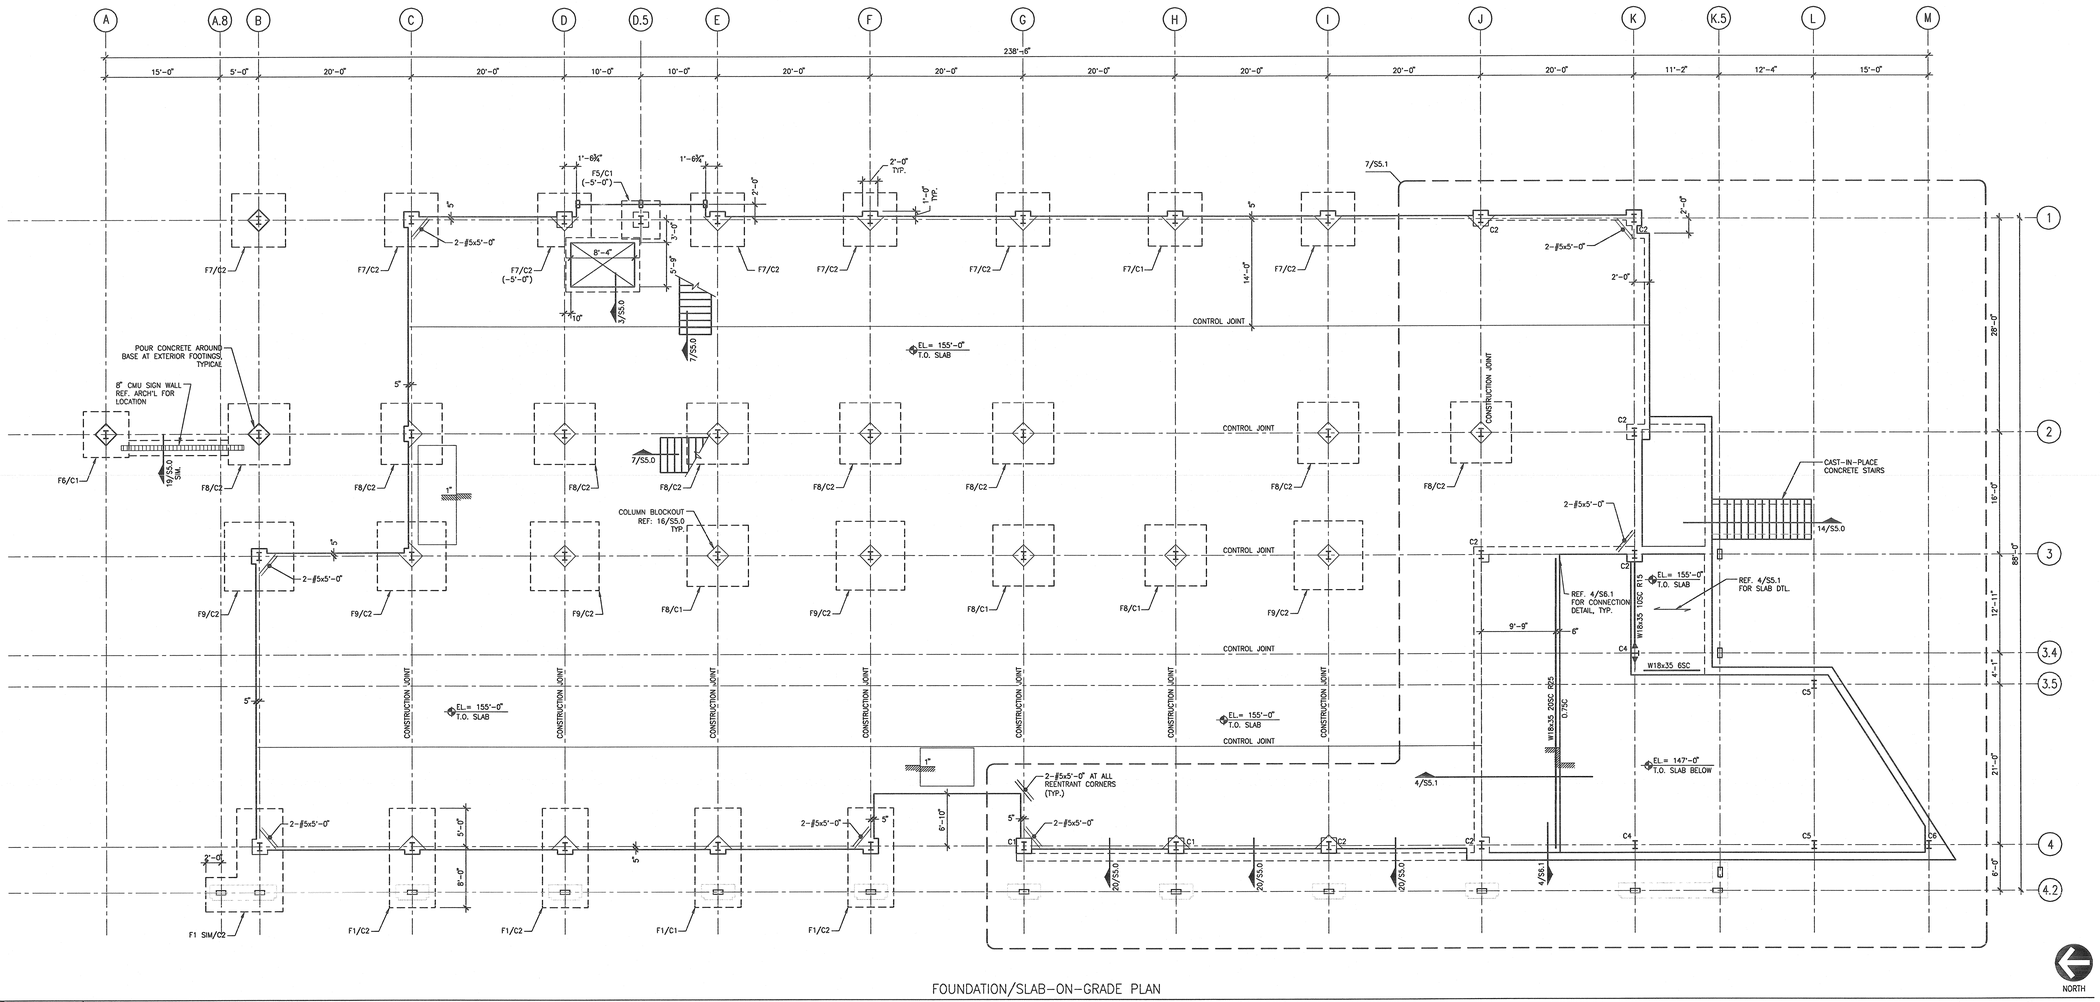

FOUNDATION/SLAB-ON-GRADE PLAN

1 1/8"=1'-0" | PLAN

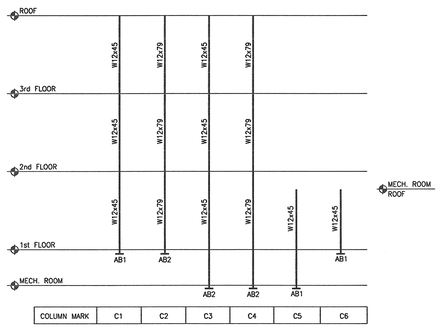

COLUMN MARK	C1	C2	C3	C4	C5	C6

NOTE:
1. BASE PLATES TO BE 20x20x1 GRADE 50, TYPICAL U.N.O. SEE 18/S5.0 FOR PLATE REQUIREMENTS AT CONCRETE PLINTHS.
2. REF. 13/S5.0 FOR ANCHOR BOLT SIZE.

COLUMN SCHEDULE

4 N.T.S. | SCHEDULE

SPREAD FOOTING SCHEDULE

MARK	SIZE IN PLAN	THICKNESS	REINFORCEMENT EA. WAY BOTTOM	REINFORCEMENT EA. WAY TOP
F1	6'-0"x13'-0"	18"	#9 @ 12	#6 @ 12
F5	5'-0"x5'-0"	18"	5-#5	5-#5
F6	6'-0"x6'-0"	18"	6-#6	6-#6
F7	7'-0"x7'-0"	18"	7-#6	7-#6
F8	8'-0"x8'-0"	24"	8-#7	8-#6
F9	9'-0"x9'-0"	24"	9-#7	9-#6
F10	10'-0"x10'-0"	28"	10-#8	10-#6

SPREAD FOOTING SCHEDULE

3 NONE | SCHEDULE

FOUNDATION / S.O.G. NOTES:
1. SLAB ON GRADE TO BE 5" THICK, 4000 PSI NORMAL WEIGHT CONCRETE REINFORCED WITH WWF 6x6-W2.9xW2.9 U.N.O. LONG STRIP CONSTRUCTION MUST BE USED, RE 2/S5.0.
2. TOP OF FOOTING ELEVATION TO BE 2'-0" BELOW TOP OF SLAB, TYPICAL U.N.O. WHERE T.O. FOOTING IS GREATER THAN 2'-0 BELOW T.O. SLAB, REF. 18/S5.0
3. SEE S5.0 FOR TYPICAL FOUNDATION AND SLAB ON GRADE DETAILS.
4. REFER TO ARCHITECTURAL DRAWINGS FOR EXTENT AND DIMENSIONS OF SLAB ON GRADE.
5. REFER TO ARCHITECTURAL DRAWINGS FOR EXTEND AND DIMENSIONS OF DEPRESSED SLAB AREAS, RAMPS AND SLOPES.
6. REFER TO ARCHITECTURAL DRAWINGS FOR ELEVATOR AND STAIR LOCATIONS AND DIMENSIONS.
7. REFER TO ARCHITECTURAL DRAWINGS FOR CMU WALL LOCATIONS.

FOUNDATION/S.O.G. NOTES

2 NONE | PLAN NOTES

M.E. RINKER, SR. SCHOOL OF BUILDING CONSTRUCTION
BCN

M.E. RINKER, Sr. HALL
SCHOOL OF BUILDING CONSTRUCTION

UNIVERSITY OF FLORIDA-GAINESVILLE
PROJECT NO. BR-191

ARCHITECTS
CROXTON COLLABORATIVE/
GOULD EVANS ASSOCIATES

CROXTON COLLABORATIVE ARCHITECTS
475 FIFTH AVENUE
NEW YORK, NY 10017
TEL 212.683.1998
FAX 212.683.2799

GOULD EVANS ASSOCIATES
5405 WEST CYPRESS STREET
TAMPA, FL 33607
TEL 813.288.0729
FAX 813.288.0231

MECHANICAL ENGINEERS
LEHR ASSOCIATES
130 WEST 30TH STREET
NEW YORK, NY 10001-4092
TEL 212.947.8050
FAX 212.957.2059

STRUCTURAL ENGINEERS
WALTER P. MOORE AND ASSOCIATES, INC.
Florida Engineering Business No. 3818
201 EAST KENNEDY BOULEVARD
TAMPA, FL 33602
TEL 813.221.2424
FAX 813.221.2289

CIVIL ENGINEERS
BROWN & CULLEN, INC.
3530 NW 43 STREET
GAINESVILLE, FL 32605
TEL 352.375.8999
FAX 352.375.0833

LANDSCAPE ENGINEERS
McCLAIN DESIGN GROUP, INC.
1843 NW 39 DRIVE
GAINESVILLE, FL 32605
TEL 352.372.2808
FAX 352.375.6622

CONSULTANT
SEEGY-BISCH
AUSSERE SULZBACHER STR. 118
NURNBERG, GERMANY
TEL 0911/59 90 99
FAX 0911/59 98 05

THIS DRAWING, AS AN INSTRUMENT OF SERVICE, IS AND SHALL REMAIN, PROPERTY OF CROXTON COLLABORATIVE ARCHITECTS. THIS DRAWING SHALL NOT BE REPRODUCED, PUBLISHED, USED ON OTHER PROJECTS, USED FOR ADDITIONS, OR USED IN COMPLETION OF THIS PROJECT BY OTHERS EXCEPT BY AGREEMENT IN WRITING. © 2001 CROXTON COLLABORATIVE ARCHITECTS/ GOULD EVANS ASSOCIATES.

NO.	ISSUE/REVISION	DATE

100% CONSTRUCTION DOCUMENTS

DRAWING NAME
FOUNDATION
SLAB-ON-GRADE PLAN

DATE 11-21-01
SCALE AS NOTED
DRAWN BY/CHECKED BY LMF/JLD
DRAWING NUMBER S1.0