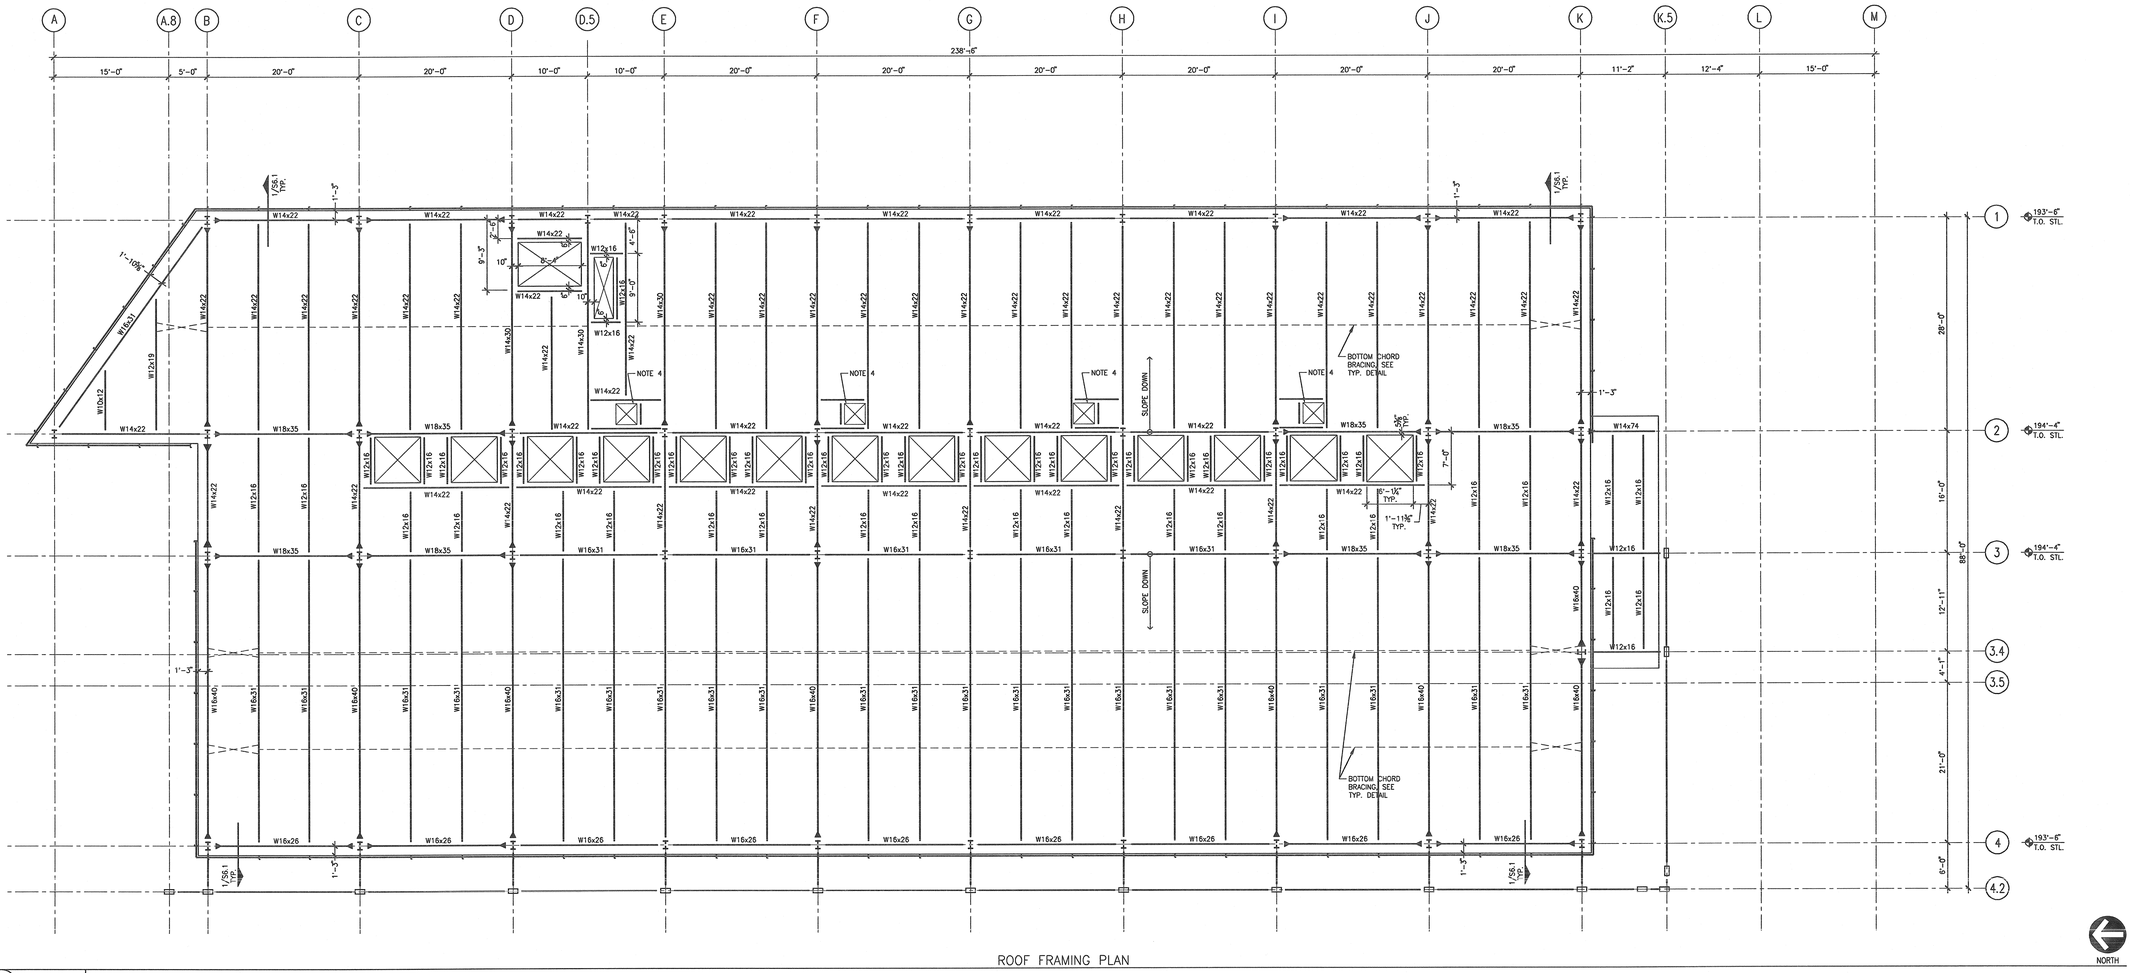


ROOF FRAMING PLAN

1 1/8" = 1'-0" | PLAN

ROOF NOTES:

1. ROOF SYSTEM CONSISTS OF 1 1/2" DEEP WIDE RIB, TYPE B, VENTED 20 GAGE GALVANIZED STEEL ROOF DECK WITH A G90 COATING. W/ 8 3/4" LIGHT WEIGHT INSULATING CONCRETE (28#/CF MAX.)
2. PROVIDE 1/4" BENT PLATE AT ALL EDGE OF DECK CONDITIONS, U.N.O.
3. ⊢— INDICATES COMPLETE PENETRATION MOMENT WELD.
4. REFER TO M.E.P. DRAWINGS FOR OPENINGS NOT SHOWN. OPENING SIZES ARE NOT FINAL AND MUST BE CONFIRMED WITH M.E.P. DRAWINGS. REFER TO ARCHITECTURAL DRAWINGS FOR DIMENSIONS NOT SHOWN. SEE TYPICAL FRAMING DETAILS.
5. >< - - - INDICATES L2x2x3/16 WELD TO BOTTOM FLANGE TYP. EXCEPT AT ENDS PROVIDE CROSS BRACES BETWEEN TOP AND BOTTOM FLANGE SIMILAR TO DETAIL 18/S6.0
6. PROVIDE W8x13 HOIST BEAM AS REQ'D BY ELEV. MFR.

ROOF NOTES

2 NONE | PLAN NOTES

M.E. RINKER, SR. SCHOOL OF BUILDING CONSTRUCTION

# M.E. RINKER, Sr. HALL
## SCHOOL OF BUILDING CONSTRUCTION

UNIVERSITY OF FLORIDA-GAINESVILLE
PROJECT NO. BR-191


ARCHITECTS
CROXTON COLLABORATIVE/
GOULD EVANS ASSOCIATES

CROXTON COLLABORATIVE ARCHITECTS
475 FIFTH AVENUE
NEW YORK, NY 10017
TEL 212.683.1998
FAX 212.683.2799

GOULD EVANS ASSOCIATES
5405 WEST CYPRESS STREET
TAMPA, FL 33607
TEL 813.288.0729
FAX 813.288.0231

MECHANICAL ENGINEERS
LEHR ASSOCIATES
130 WEST 30TH STREET
NEW YORK, NY 10001-4092
TEL 212.947.8050
FAX 212.967.2059

STRUCTURAL ENGINEERS
WALTER P. MOORE AND ASSOCIATES, INC.
Florida Engineering Business No. 3818
201 EAST KENNEDY BOULEVARD
TAMPA, FL 33602
TEL 813.221.2424
FAX 813.221.2289

CIVIL ENGINEERS
BROWN & CULLEN, INC.
3530 NW 43 STREET
GAINESVILLE, FL 32605
TEL 352.375.8999
FAX 352.375.0833

LANDSCAPE ENGINEERS
McCLAIN DESIGN GROUP, INC.
1843 NW 39 DRIVE
GAINESVILLE, FL 32605
TEL 352.372.2808
FAX 352.375.6622

CONSULTANT
SEEGY-BISCH
AUSSERE SULZBACHER STR. 118
NURNBERG, GERMANY
TEL 0911/59 90 99
FAX 0911/59 98 05



THIS DRAWING, AS AN INSTRUMENT OF SERVICE, IS AND SHALL REMAIN, PROPERTY OF CROXTON COLLABORATIVE ARCHITECTS. THIS DRAWING SHALL NOT BE REPRODUCED, PUBLISHED, USED ON OTHER PROJECTS, USED FOR ADDITIONS, OR USED IN COMPLETION OF THIS PROJECT BY OTHERS EXCEPT BY AGREEMENT IN WRITING. © 2001 CROXTON COLLABORATIVE ARCHITECTS/ GOULD EVANS ASSOCIATES.


| NO. | ISSUE/REVISION | DATE |
|---|---|---|

100% CONSTRUCTION DOCUMENTS

DRAWING NAME
ROOF FRAMING PLAN

DATE 11-21-01
SCALE AS NOTED
DRAWN BY/CHECKED BY LMR/JLD
DRAWING NUMBER S4.0